


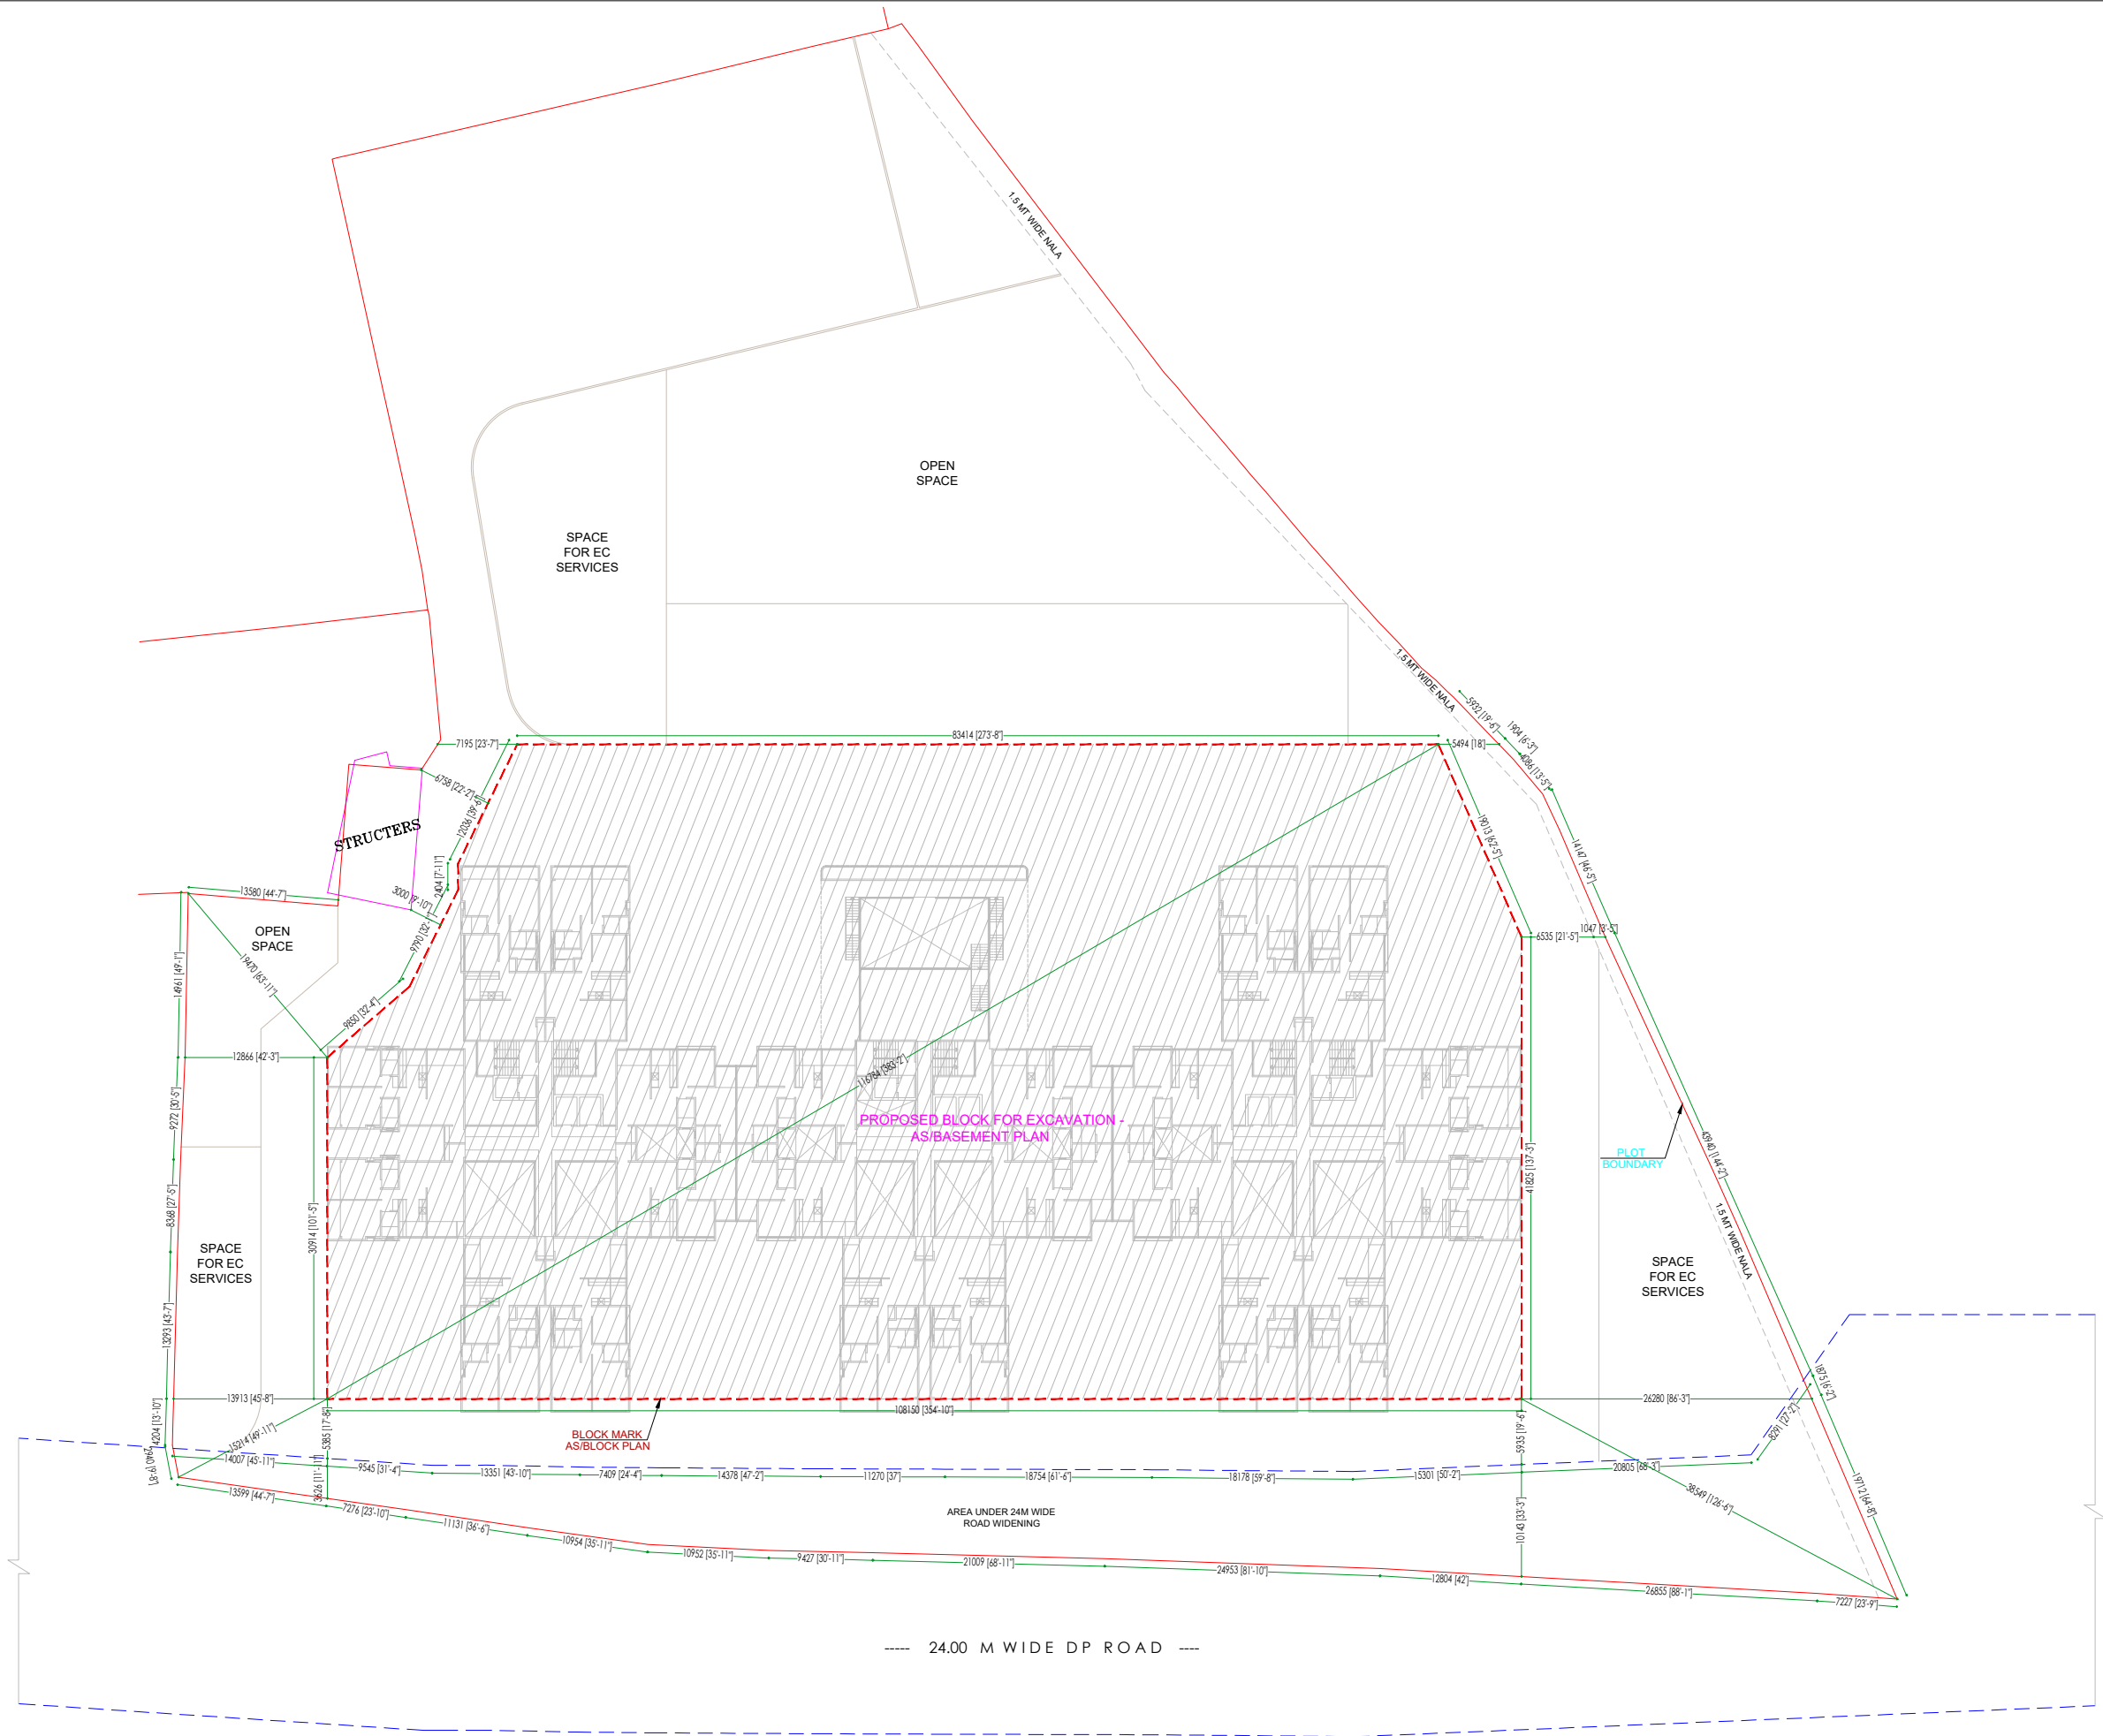

Notes:

- 01) DO NOT SCALE FROM THIS DRAWING ONLY WRITTEN DIMENSIONS SHOULD BE FOLLOWED.

02) ALL DIMENSIONS ARE IN MM UNLESS OTHERWISE SPECIED.

03) ALL EXTERNAL AND INTERNAL WALLS ARE 150MM THIK UNLESS OTHERWISE SPECIED.

04) WALLS HAVING THICKNESS OTHER THAN 150MM ARE SHOWN IN DIFFERENT HATCHES.

05) TOILET SLAB IS 250MM SUNK.

06) SLAB OF ALL TERRACES IS 150 MM SUNK.

07) SUNKEN PORTION IS SHOWN HATCHED.

08) FOR POSITION OF -V-REFER TOILET DETAILS.
- 09) CONTRACTORS MUST CHECK & VERIFY THE DRAWING BEFORE EXECUTION AND DISCREPANCY IF ANY MUST BE REPORTED TO THE ARCHITECT.

10) FOR SIZES OF STRUCTURAL ELEMENTS PLEASE REFER STRUCTURAL CONSULTANTS' CURRENT DRAWING.

11) FOR DRAINAGE, PLUMBING, ELECTRICAL & LANDSCAPE DETAILS, PLEASE REFER CONSULTANTS'DRAWING.

12) CHANGES/DEVIATIONS MADE ON SITE WITHOUT CONSULTING THE ARCHITECT WILL BE AT THE TOTAL RESPONSIBILITY OF THE CLIENTS.

REV-1					Client Company & Name
REV-2					MR. RAVI TINGRE
REV-3					Job Title
REV-4					PROPOSED MIX USED BUILDING AT SR.NO. 37&39, KONDHWA KH, DIST - PUNE
REV-5					Drawing Title
REV-6					Block Plan
REV	DETAILS	DRAWN	CHKD	DATE	Scale
					-
					Drawn by
					TEJAL
					Checked by
					AJAY SIR
					Date
					11-12-2025
					Job no.
					Drawing no
					Revision
					Status