



A.V. ROOM ELEVATION AT A

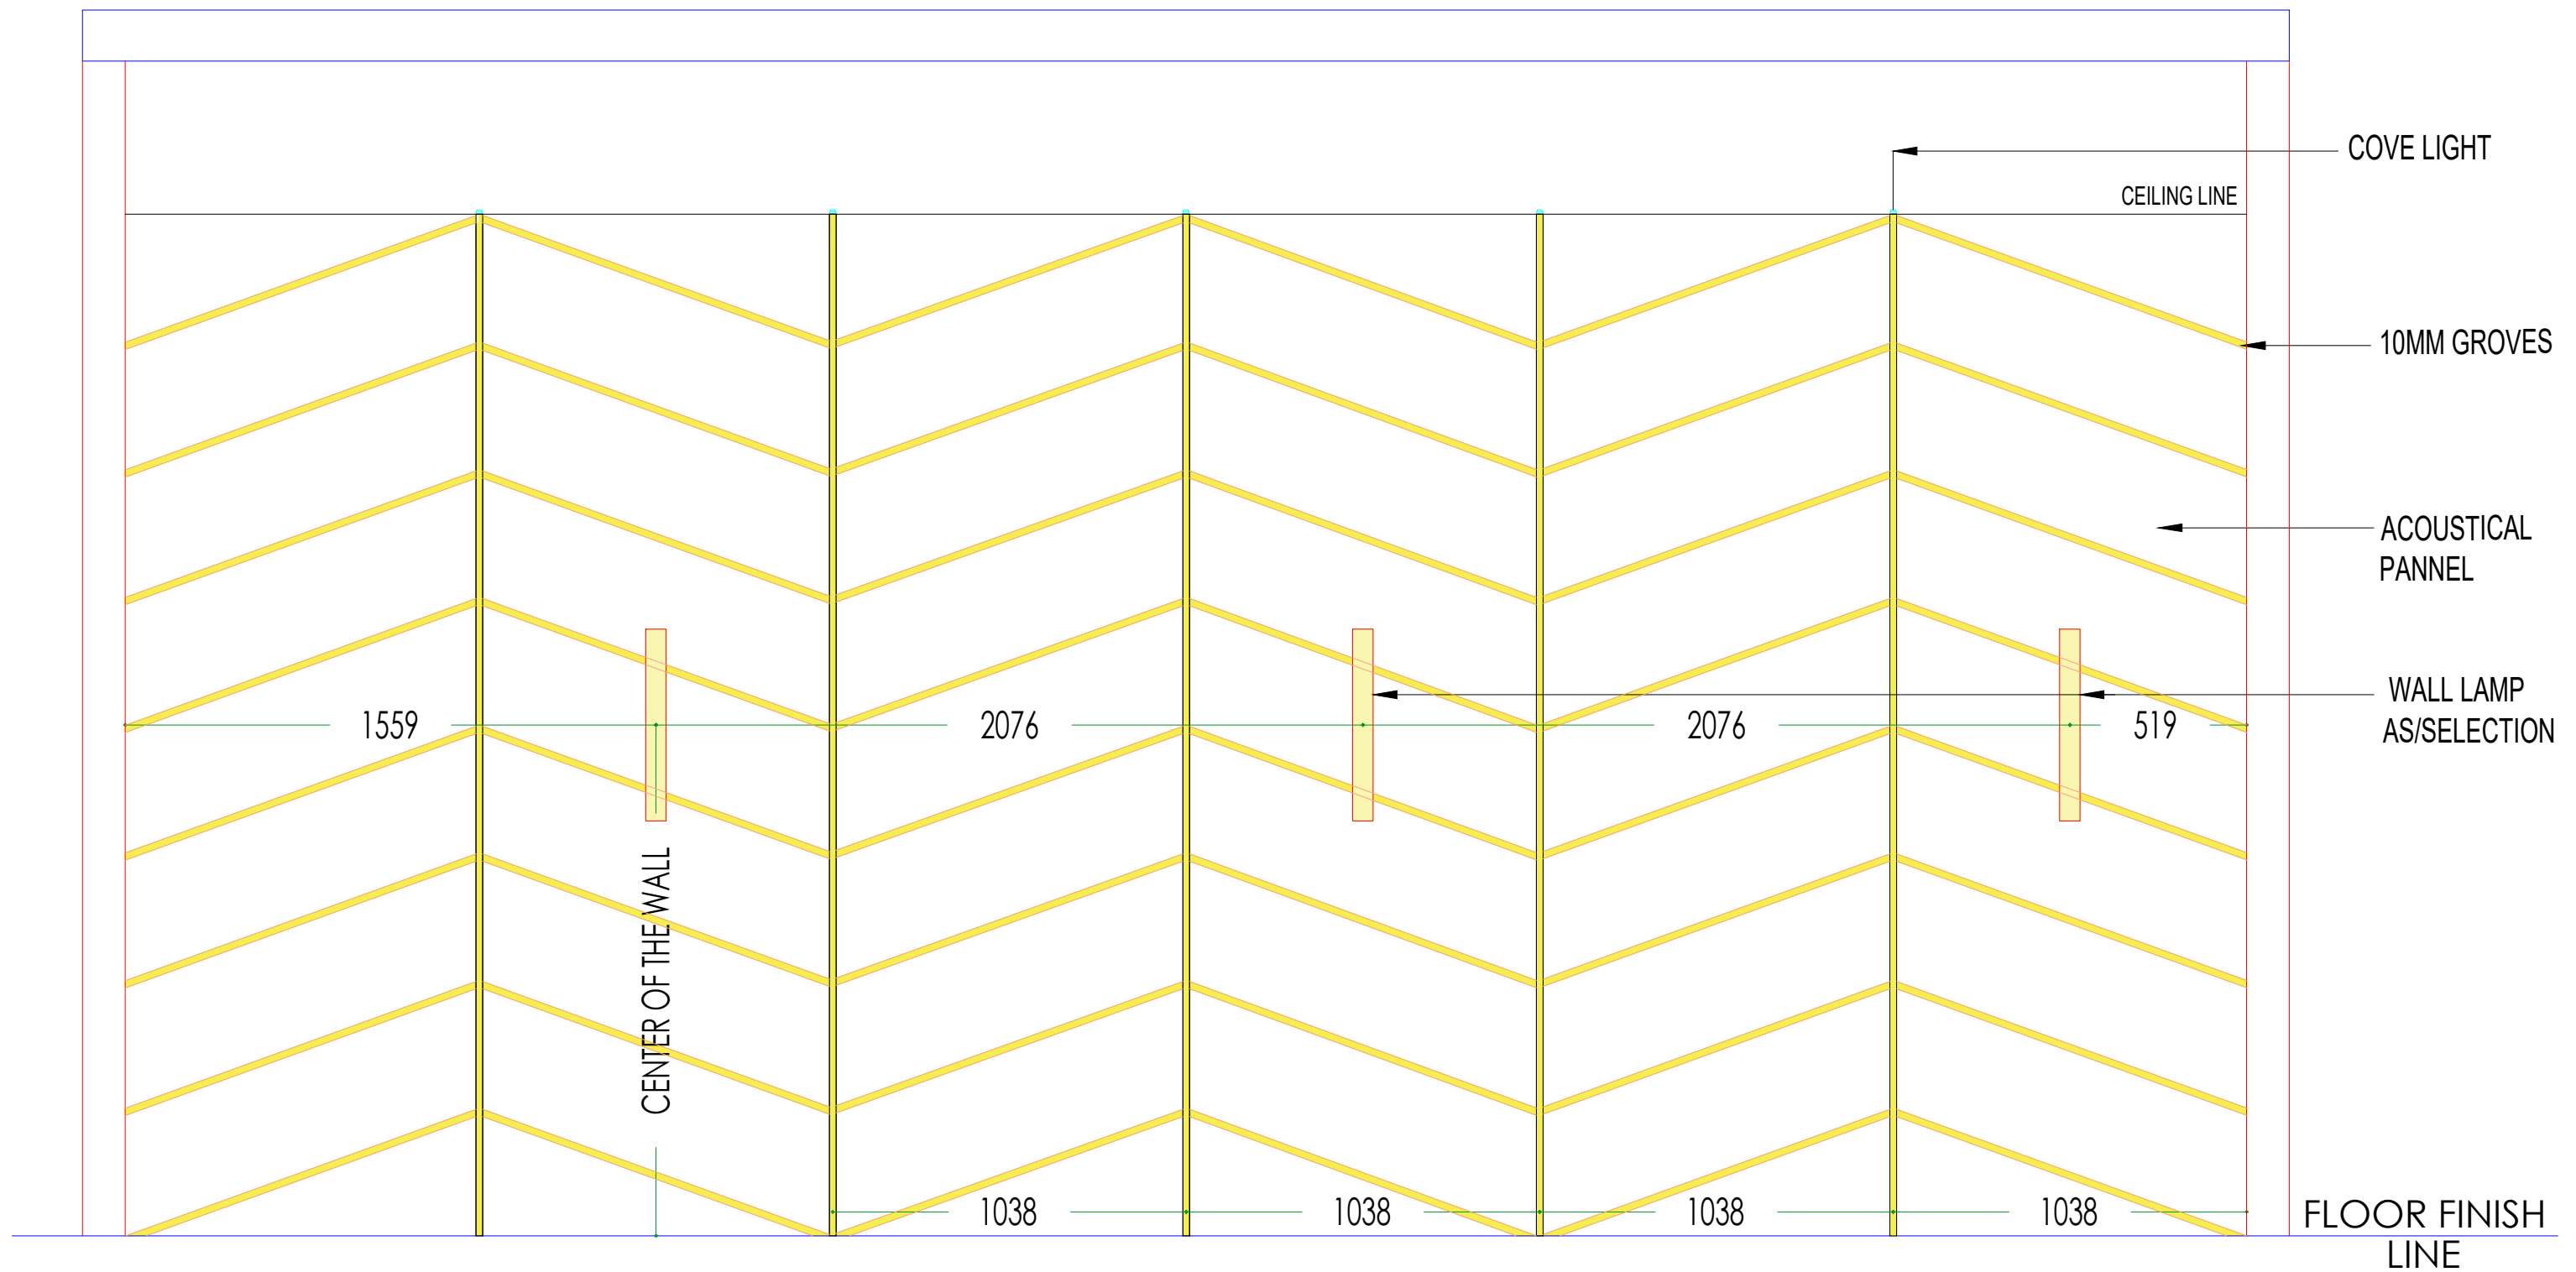

					Client Company & Name
					MR. RAVI TINGRE
					Job Title
					PROPOSED MIX USED BUILDING AT SR.NO. 37 & 39 KONDHWA KH
					Drawing Title Scale
					WALL ELEVATION N.T.S
					Drawn by Checked by Date
					TEJAL 13/12/2025
					Job no. Drawing no Revision

REV	DETAILS	DRAWN	CHKD	DATE	Status


A.V. ROOM
ELEVATION AT B

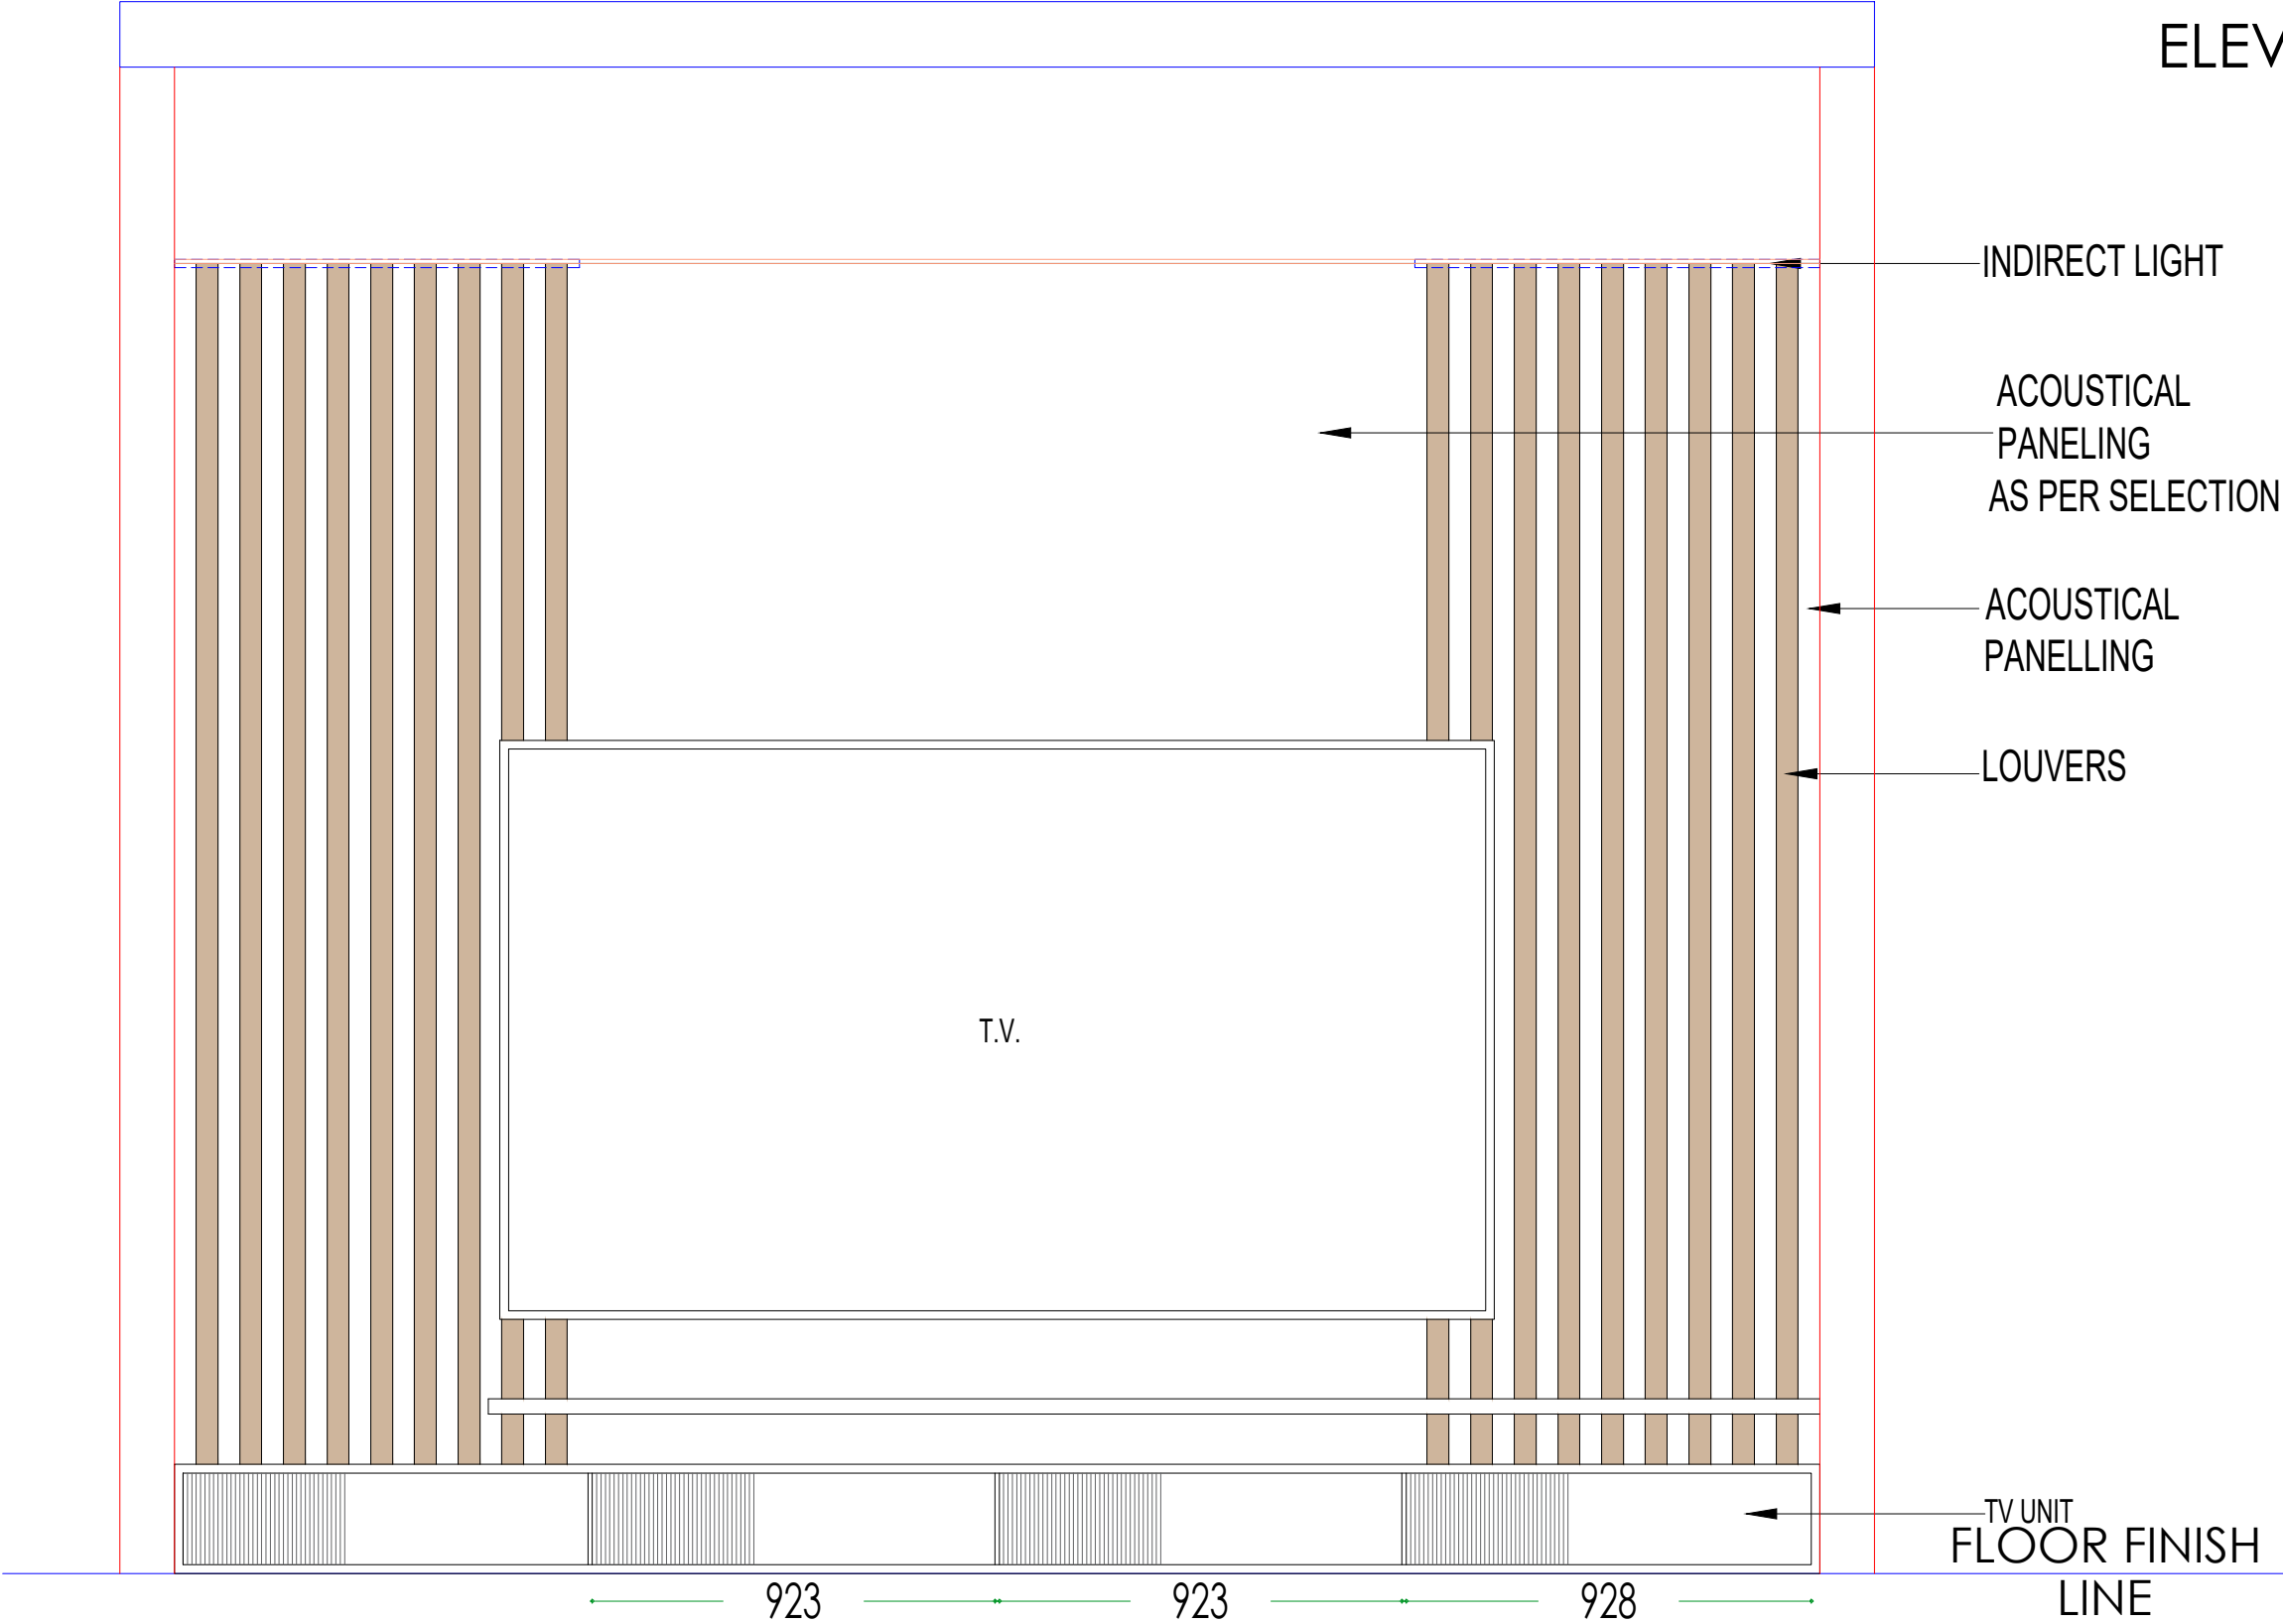

					Client Company & Name
					MR. RAVI TINGRE
					Job Title
					PROPOSED MIX USED BUILDING AT SR.NO. 37 & 39 KONDHWA KH
					Drawing Title
					WALL ELEVATION
					Scale
					N.T.S
					Drawn by
					TEJAL
					Checked by
					Date
					13/12/2025
					Job no.

					Drawing no
					Revision
					Status
REV	DETAILS	DRAWN	CHKD	DATE	


A.V. ROOM
ELEVATION AT C

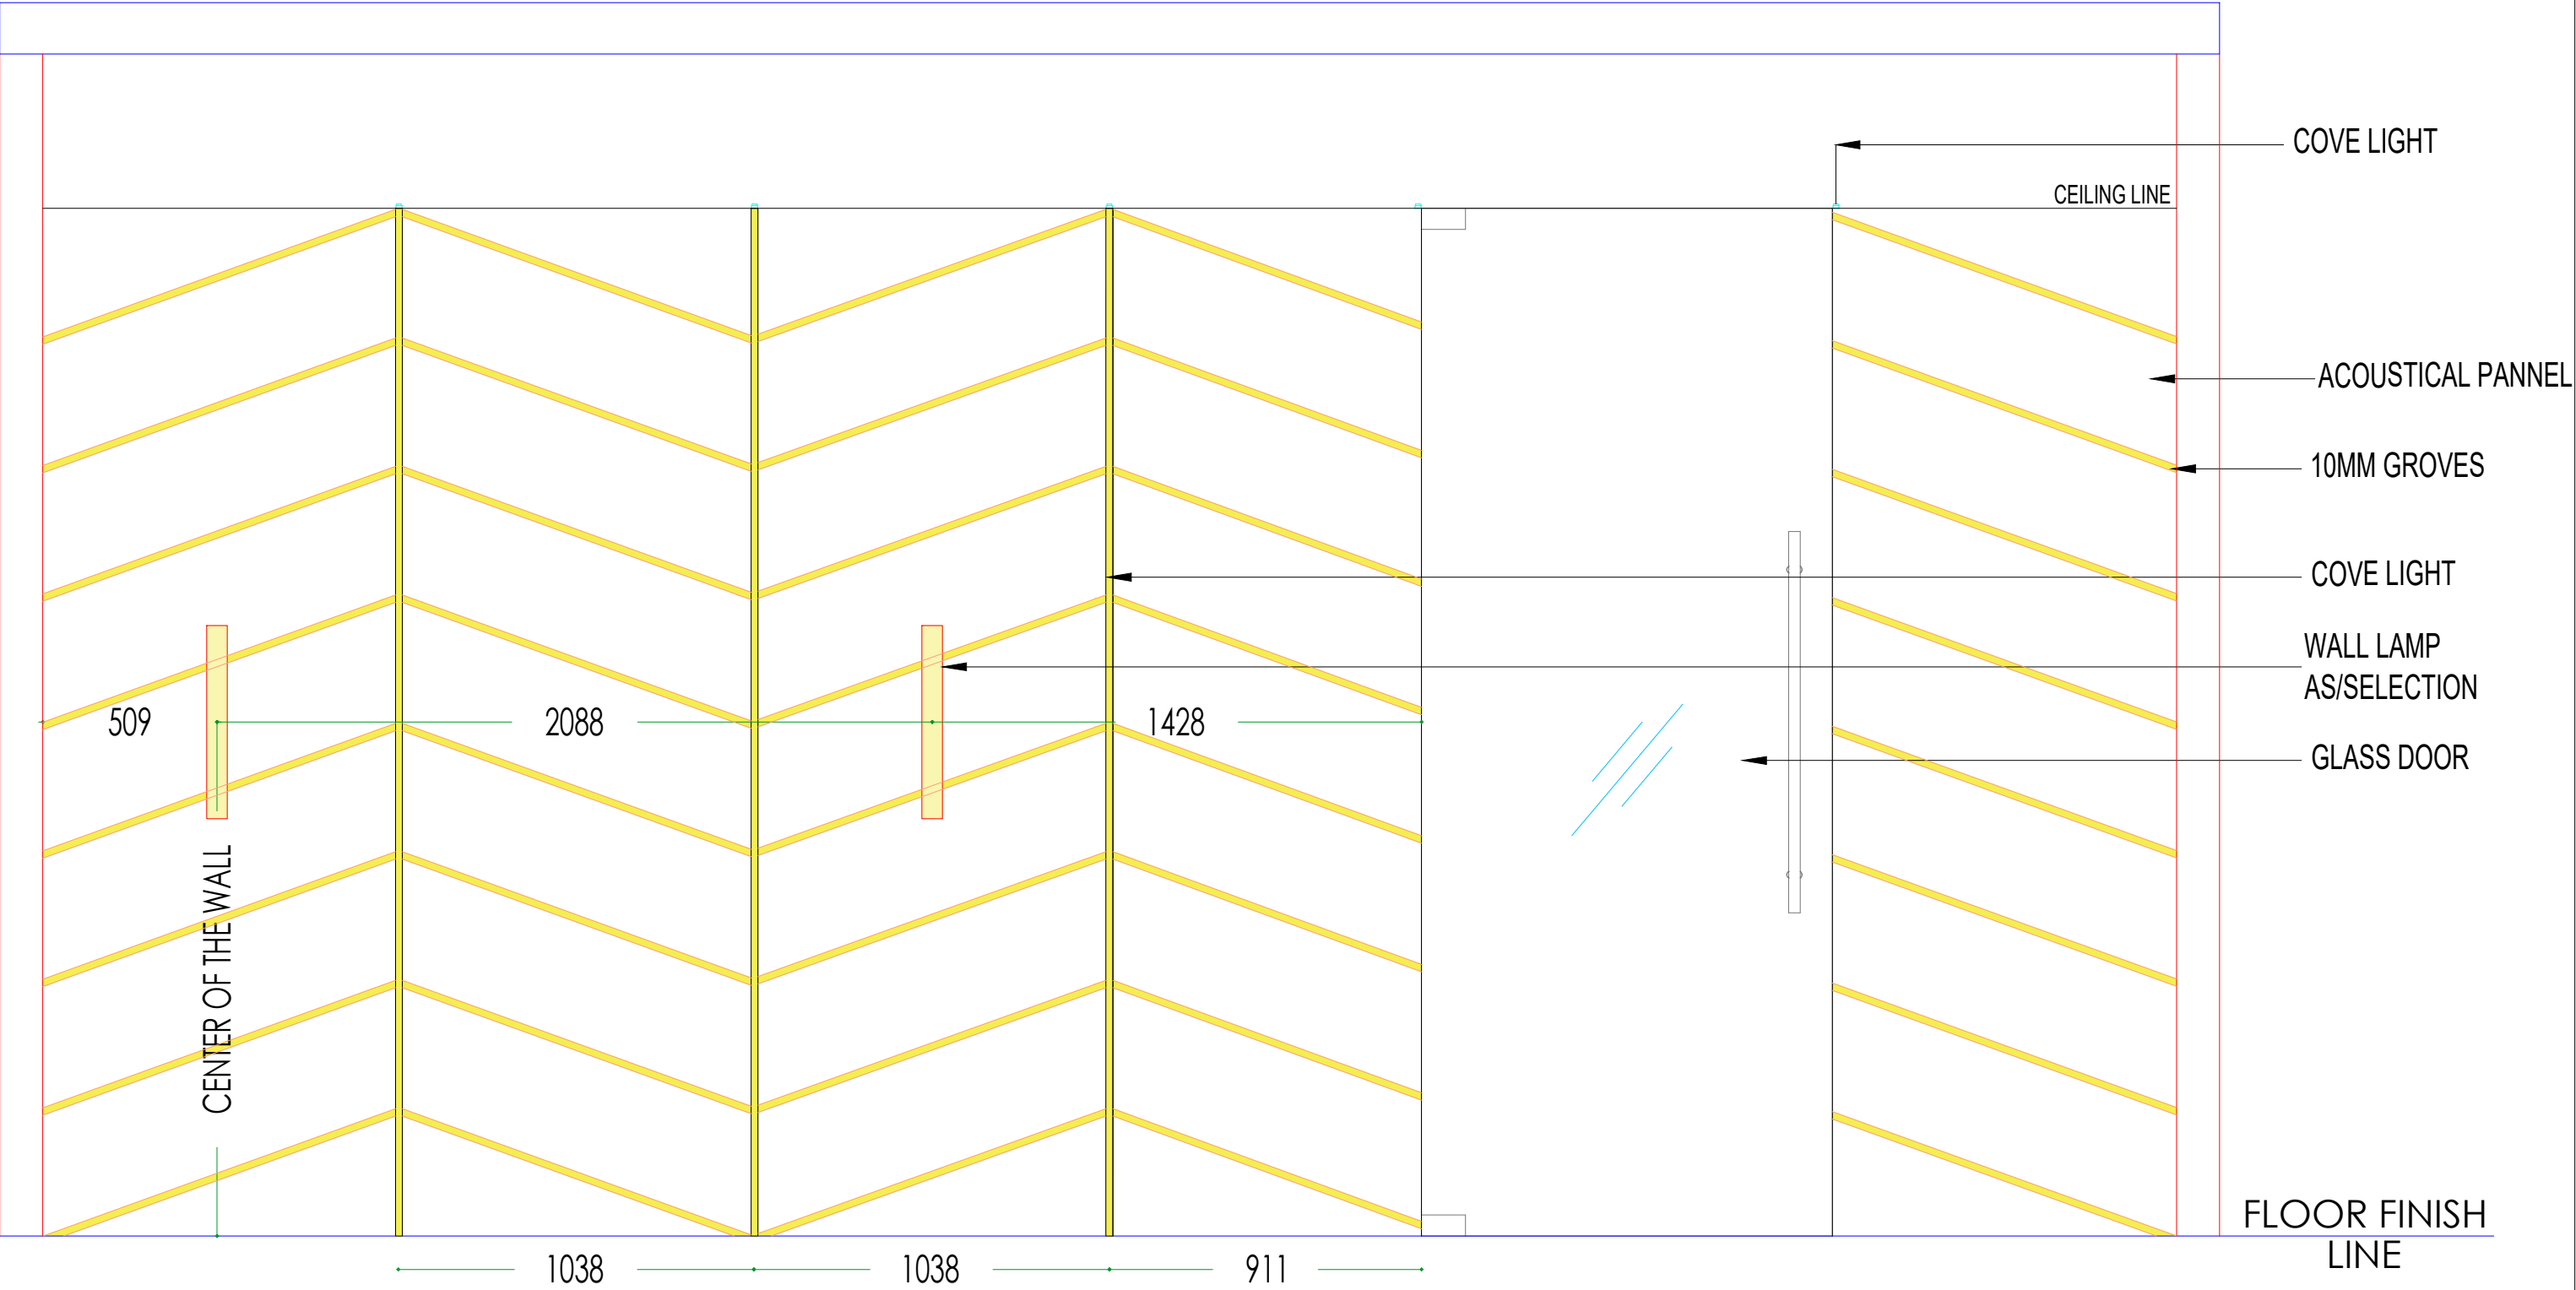

					Client Company & Name
					MR. RAVI TINGRE
					Job Title
					PROPOSED MIX USED BUILDING AT SR.NO. 37 & 39 KONDHWA KH
					Drawing Title
					WALL ELEVATION
					Scale
					N.T.S
					Drawn by
					TEJAL
					Checked by
					Date
					13/12/2025
					Job no.

					Drawing no
					Revision
					Status
REV	DETAILS	DRAWN	CHKD	DATE	


A.V. ROOM
ELEVATION AT D

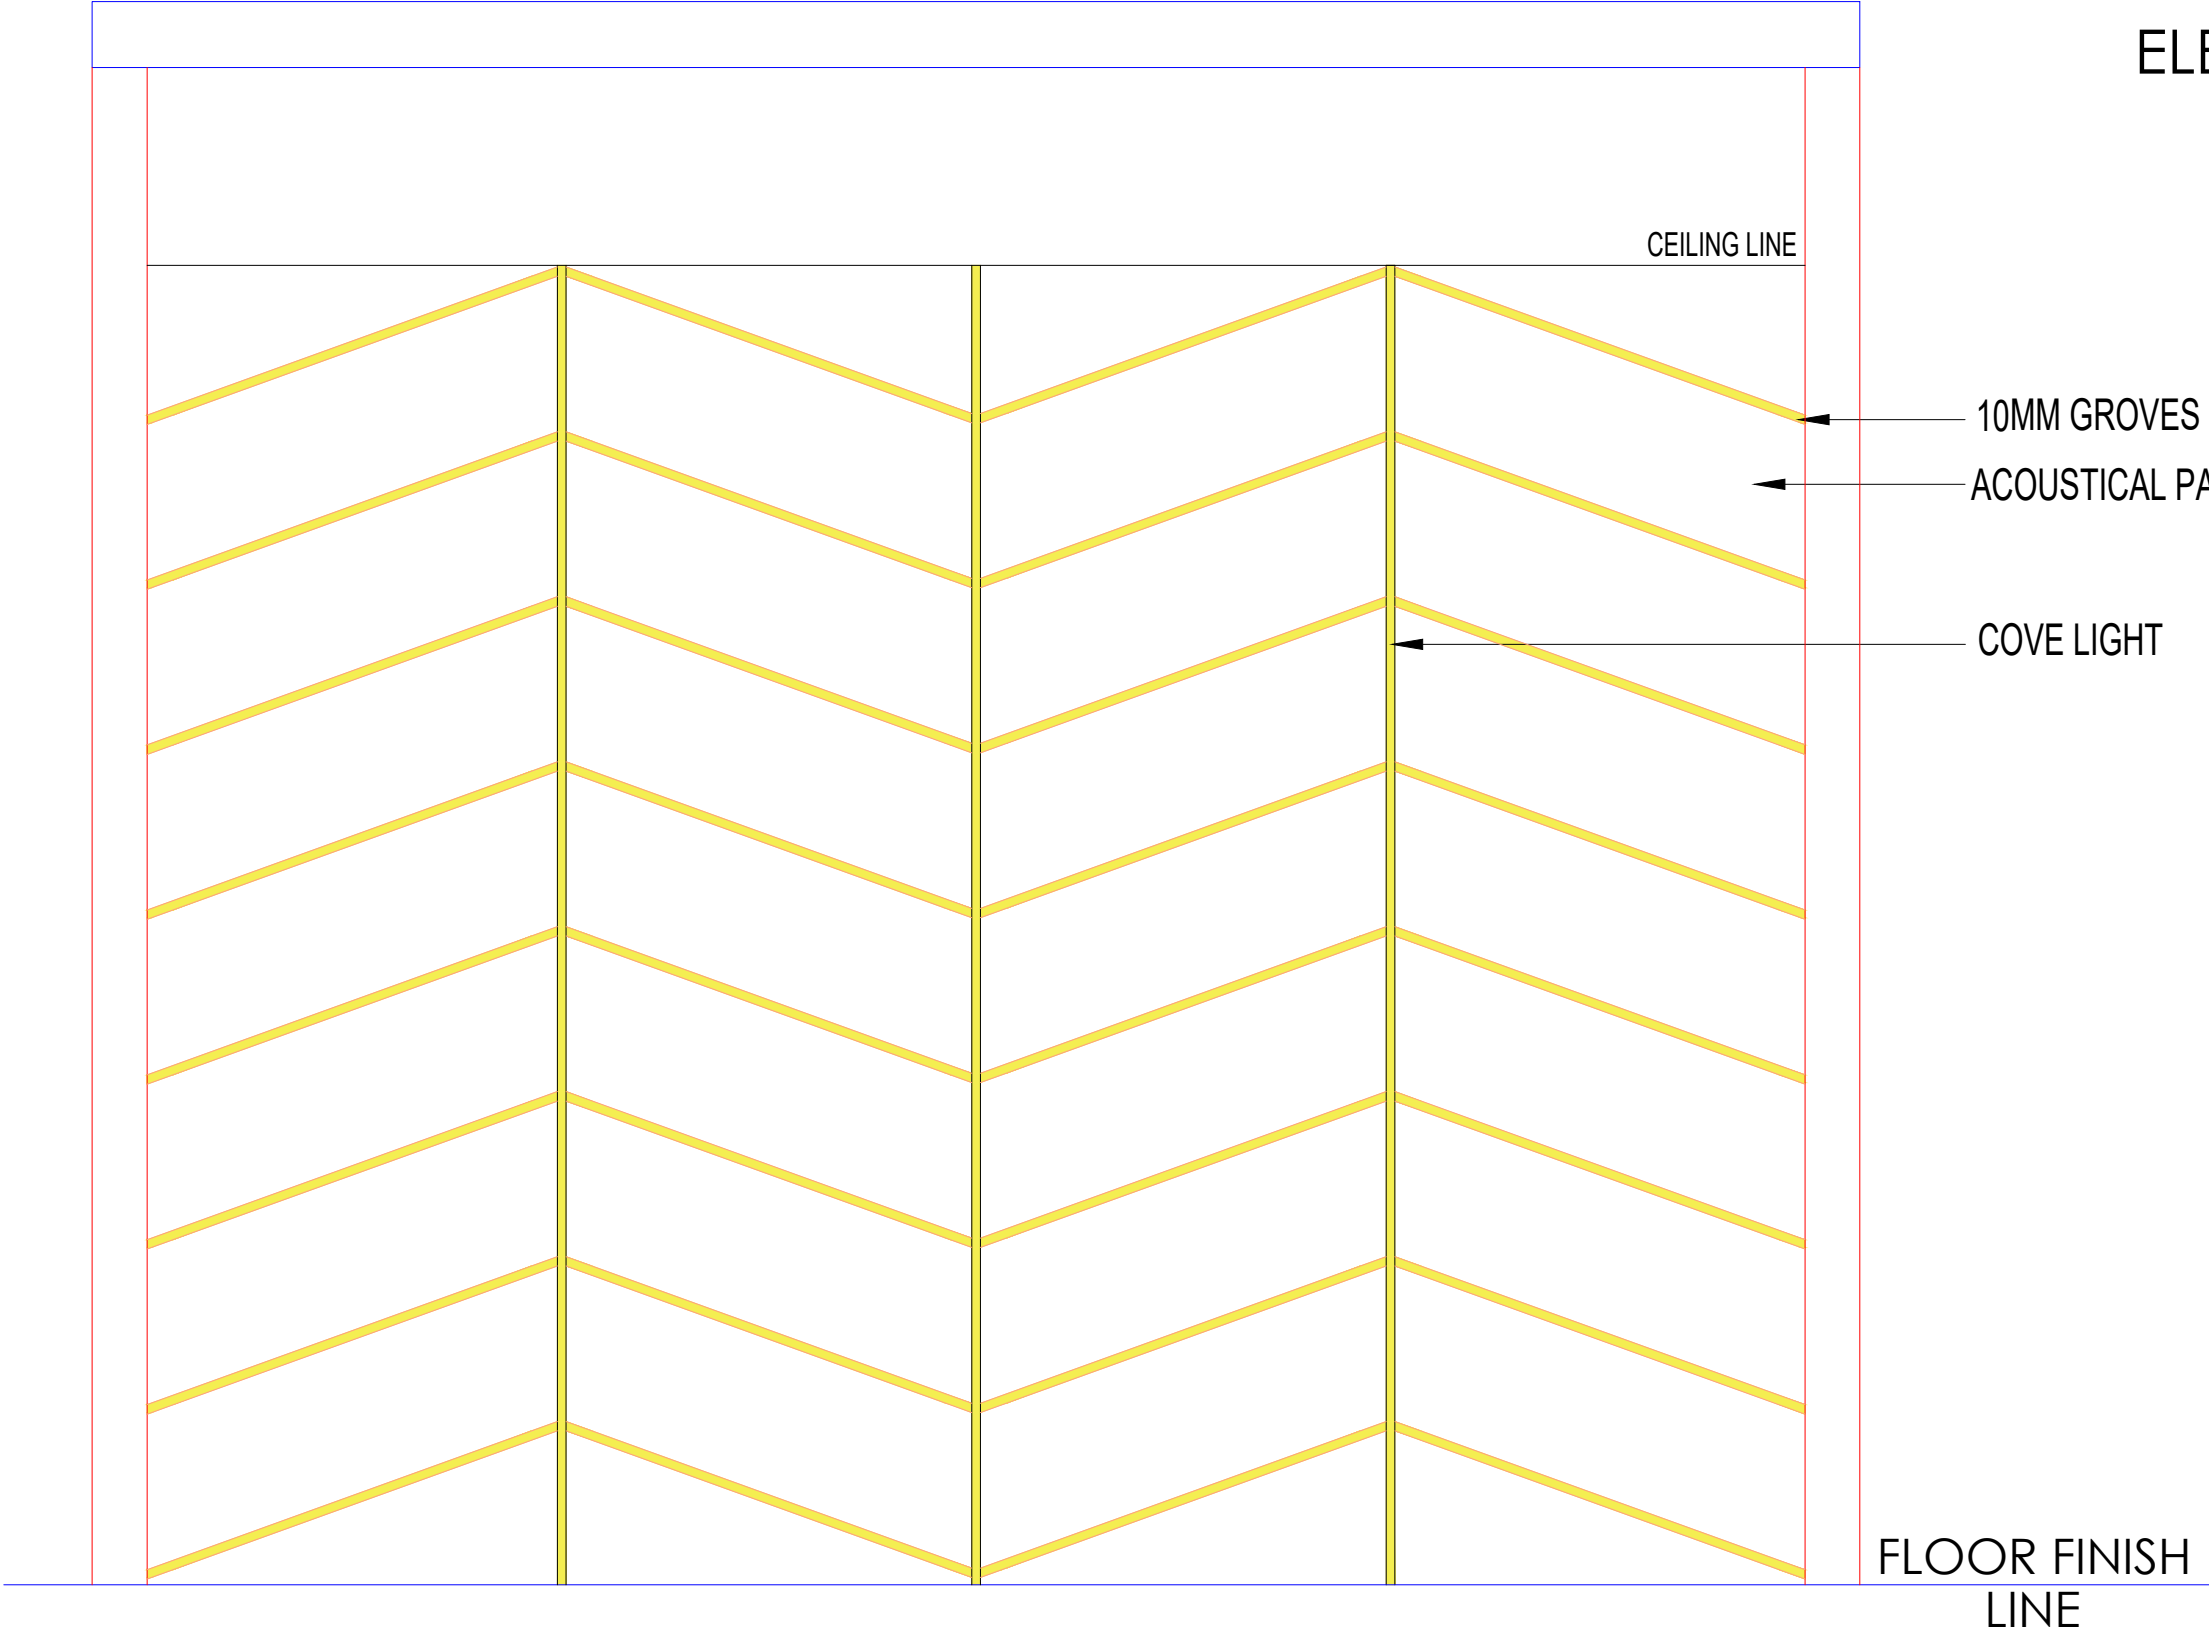

					Client Company & Name
					MR. RAVI TINGRE
					Job Title
					PROPOSED MIX USED BUILDING AT SR.NO. 37 & 39 KONDHWA KH
					Drawing Title
					WALL ELEVATION
					Scale
					N.T.S
					Drawn by
					TEJAL
					Checked by
					Date
					13/12/2025
					Job no.

					Drawing no
					Revision
					Status
REV	DETAILS	DRAWN	CHKD	DATE	


C.E.O. CABIN 01 & REST ROOM
ELEVATION A

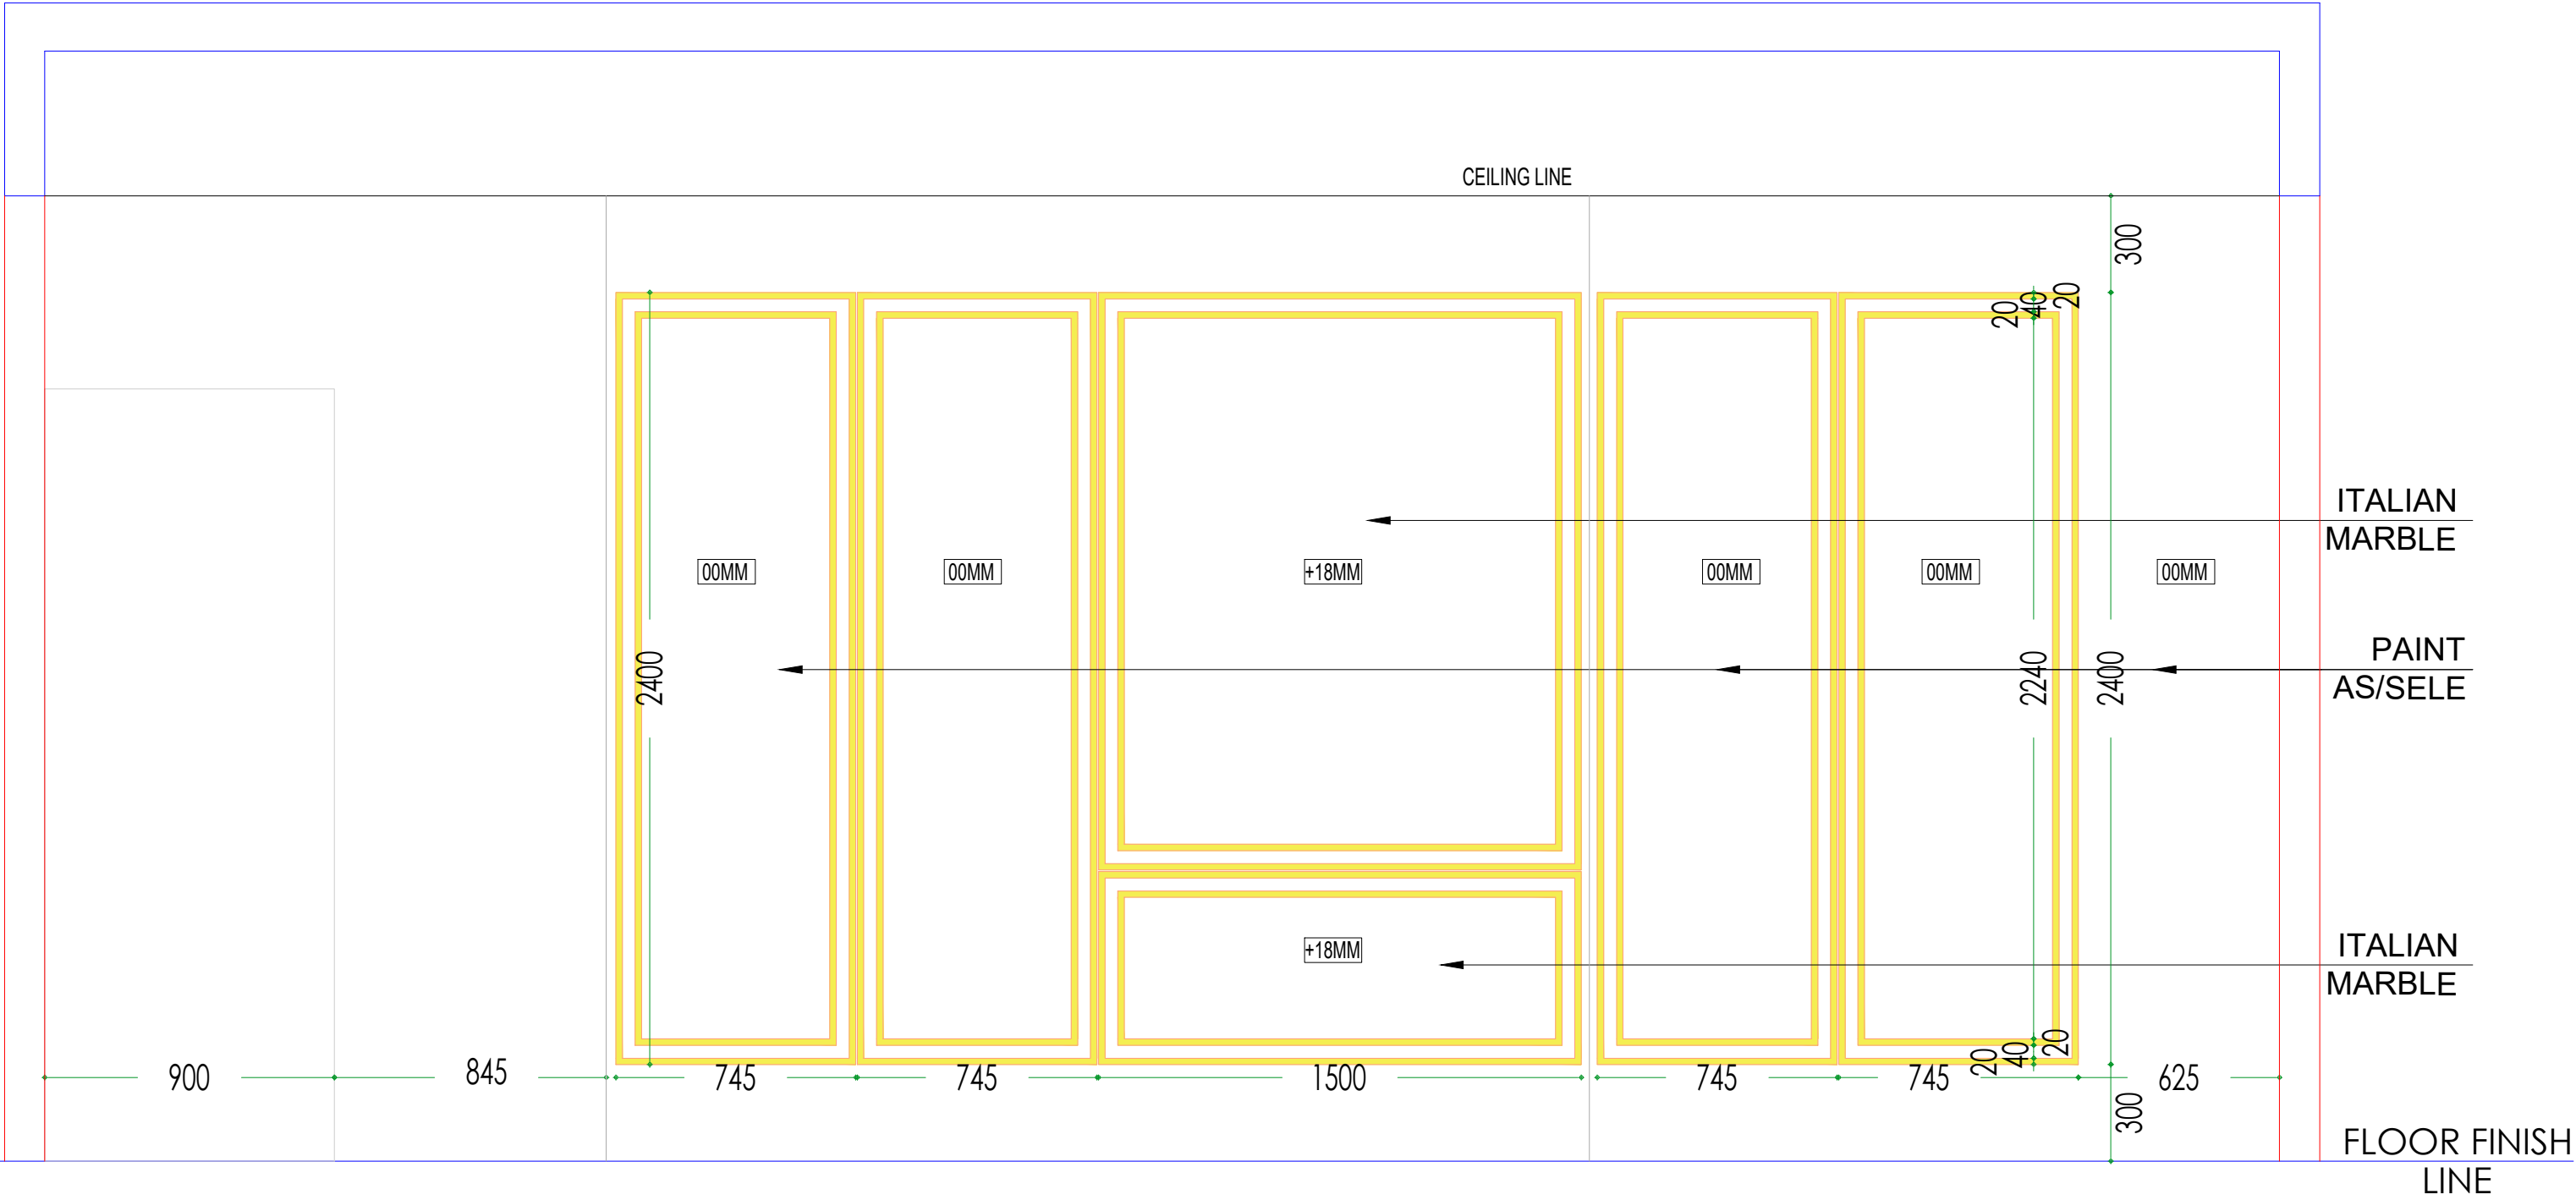

					Client Company & Name
					MR. RAVI TINGRE
					Job Title
					PROPOSED MIX USED BUILDING AT SR.NO. 37 & 39 KONDHWA KH
					Drawing Title
					WALL ELEVATION
					Scale
					N.T.S
					Drawn by
					TEJAL
					Checked by
					Date
					13/12/2025
					Job no.

					Drawing no
					Revision
REV	DETAILS	DRAWN	CHKD	DATE	Status


C.E.O. CABIN 01 & REST ROOM
ELEVATION B

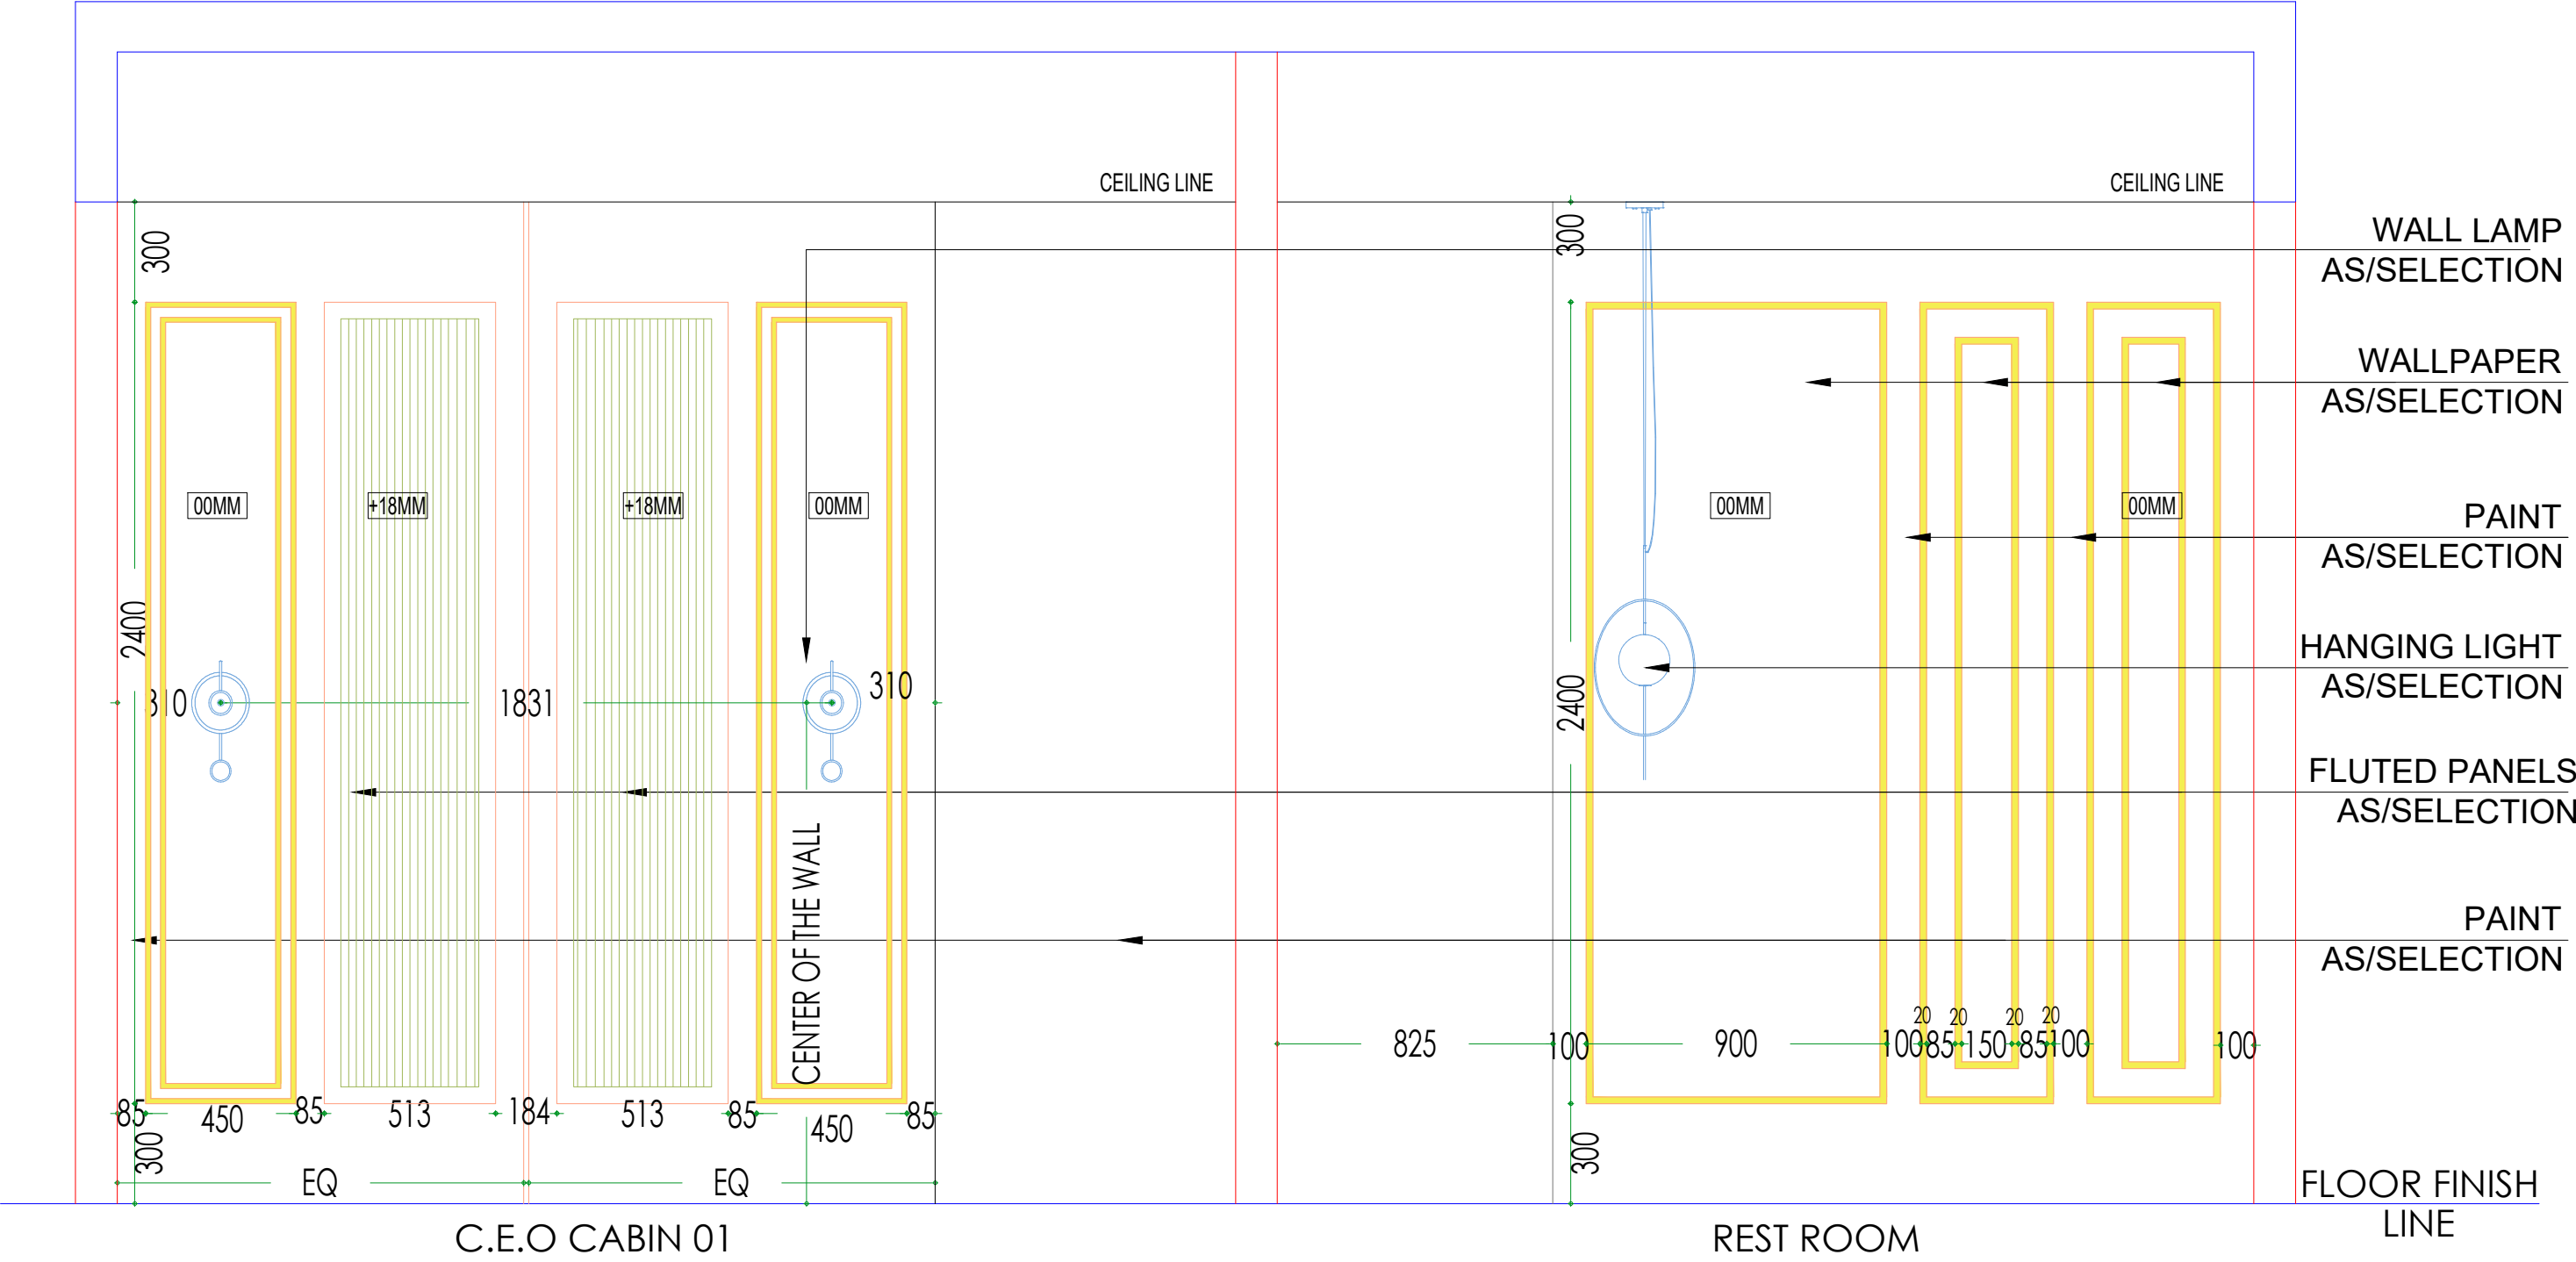

					Client Company & Name
					MR. RAVI TINGRE
					Job Title
					PROPOSED MIX USED BUILDING AT SR.NO. 37 & 39 KONDHWA KH
					Drawing Title
					WALL ELEVATION
					Scale
					N.T.S
					Drawn by
					TEJAL
					Checked by
					Date
					13/12/2025
					Job no.

					Drawing no
					Revision
					Status
REV	DETAILS	DRAWN	CHKD	DATE	


C.E.O. CABIN 01 & REST ROOM
ELEVATION C

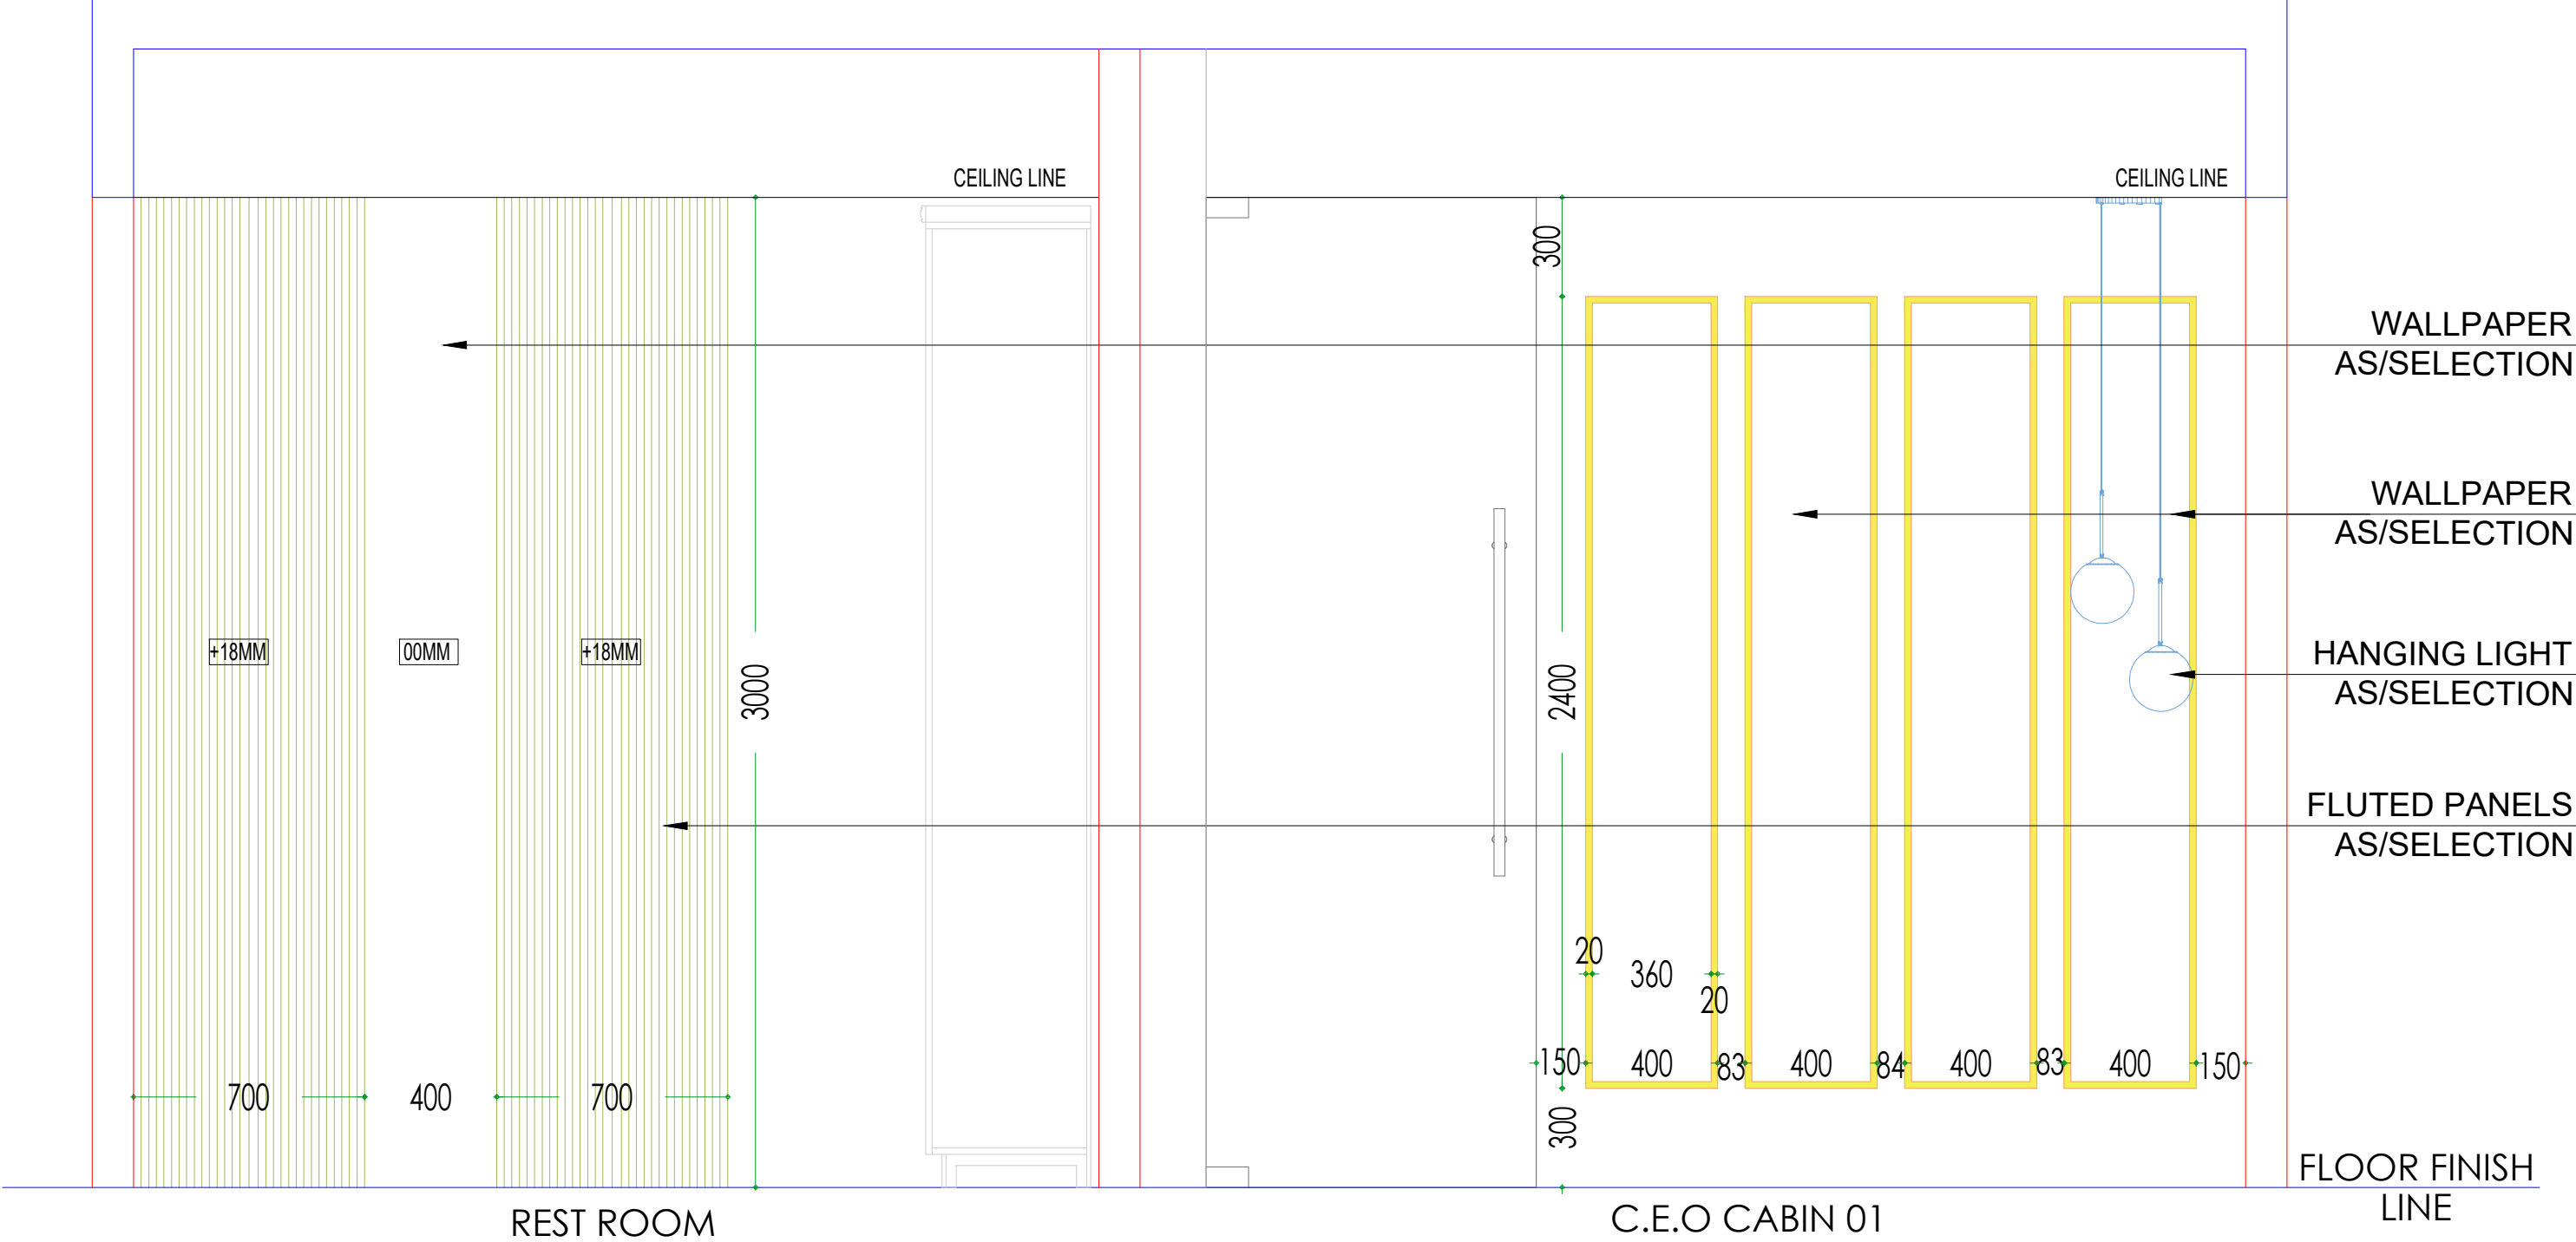

					Client Company & Name
					MR. RAVI TINGRE
					Job Title
					PROPOSED MIX USED BUILDING AT SR.NO. 37 & 39 KONDHWA KH
					Drawing Title
					WALL ELEVATION
					Scale
					N.T.S
					Drawn by
					TEJAL
					Checked by
					Date
					13/12/2025
					Job no.

					Drawing no
					Revision
					Status
REV	DETAILS	DRAWN	CHKD	DATE	


C.E.O. CABIN 02
ELEVATION A

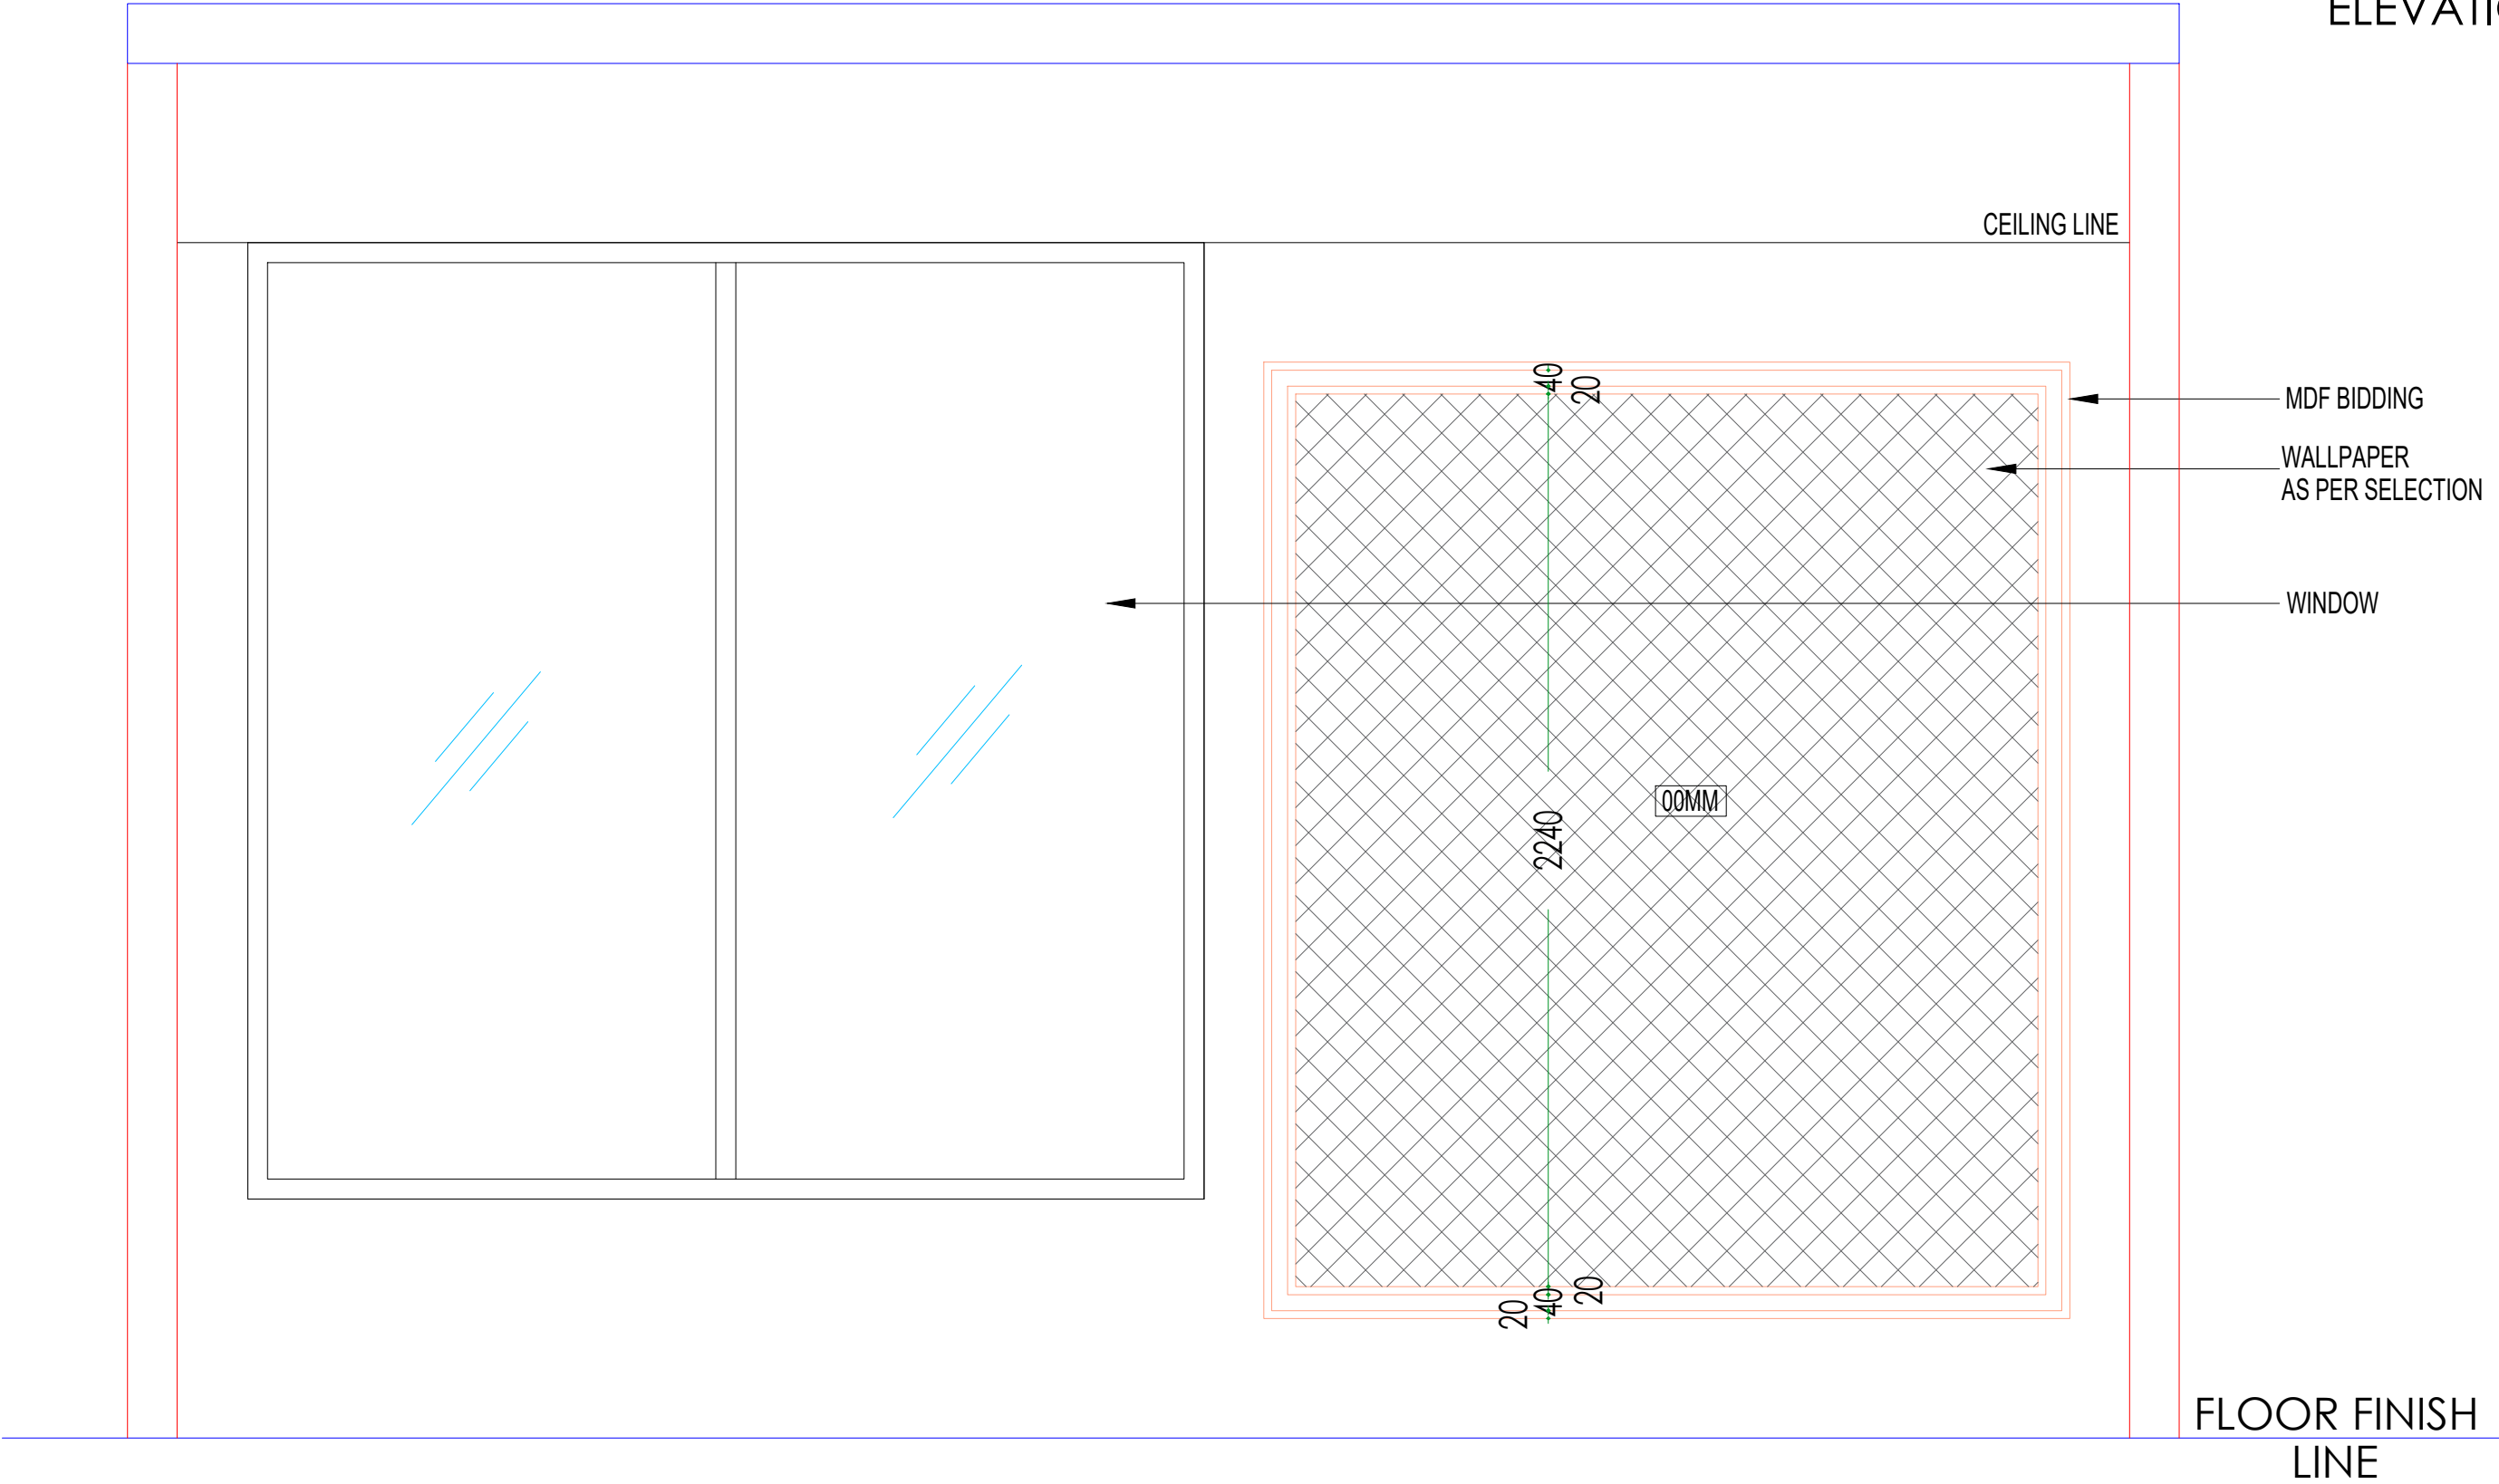

					Client Company & Name
					MR. RAVI TINGRE
					Job Title
					PROPOSED MIX USED BUILDING AT SR.NO. 37 & 39 KONDHWA KH
					Drawing Title
					WALL ELEVATION
					Scale
					N.T.S
					Drawn by
					TEJAL
					Checked by
					Date
					13/12/2025
					Job no.

					Drawing no
					Revision
					Status
REV	DETAILS	DRAWN	CHKD	DATE	


C.E.O. CABIN 02
ELEVATION B

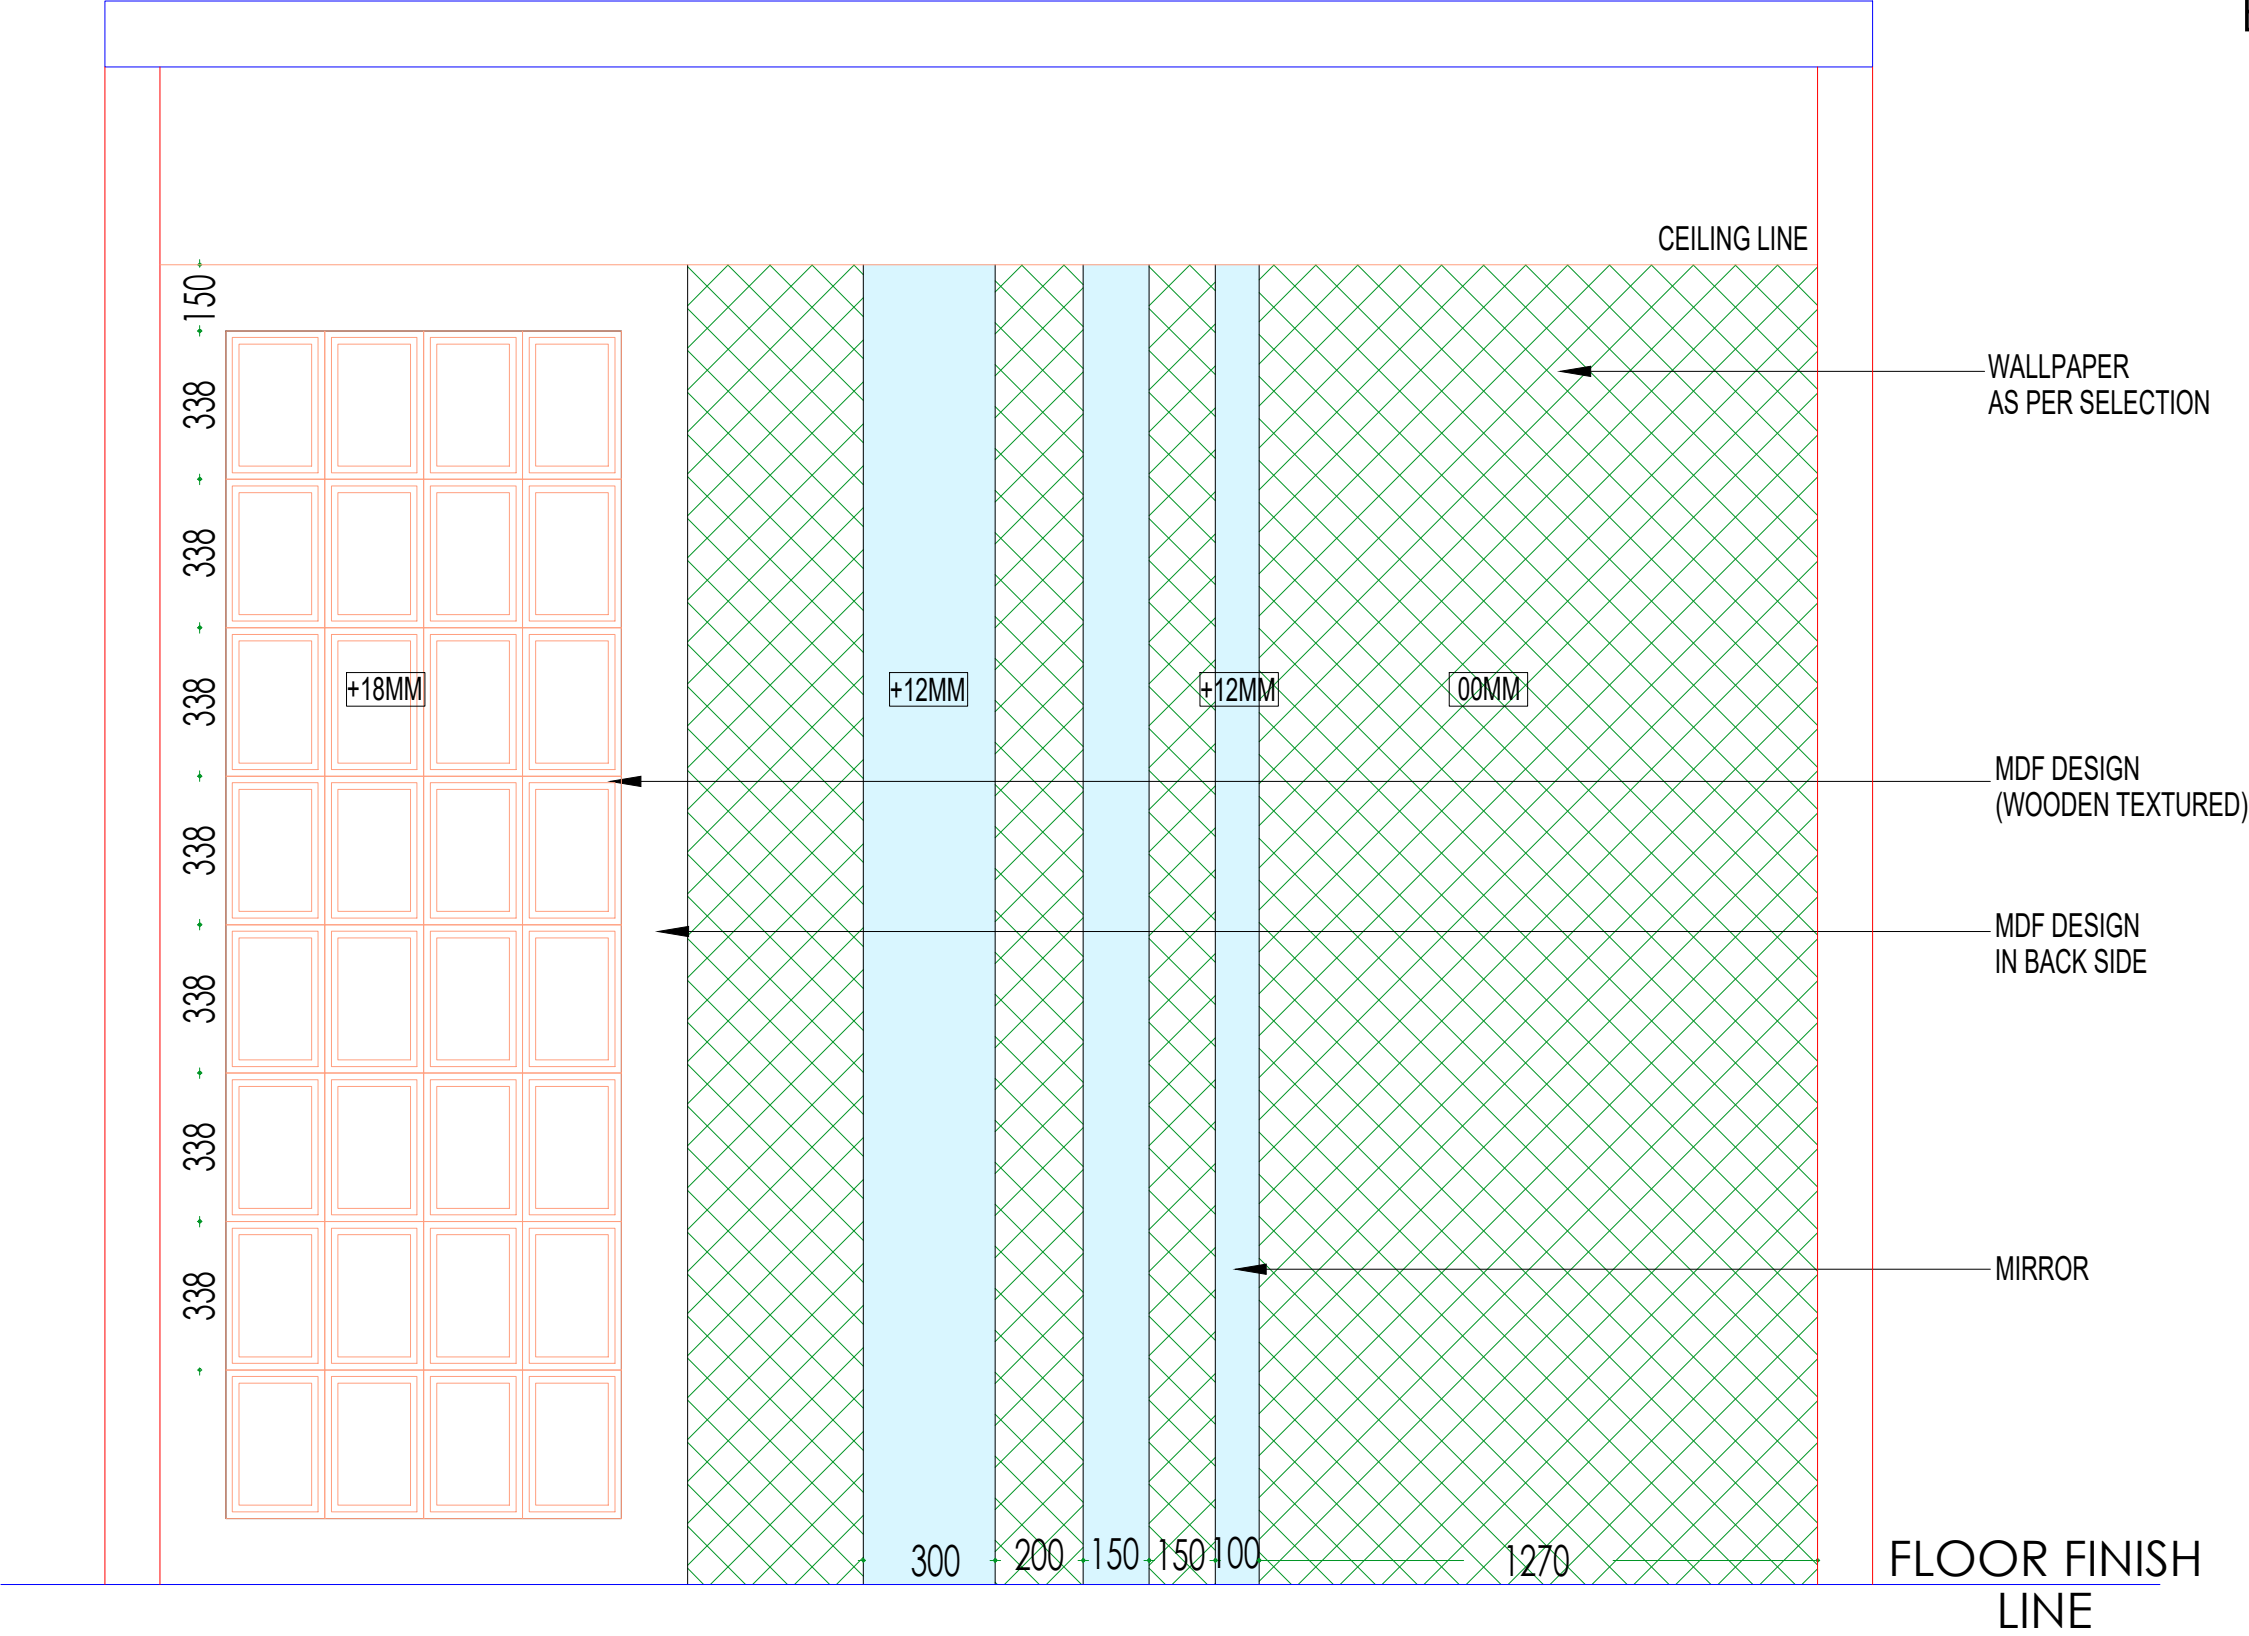

					Client Company & Name
					MR. RAVI TINGRE
					Job Title
					PROPOSED MIX USED BUILDING AT SR.NO. 37 & 39 KONDHWA KH
					Drawing Title
					WALL ELEVATION
					Scale
					N.T.S
					Drawn by
					TEJAL
					Checked by
					Date
					13/12/2025
					Job no.
					Drawing no
					Revision

					Status
REV	DETAILS	DRAWN	CHKD	DATE	


C.E.O. CABIN 02
ELEVATION C

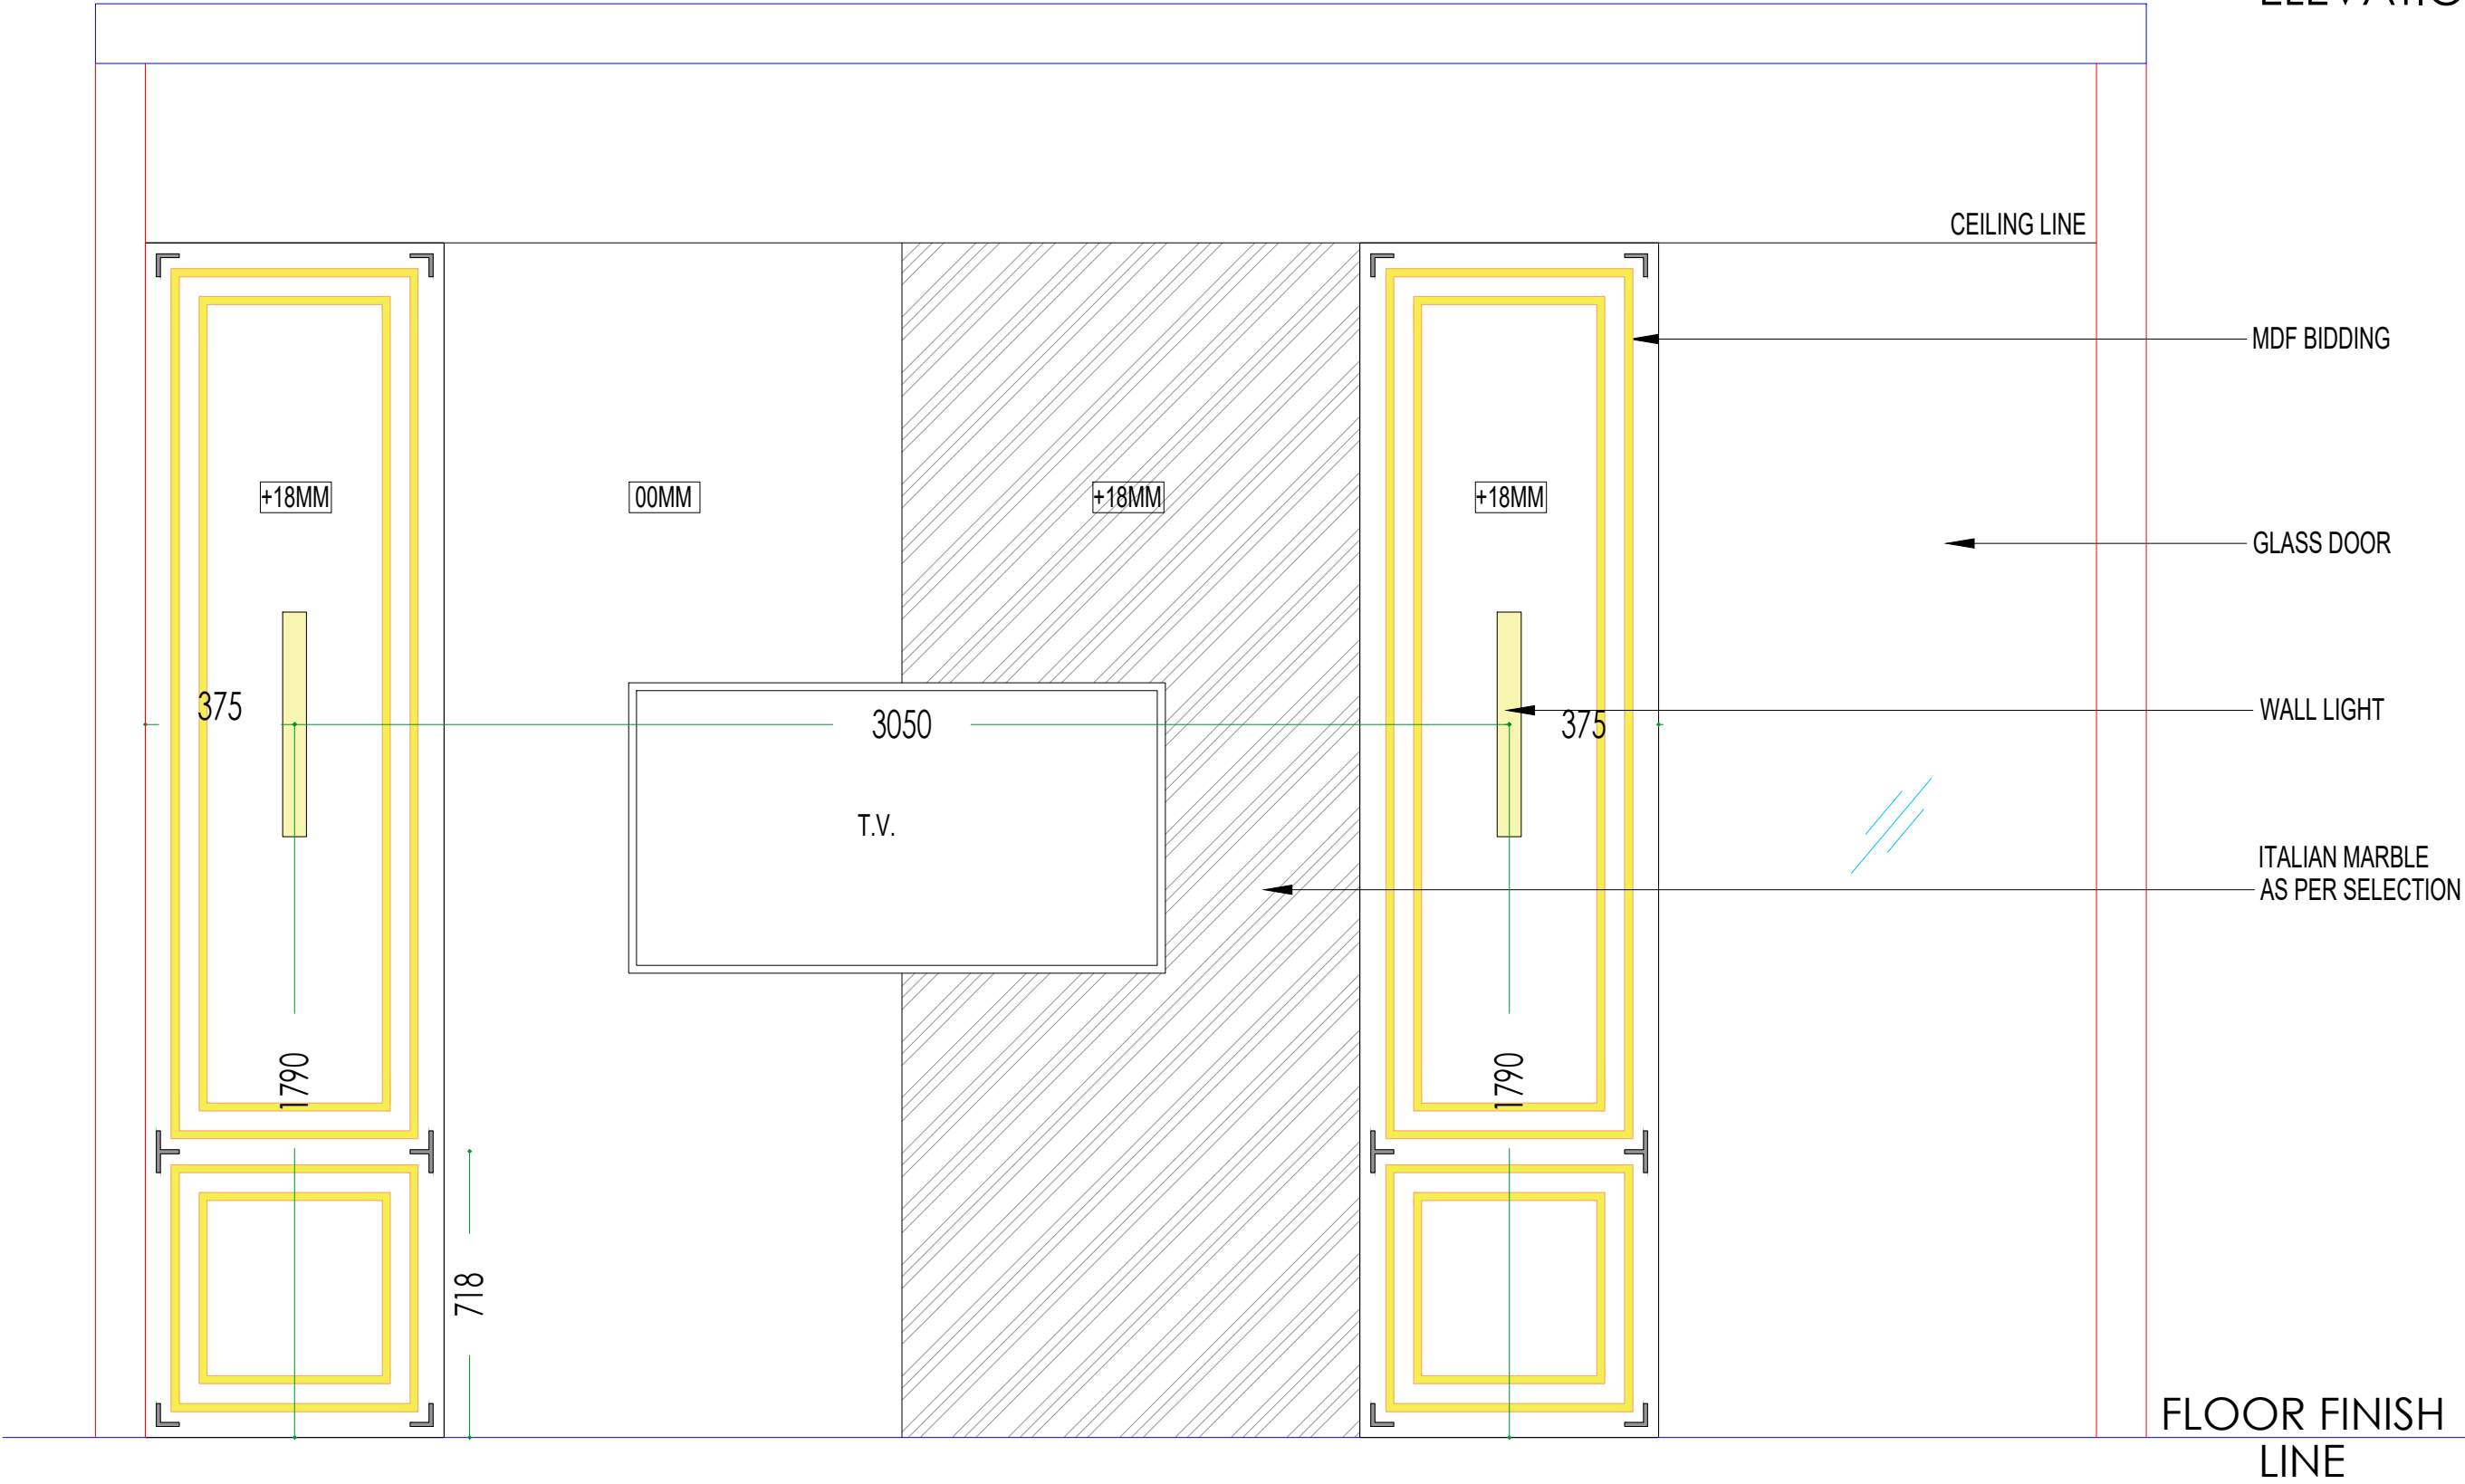

					Client Company & Name
					MR. RAVI TINGRE
					Job Title
					PROPOSED MIX USED BUILDING AT SR.NO. 37 & 39 KONDHWA KH
					Drawing Title
					WALL ELEVATION
					Scale
					N.T.S
					Drawn by
					TEJAL
					Checked by
					Date
					13/12/2025
					Job no.

					Drawing no
					Revision
					Status
REV	DETAILS	DRAWN	CHKD	DATE	


C.E.O. CABIN 02
ELEVATION D

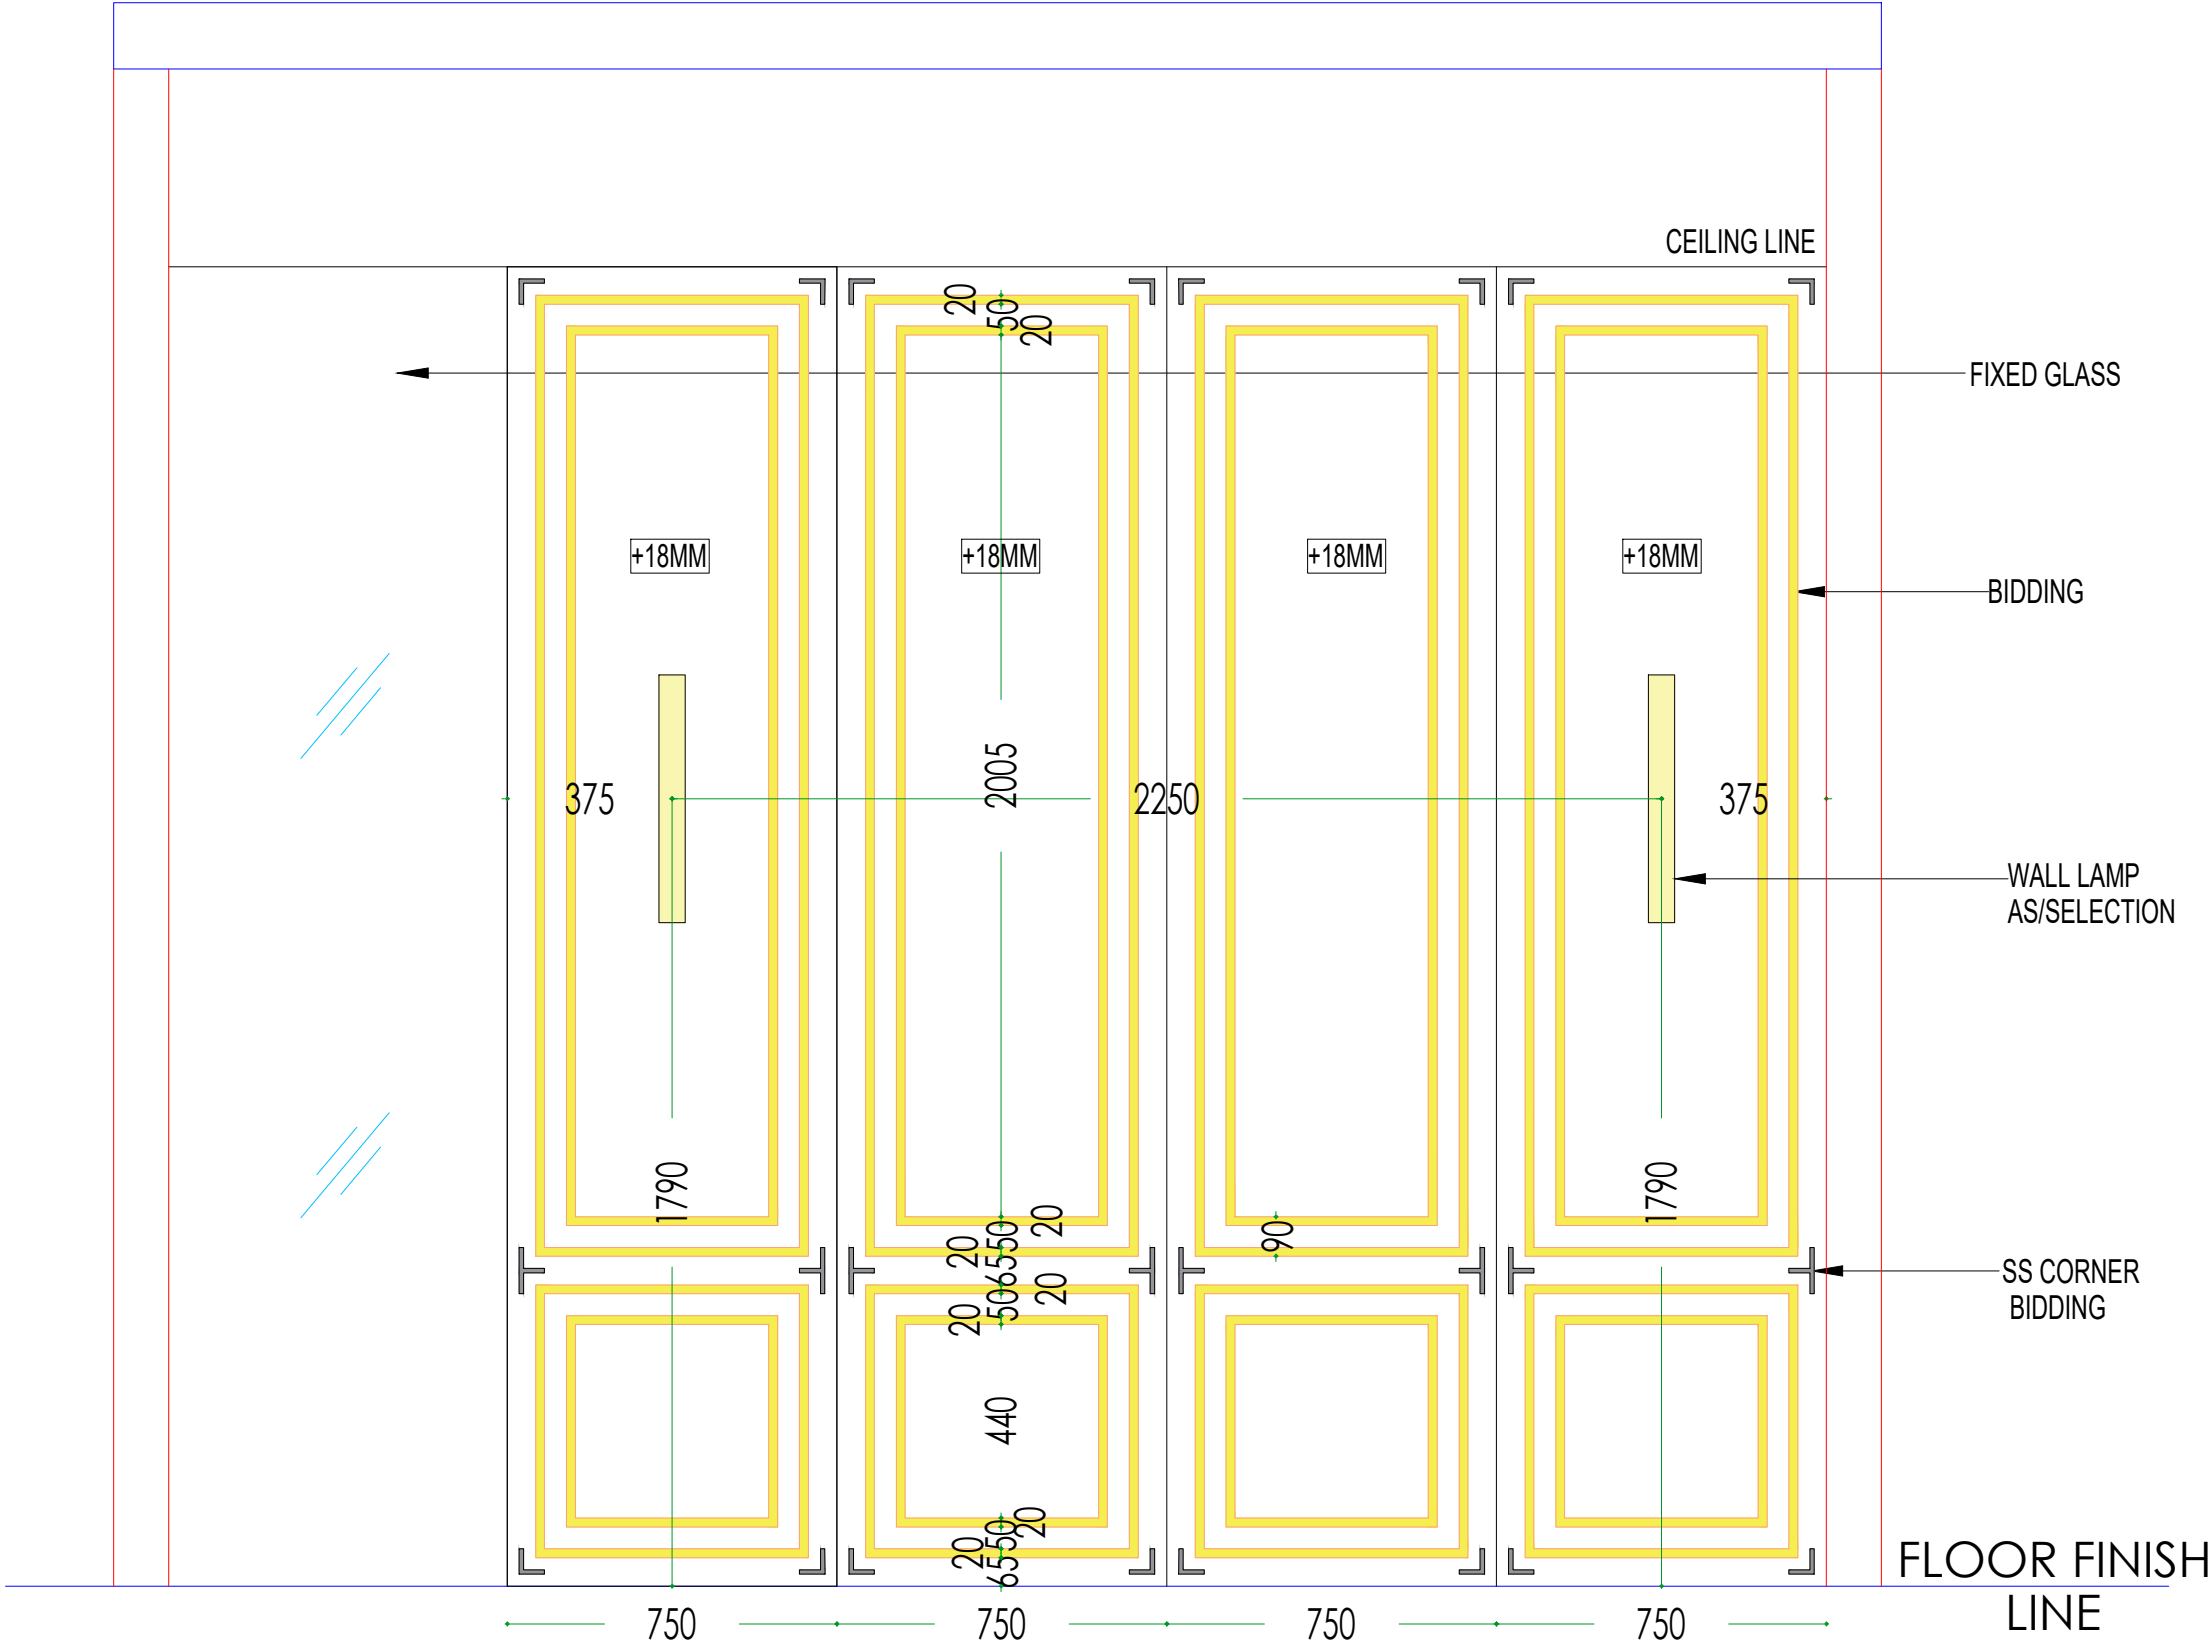

					Client Company & Name
					MR. RAVI TINGRE
					Job Title
					PROPOSED MIX USED BUILDING AT SR.NO. 37 & 39 KONDHWA KH
					Drawing Title
					WALL ELEVATION
					Scale
					N.T.S
					Drawn by
					TEJAL
					Checked by
					Date
					13/12/2025
					Job no.

					Drawing no
					Revision
					Status
REV	DETAILS	DRAWN	CHKD	DATE	


MODEL DISPLAY AREA
ELEVATION AT A

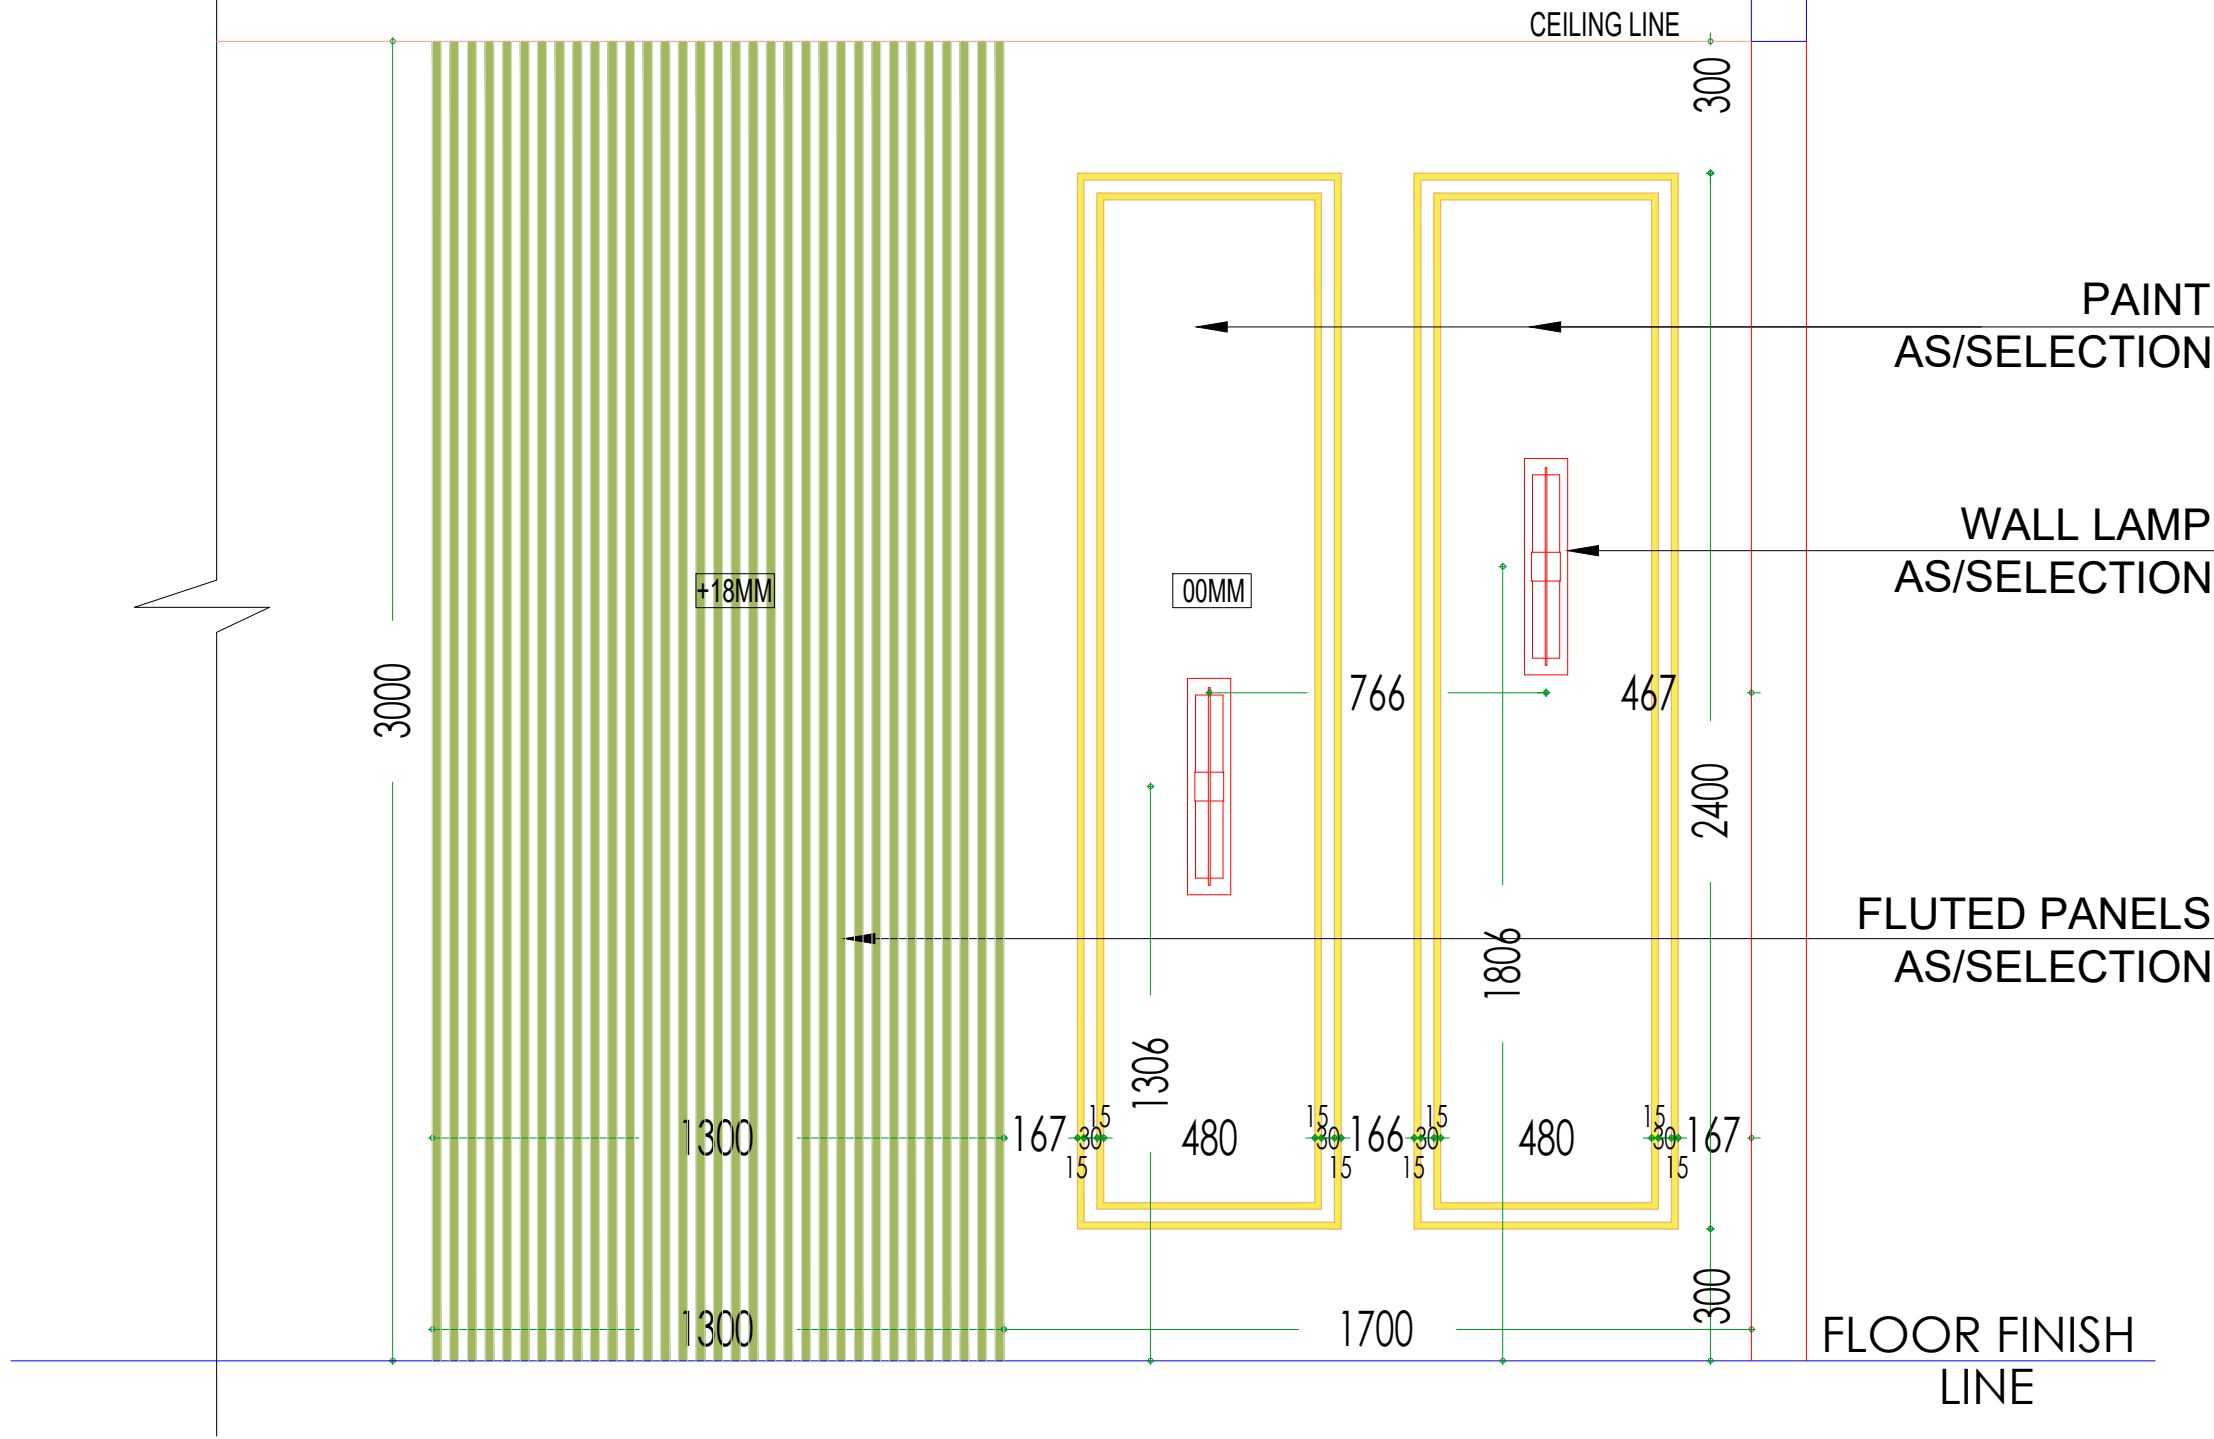

					Client Company & Name
					MR. RAVI TINGRE
					Job Title
					PROPOSED MIX USED BUILDING AT SR.NO. 37 & 39 KONDHWA KH
					Drawing Title
					WALL ELEVATION
					Scale
					N.T.S
					Drawn by
					TEJAL
					Checked by
					Date
					13/12/2025
					Job no.

					Drawing no
					Revision
					Status
REV	DETAILS	DRAWN	CHKD	DATE	


MODEL DISPLAY AREA
ELEVATION AT B

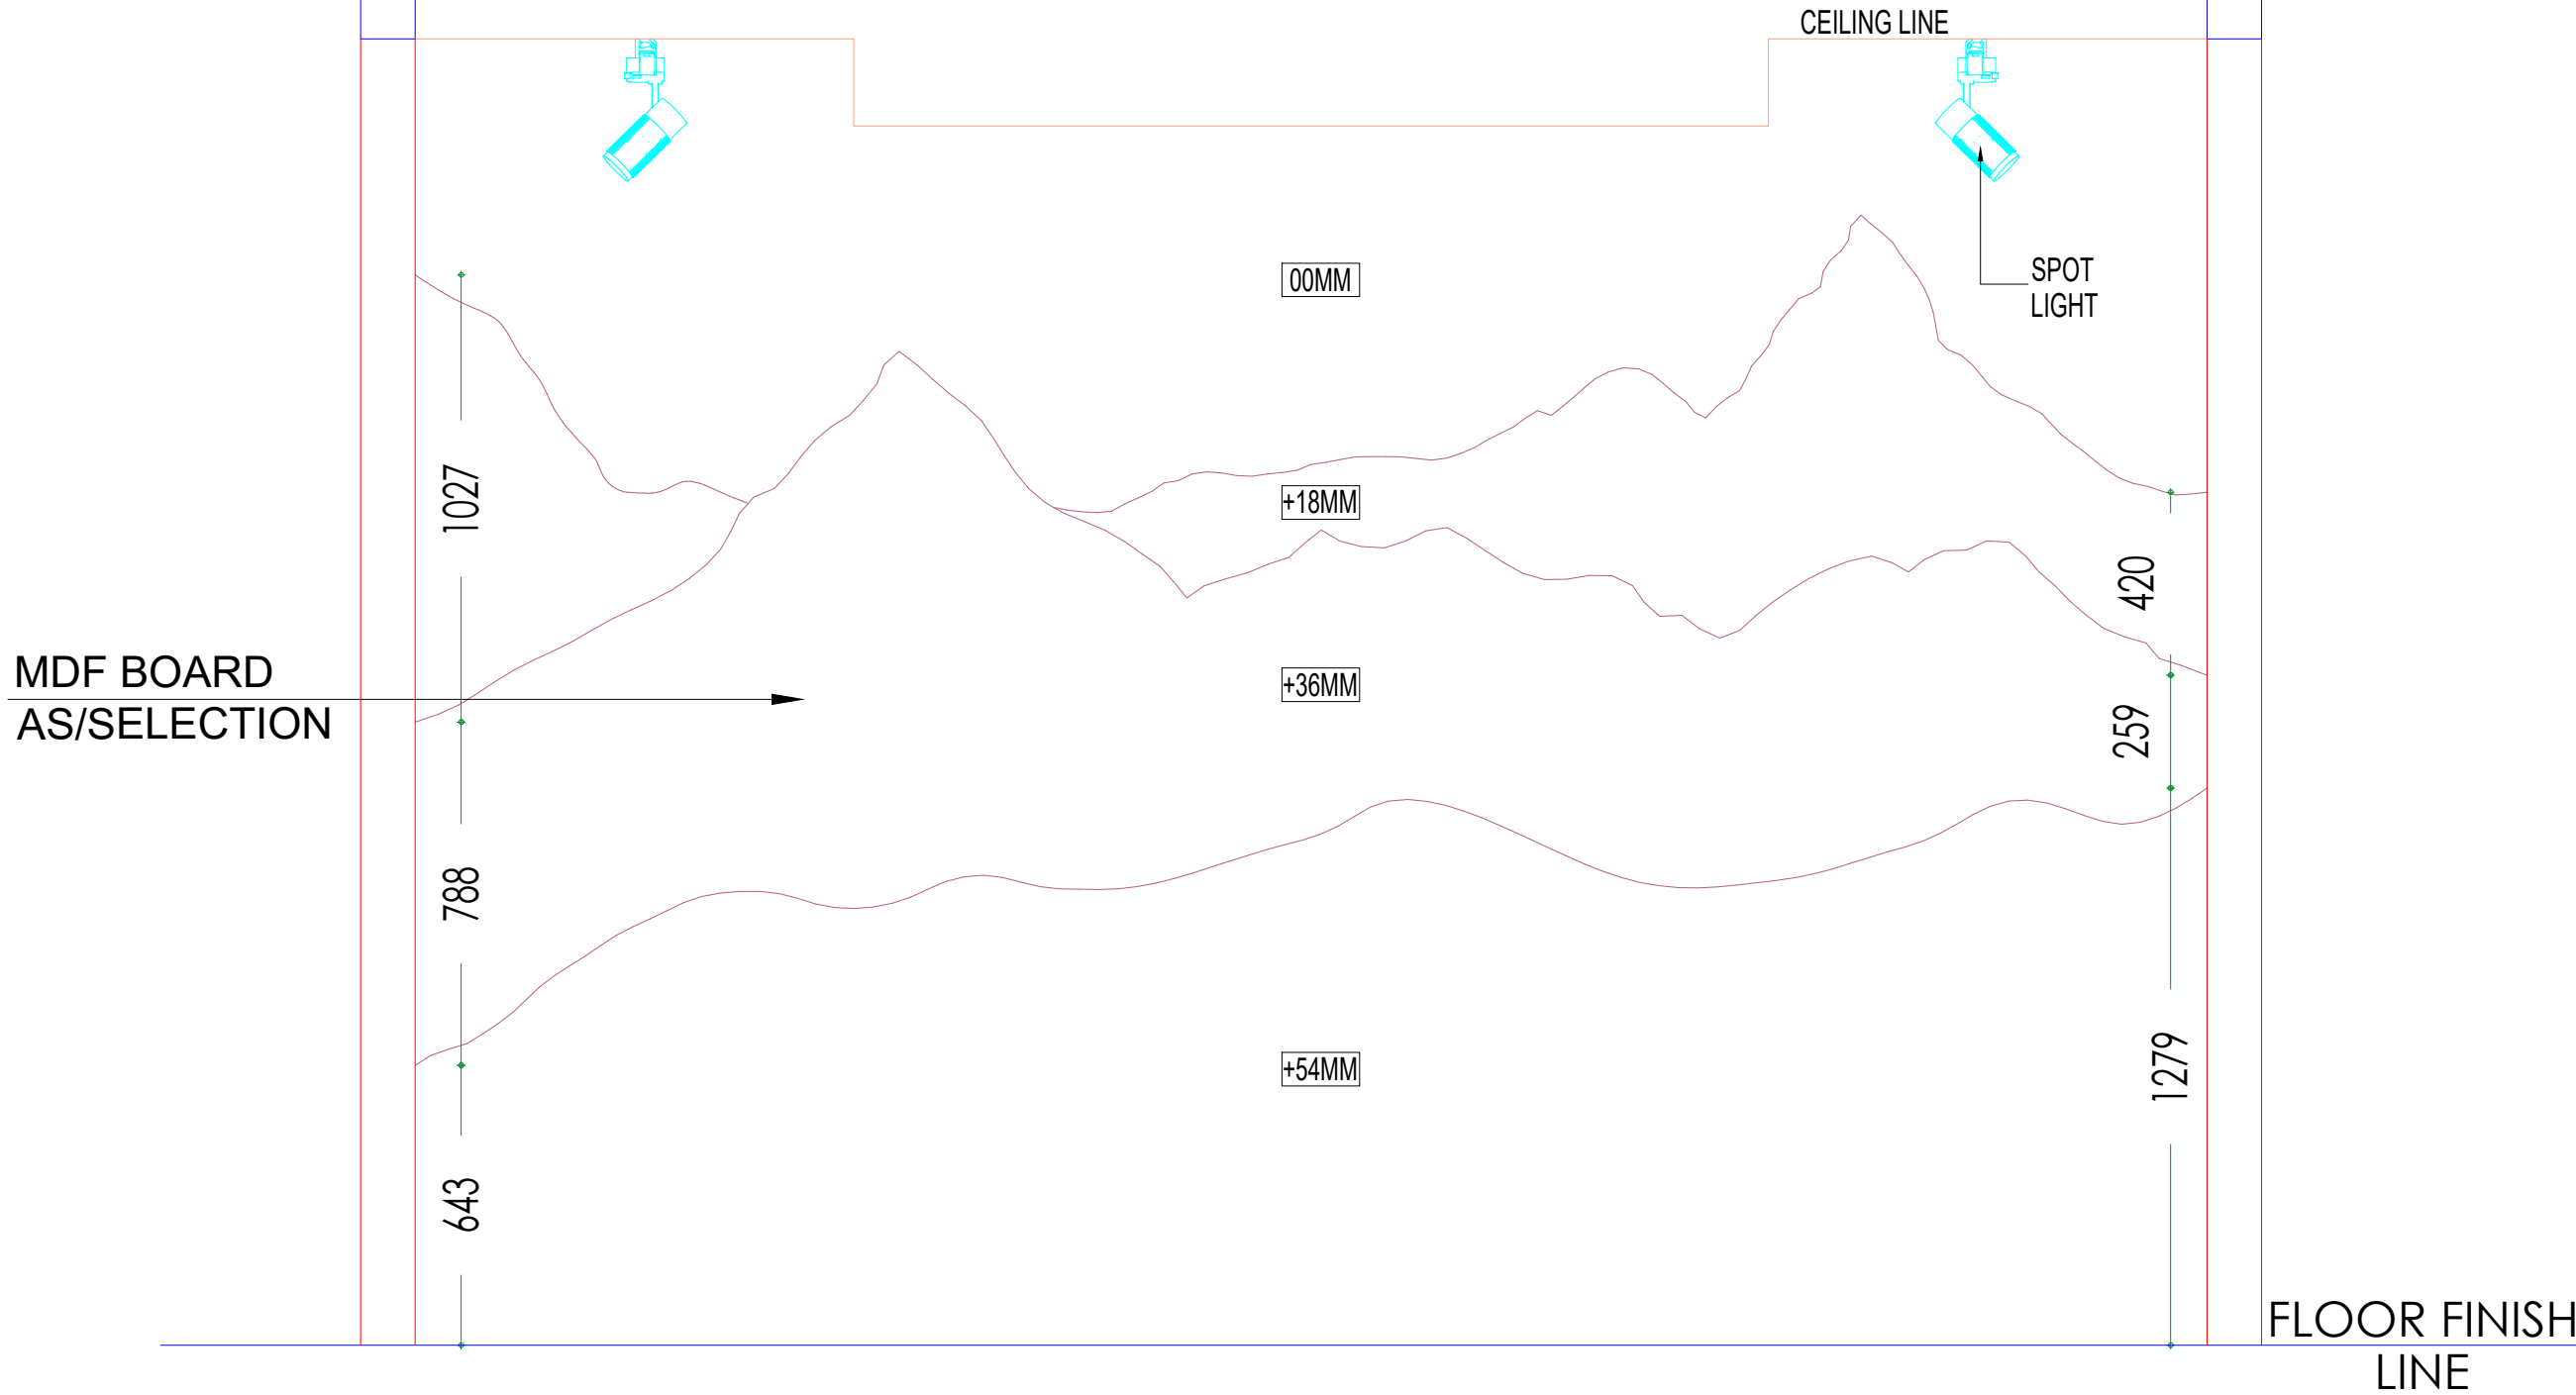

					Client Company & Name
					MR. RAVI TINGRE
					Job Title
					PROPOSED MIX USED BUILDING AT SR.NO. 37 & 39 KONDHWA KH
					Drawing Title
					WALL ELEVATION
					Scale
					N.T.S
					Drawn by
					TEJAL
					Checked by
					Date
					13/12/2025
					Job no.

					Drawing no
					Revision
					Status
REV	DETAILS	DRAWN	CHKD	DATE	


MODEL DISPLAY AREA
ELEVATION AT C

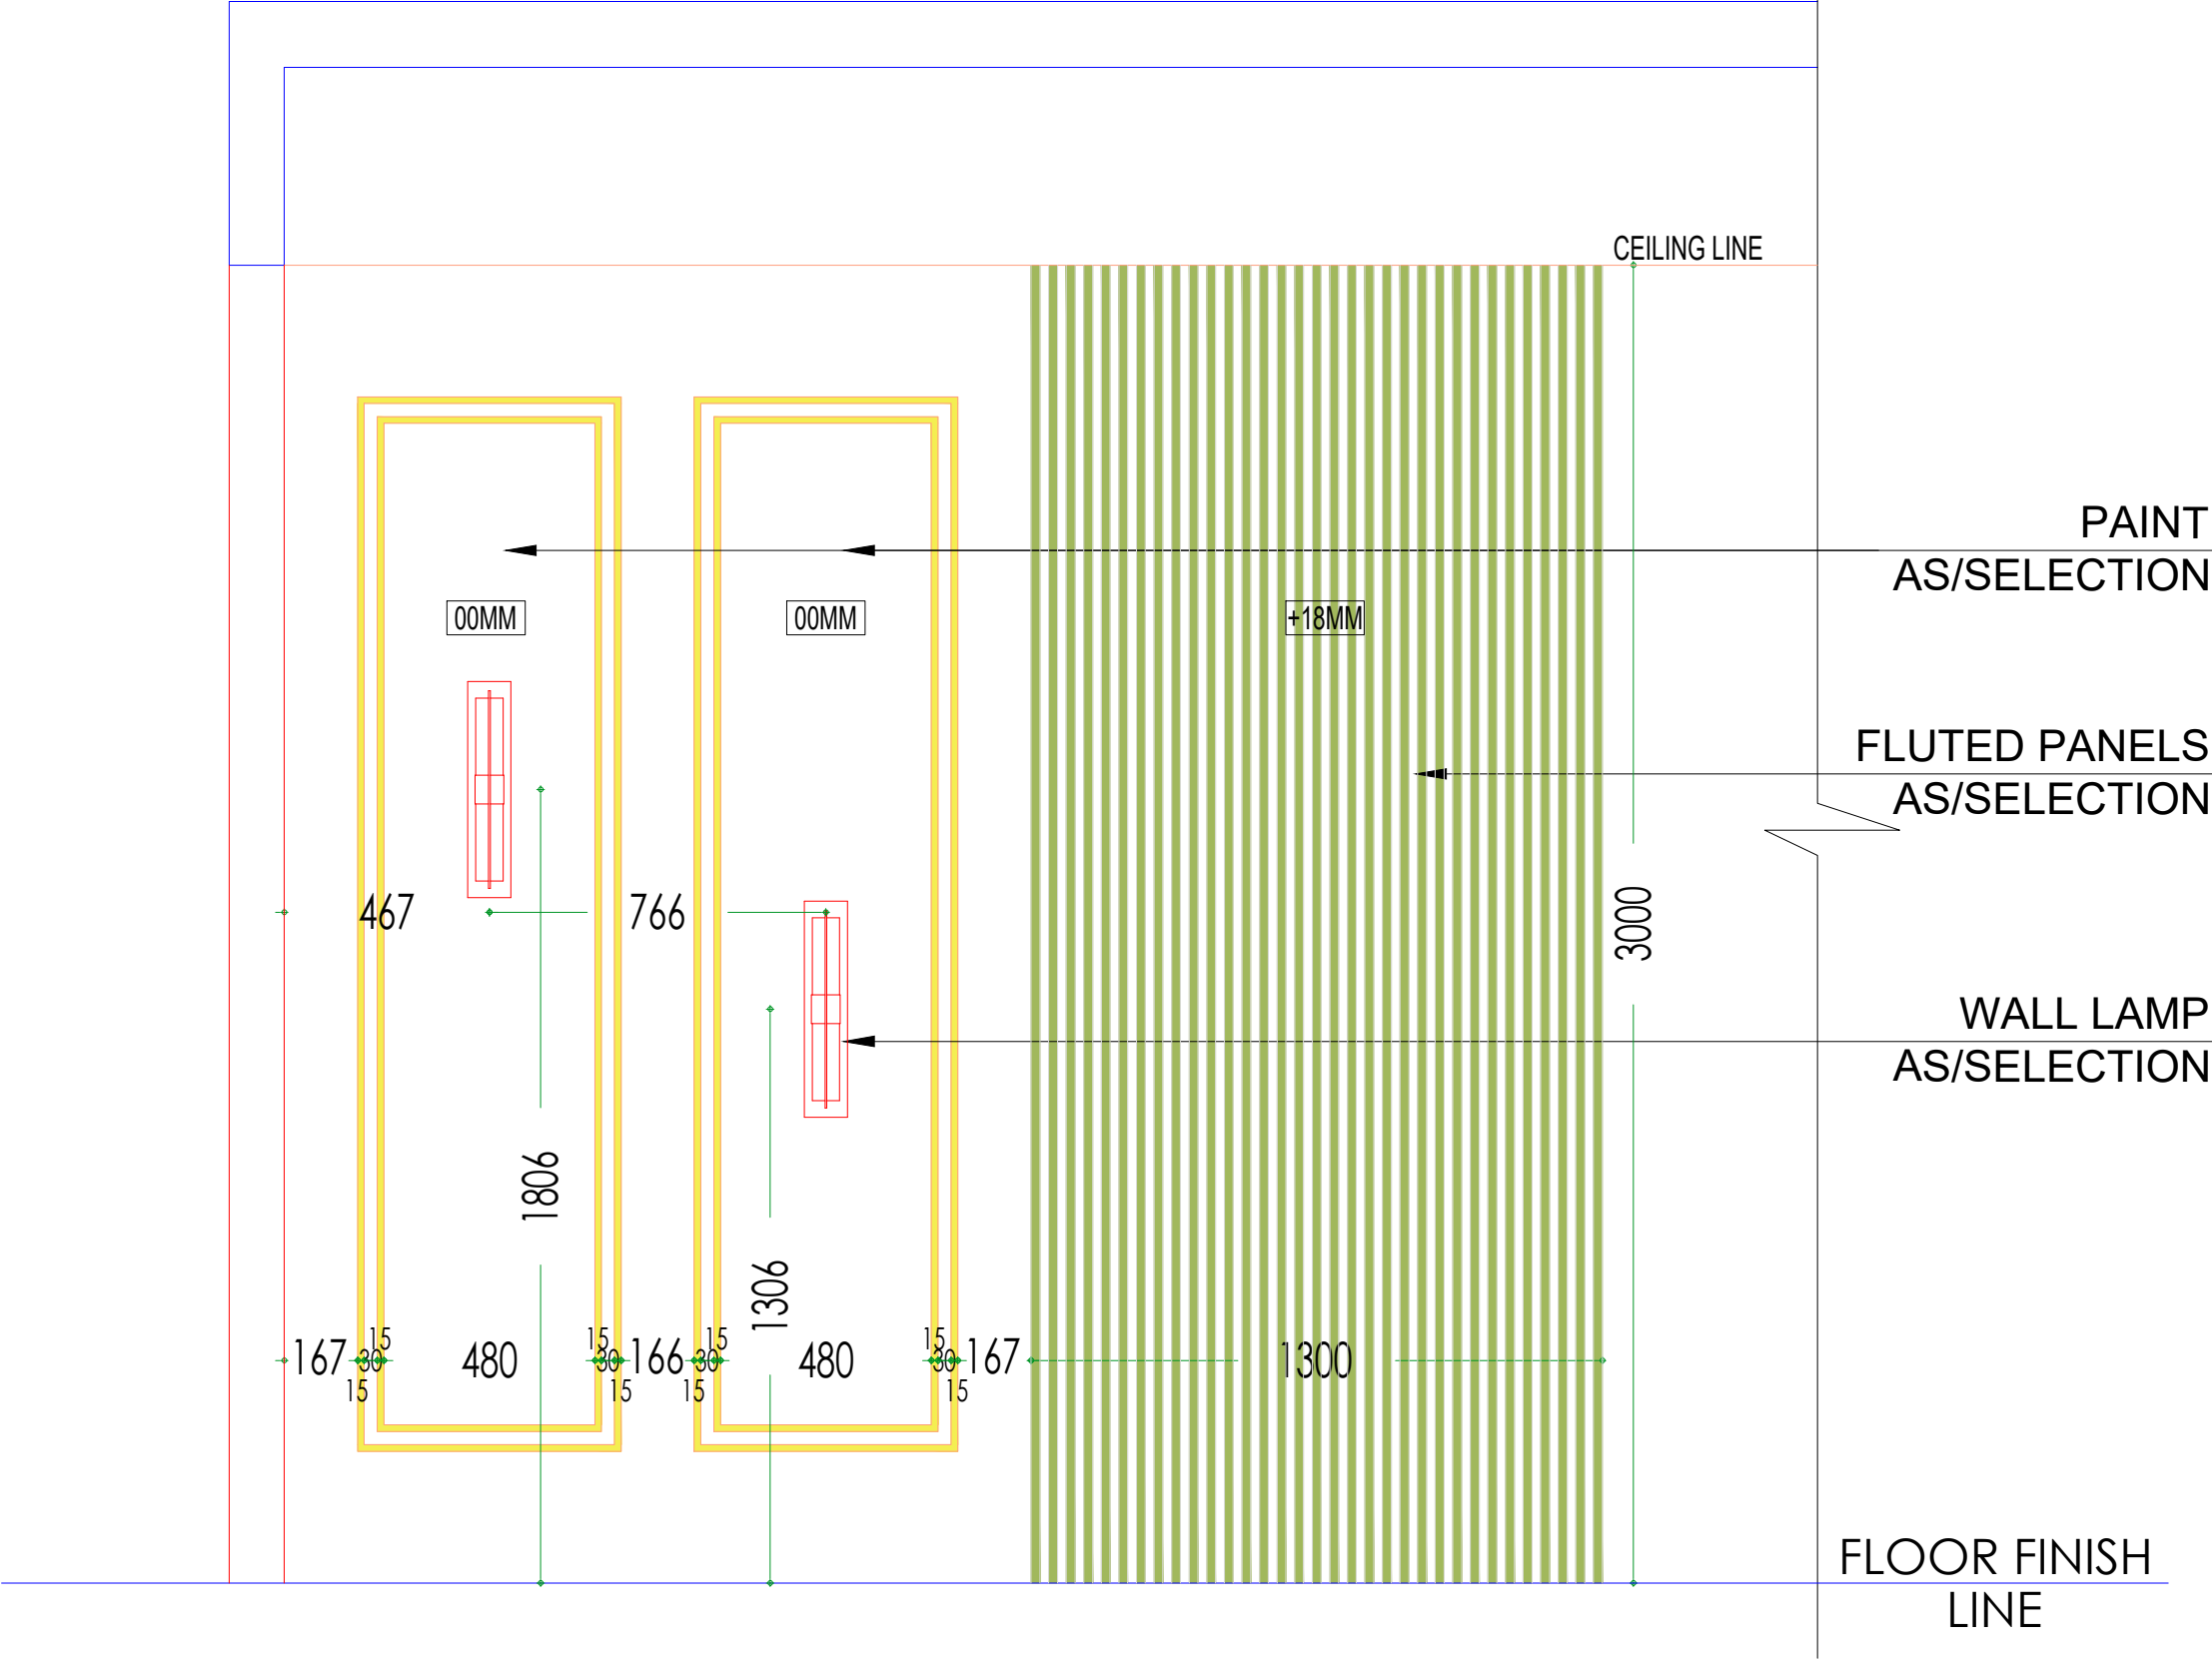

					Client Company & Name
					MR. RAVI TINGRE
					Job Title
					PROPOSED MIX USED BUILDING AT SR.NO. 37 & 39 KONDHWA KH
					Drawing Title
					WALL ELEVATION
					Scale
					N.T.S
					Drawn by
					TEJAL
					Checked by
					Date
					13/12/2025
					Job no.

					Drawing no
					Revision
					Status
REV	DETAILS	DRAWN	CHKD	DATE	

SALES CABIN 01 & 02
ELEVATION A

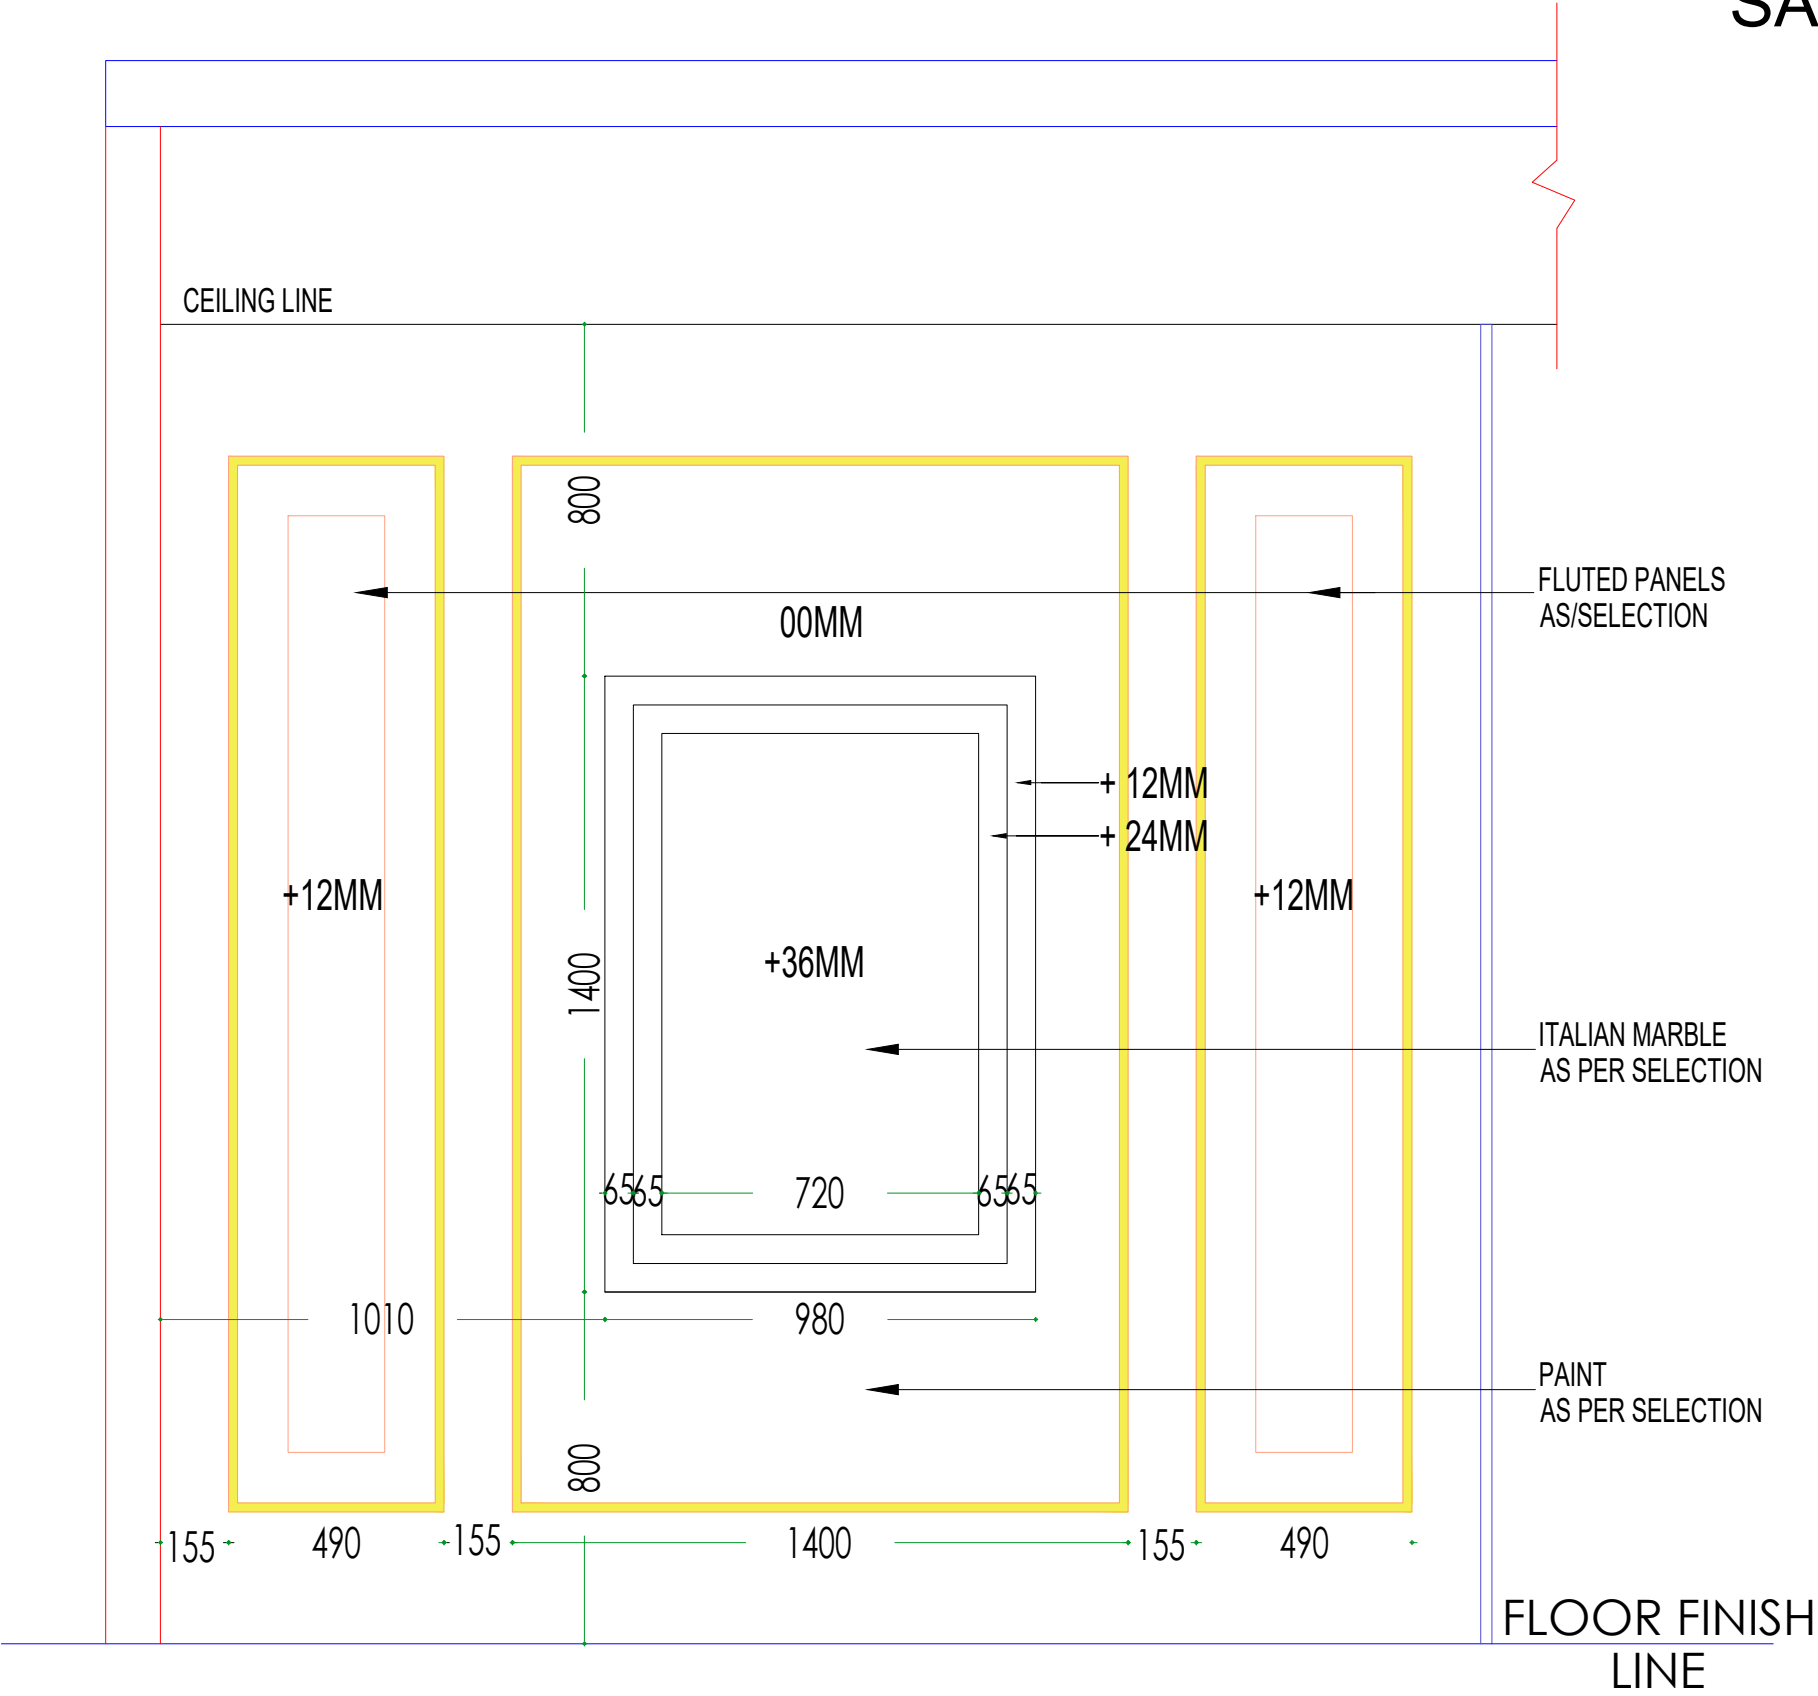


					Client Company & Name
					MR. RAVI TINGRE
					Job Title
					PROPOSED MIX USED BUILDING AT SR.NO. 37 & 39 KONDHWA KH
					Drawing Title
					WALL ELEVATION
					Scale
					N.T.S
					Drawn by
					TEJAL
					Checked by
					Date
					13/12/2025
					Job no.

					Drawing no
					Revision
					Status
REV	DETAILS	DRAWN	CHKD	DATE	

SALES CABIN 03


ELEVATION A

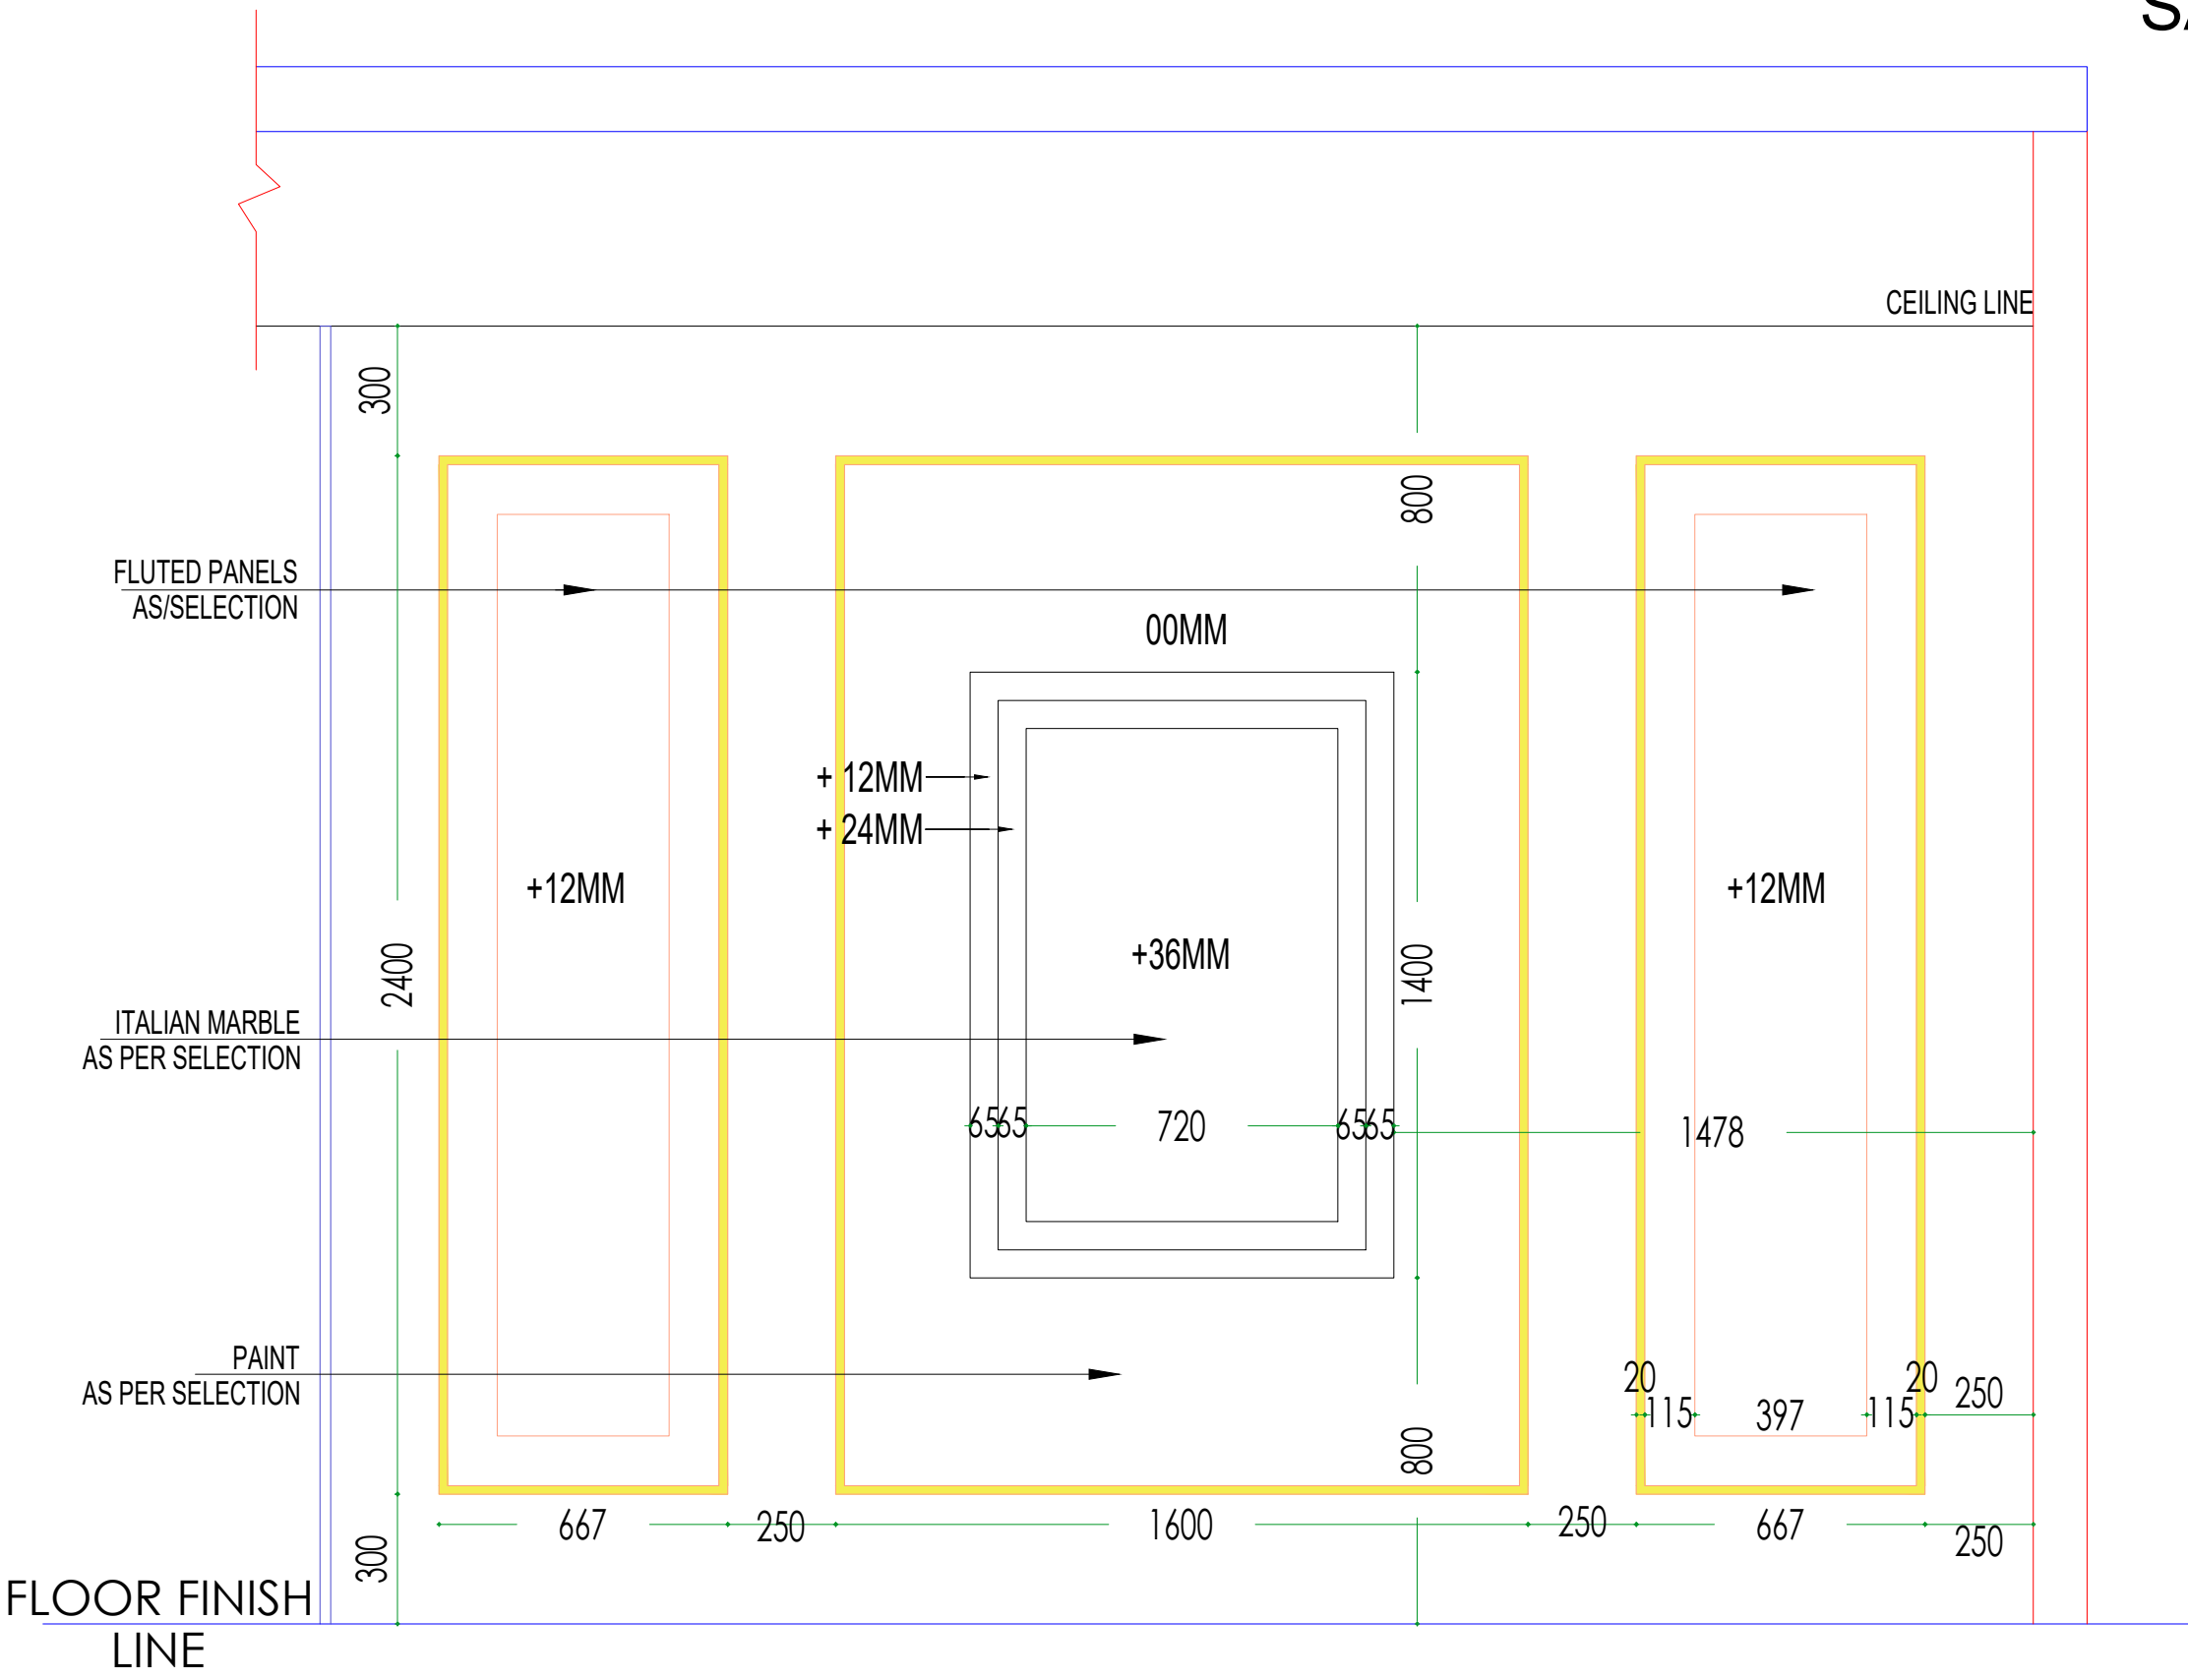

					Client Company & Name
					MR. RAVI TINGRE
					Job Title
					PROPOSED MIX USED BUILDING AT SR.NO. 37 & 39 KONDHWA KH
					Drawing Title
					WALL ELEVATION
					Scale
					N.T.S
					Drawn by
					TEJAL
					Checked by
					Date
					13/12/2025
					Job no.


					Drawing no
					Revision
					Status
REV	DETAILS	DRAWN	CHKD	DATE	

LIVING ROOM & ENTRANCE LOBBY
ELEVATION A

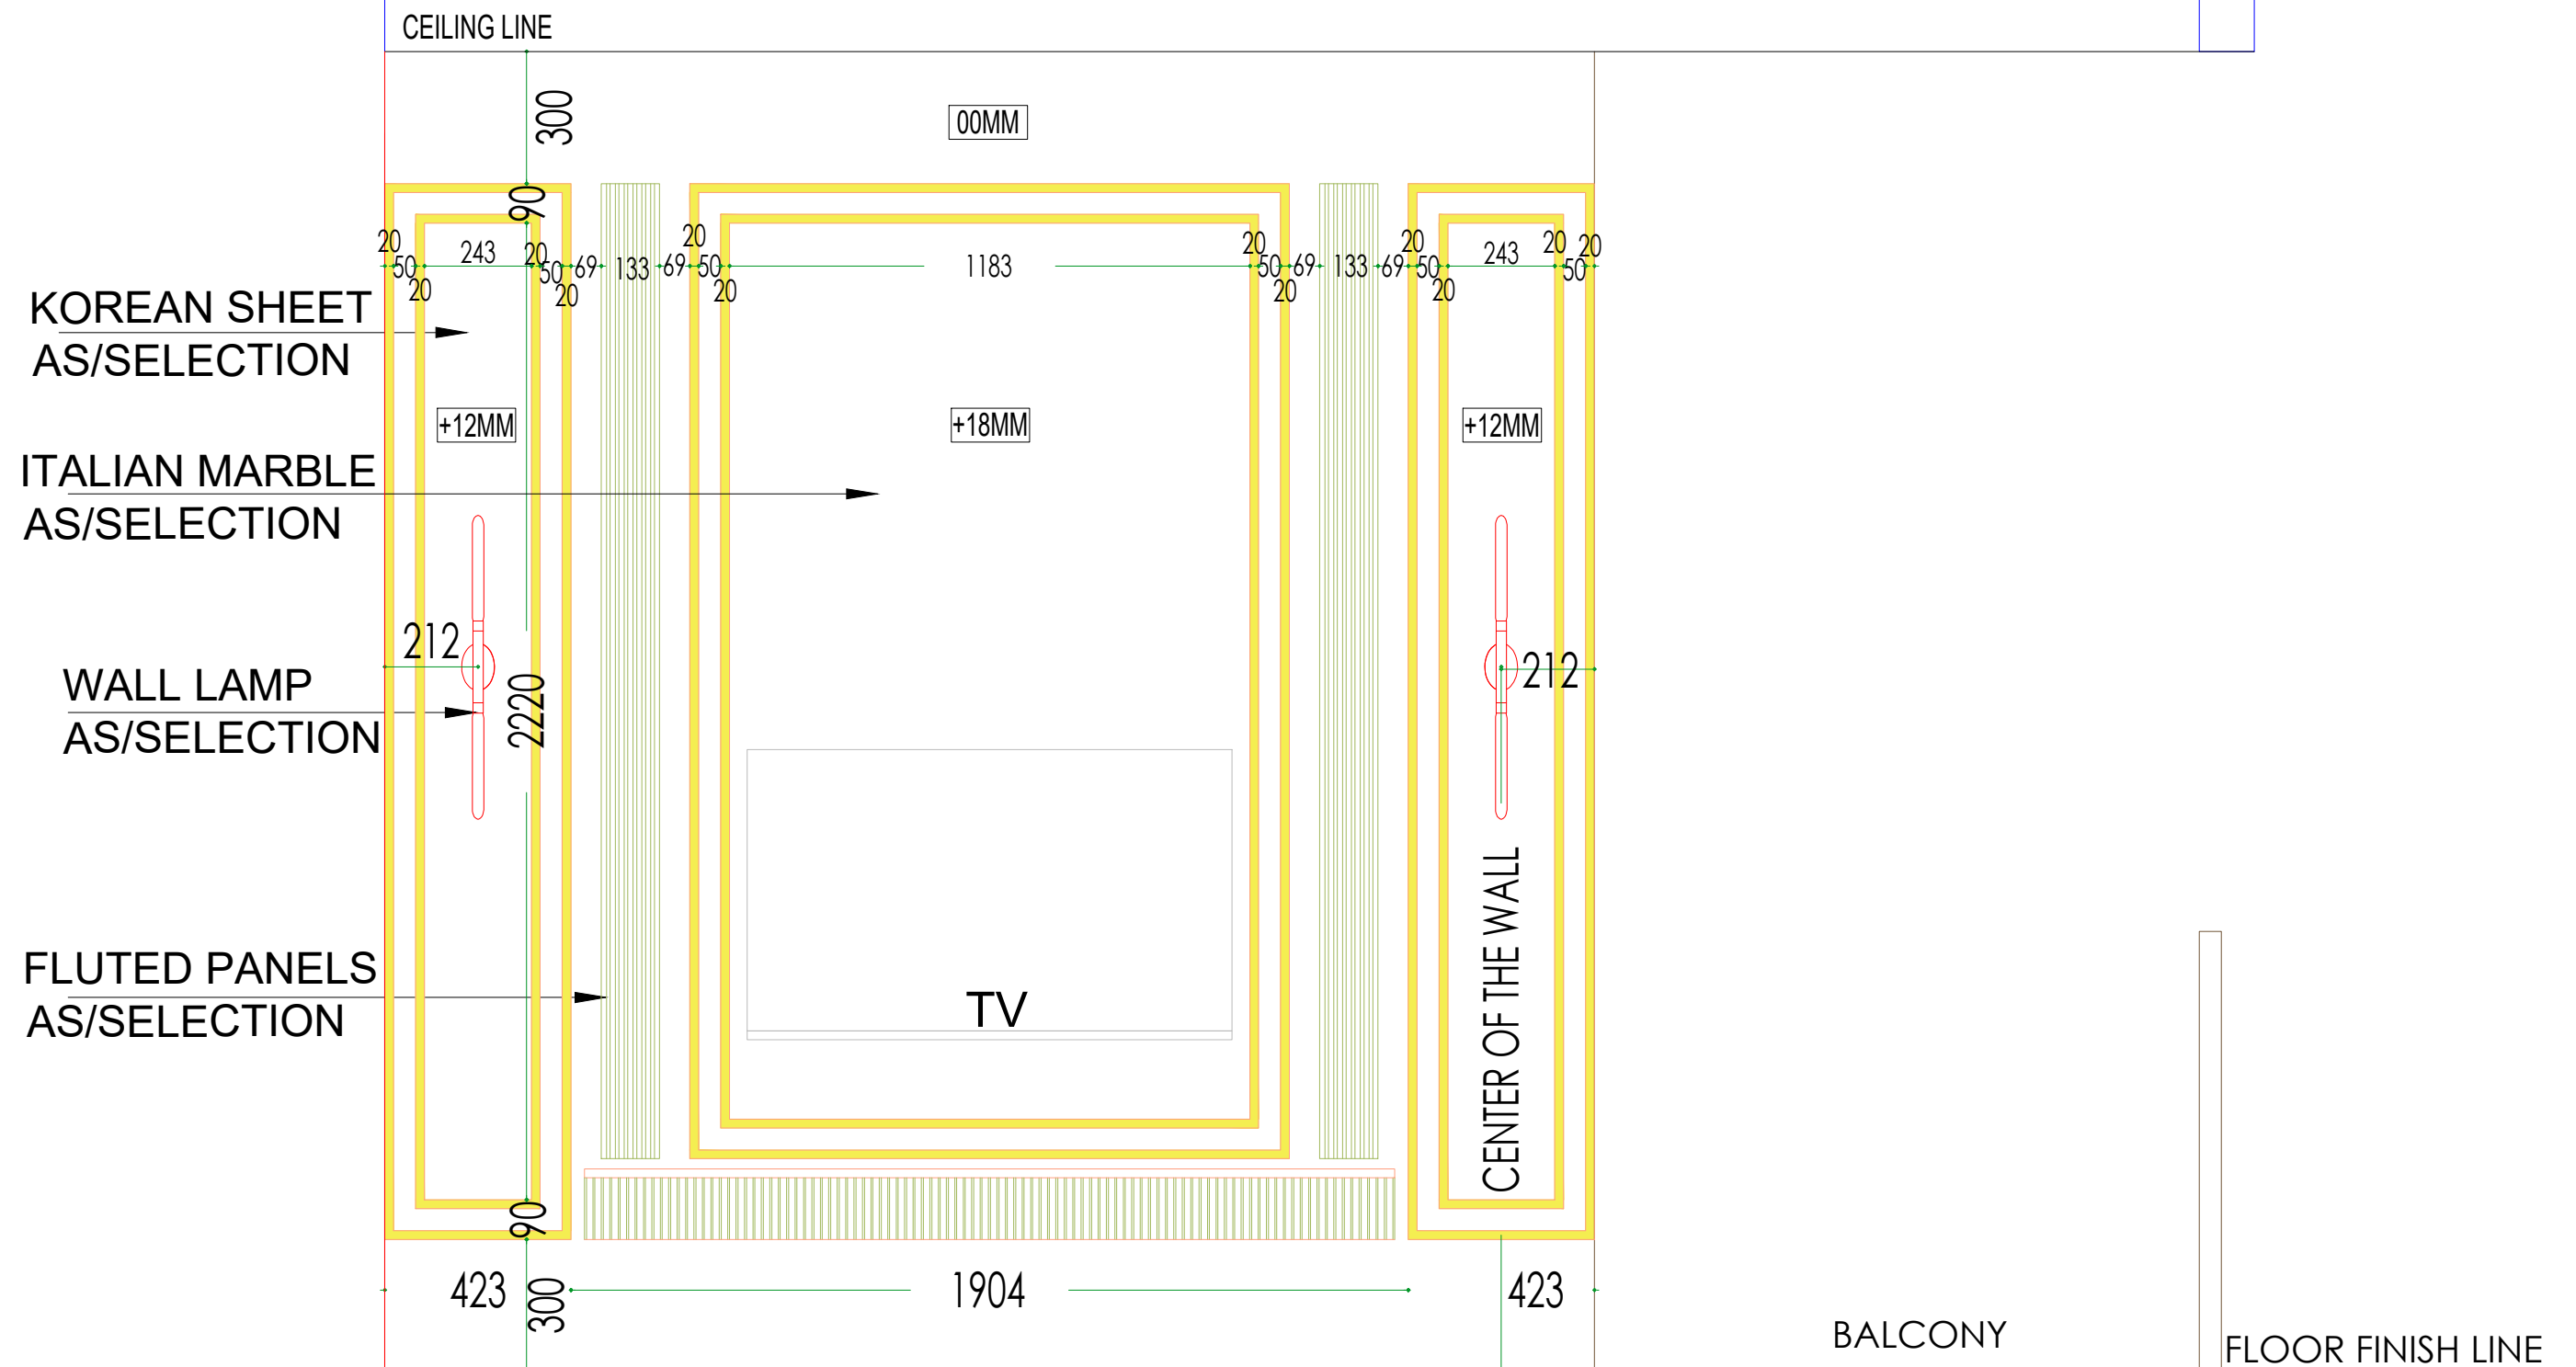

					Client Company & Name
					MR. RAVI TINGRE
					Job Title
					PROPOSED MIX USED BUILDING AT SR.NO. 37 & 39 KONDHWA KH
					Drawing Title
					WALL ELEVATION
					Scale
					N.T.S
					Drawn by
					TEJAL
					Checked by
					Date
					13/12/2025
					Job no.
					Drawing no
					Revision


REV	DETAILS	DRAWN	CHKD	DATE	Status

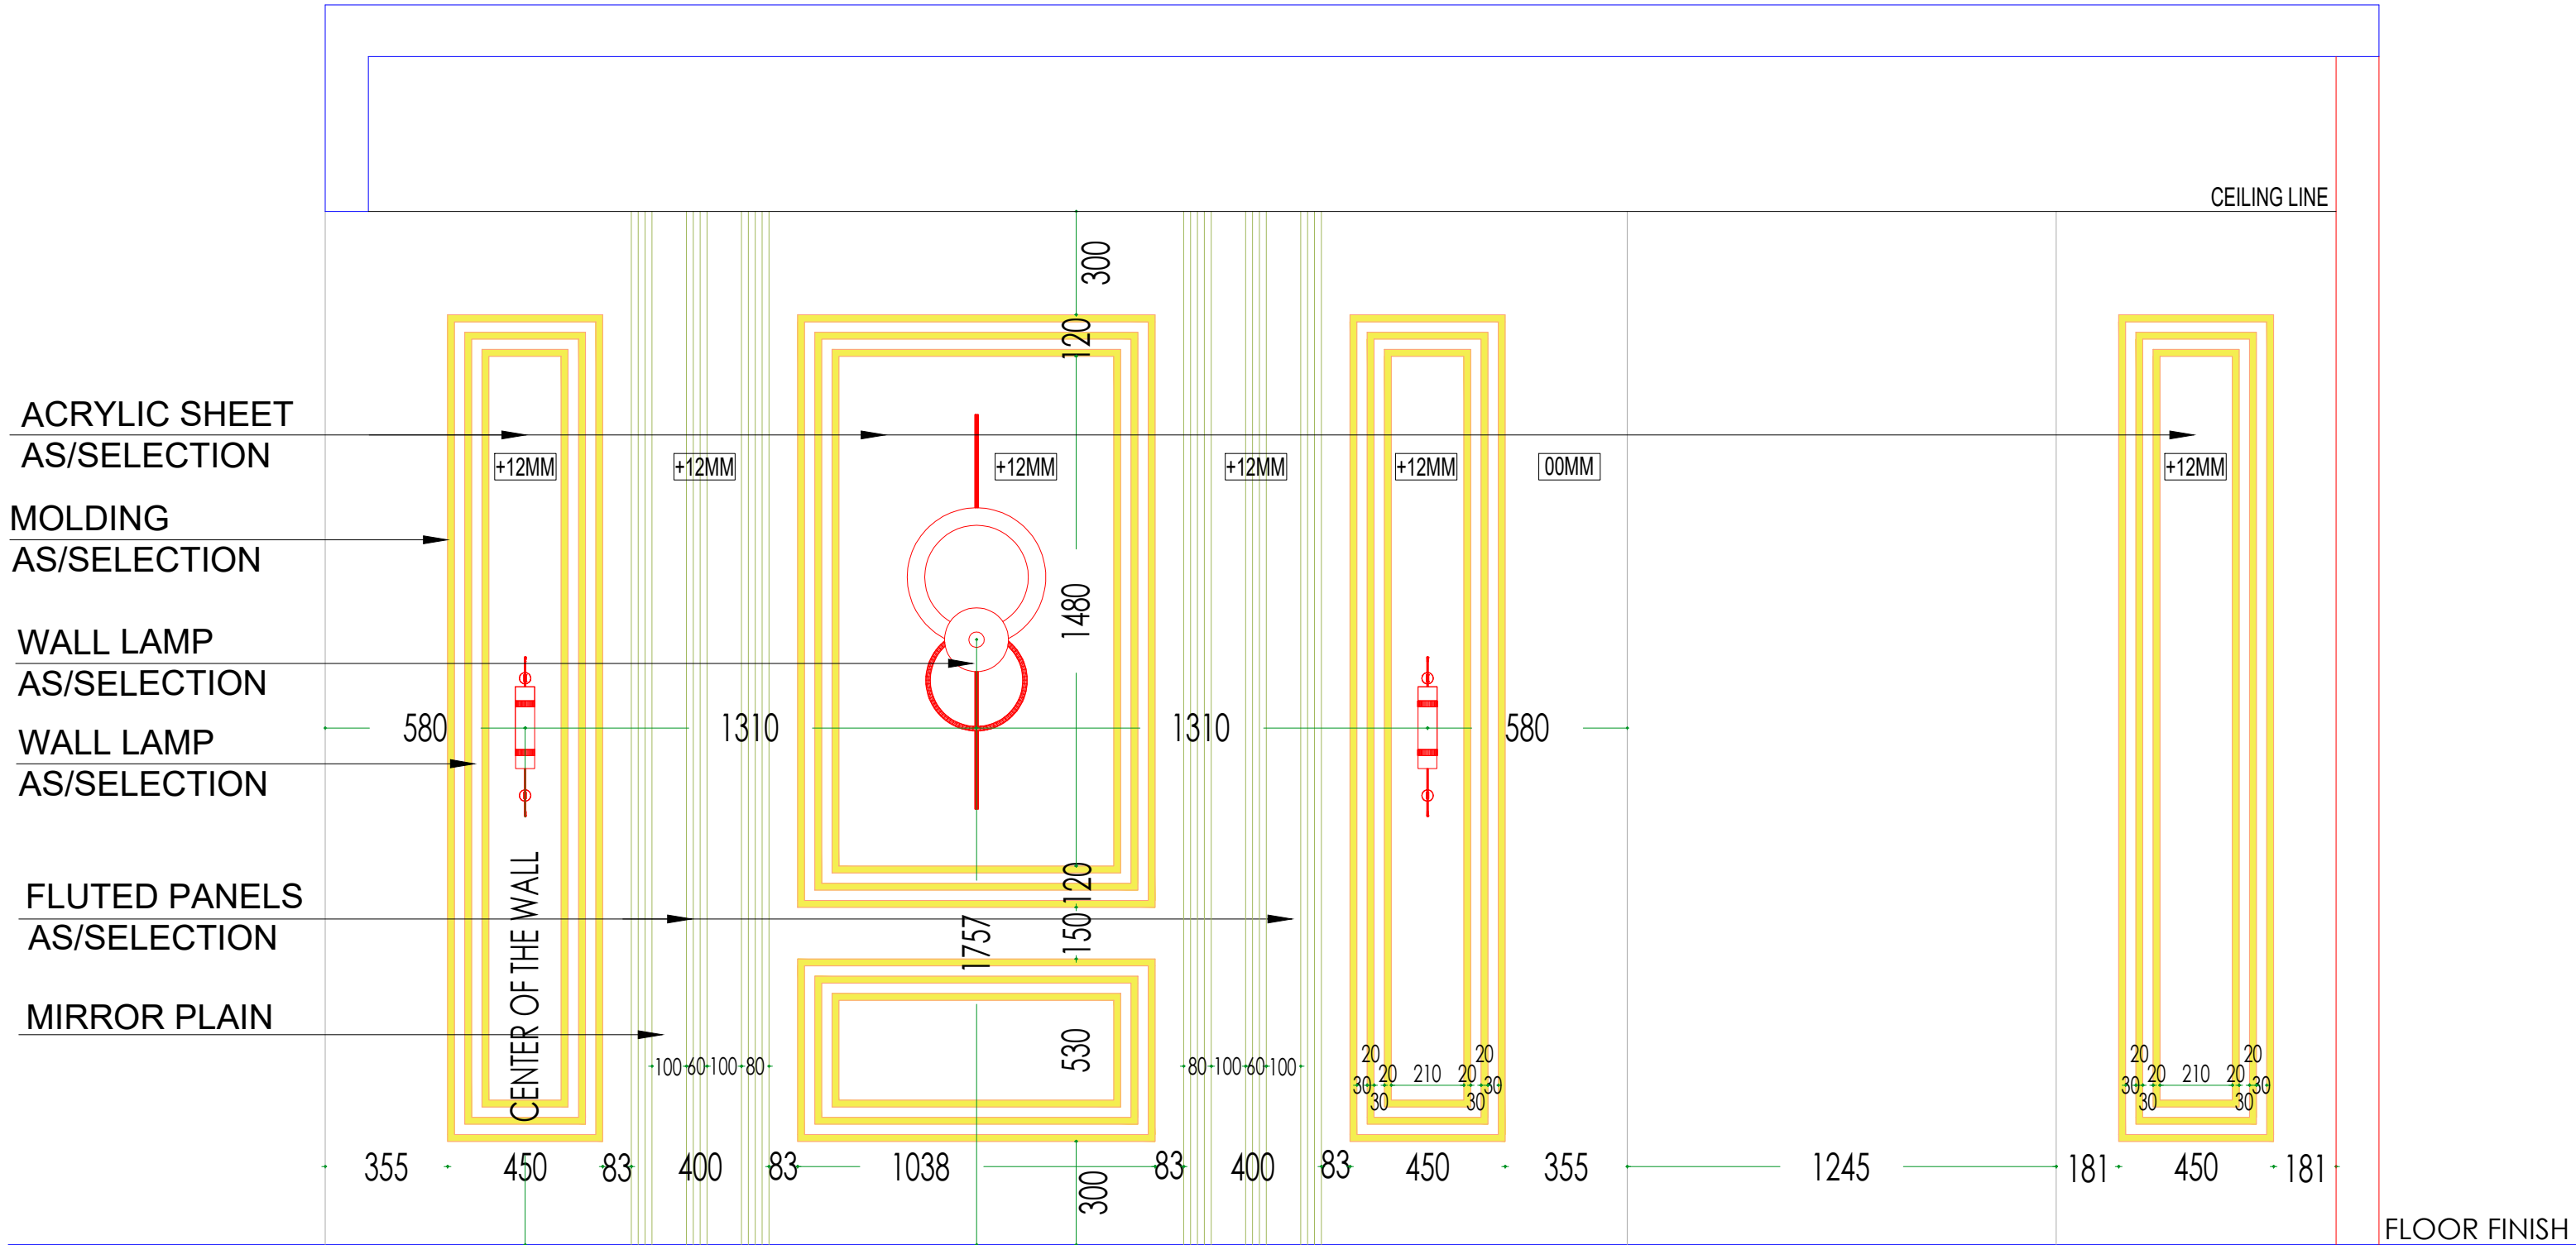

					Client Company & Name
					MR. RAVI TINGRE
					Job Title
					PROPOSED MIX USED BUILDING AT SR.NO. 37 & 39 KONDHWA KH
					Drawing Title
					WALL ELEVATION
					Scale
					N.T.S
					Drawn by
					TEJAL
					Checked by
					Date
					13/12/2025
					Job no.

					Drawing no
					Revision
					Status
REV	DETAILS	DRAWN	CHKD	DATE	


LIVING ROOM & ENTRANCE LOBBY
ELEVATION AT C

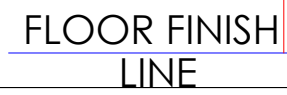

					Client Company & Name
					MR. RAVI TINGRE
					Job Title
					PROPOSED MIX USED BUILDING AT SR.NO. 37 & 39 KONDHWA KH
					Drawing Title Scale
					WALL ELEVATION N.T.S
					Drawn by Checked by Date
					TEJAL 13/12/2025
					Job no. Drawing no Revision

REV	DETAILS	DRAWN	CHKD	DATE	Status

DINING AREA
FIRST ELEVATION

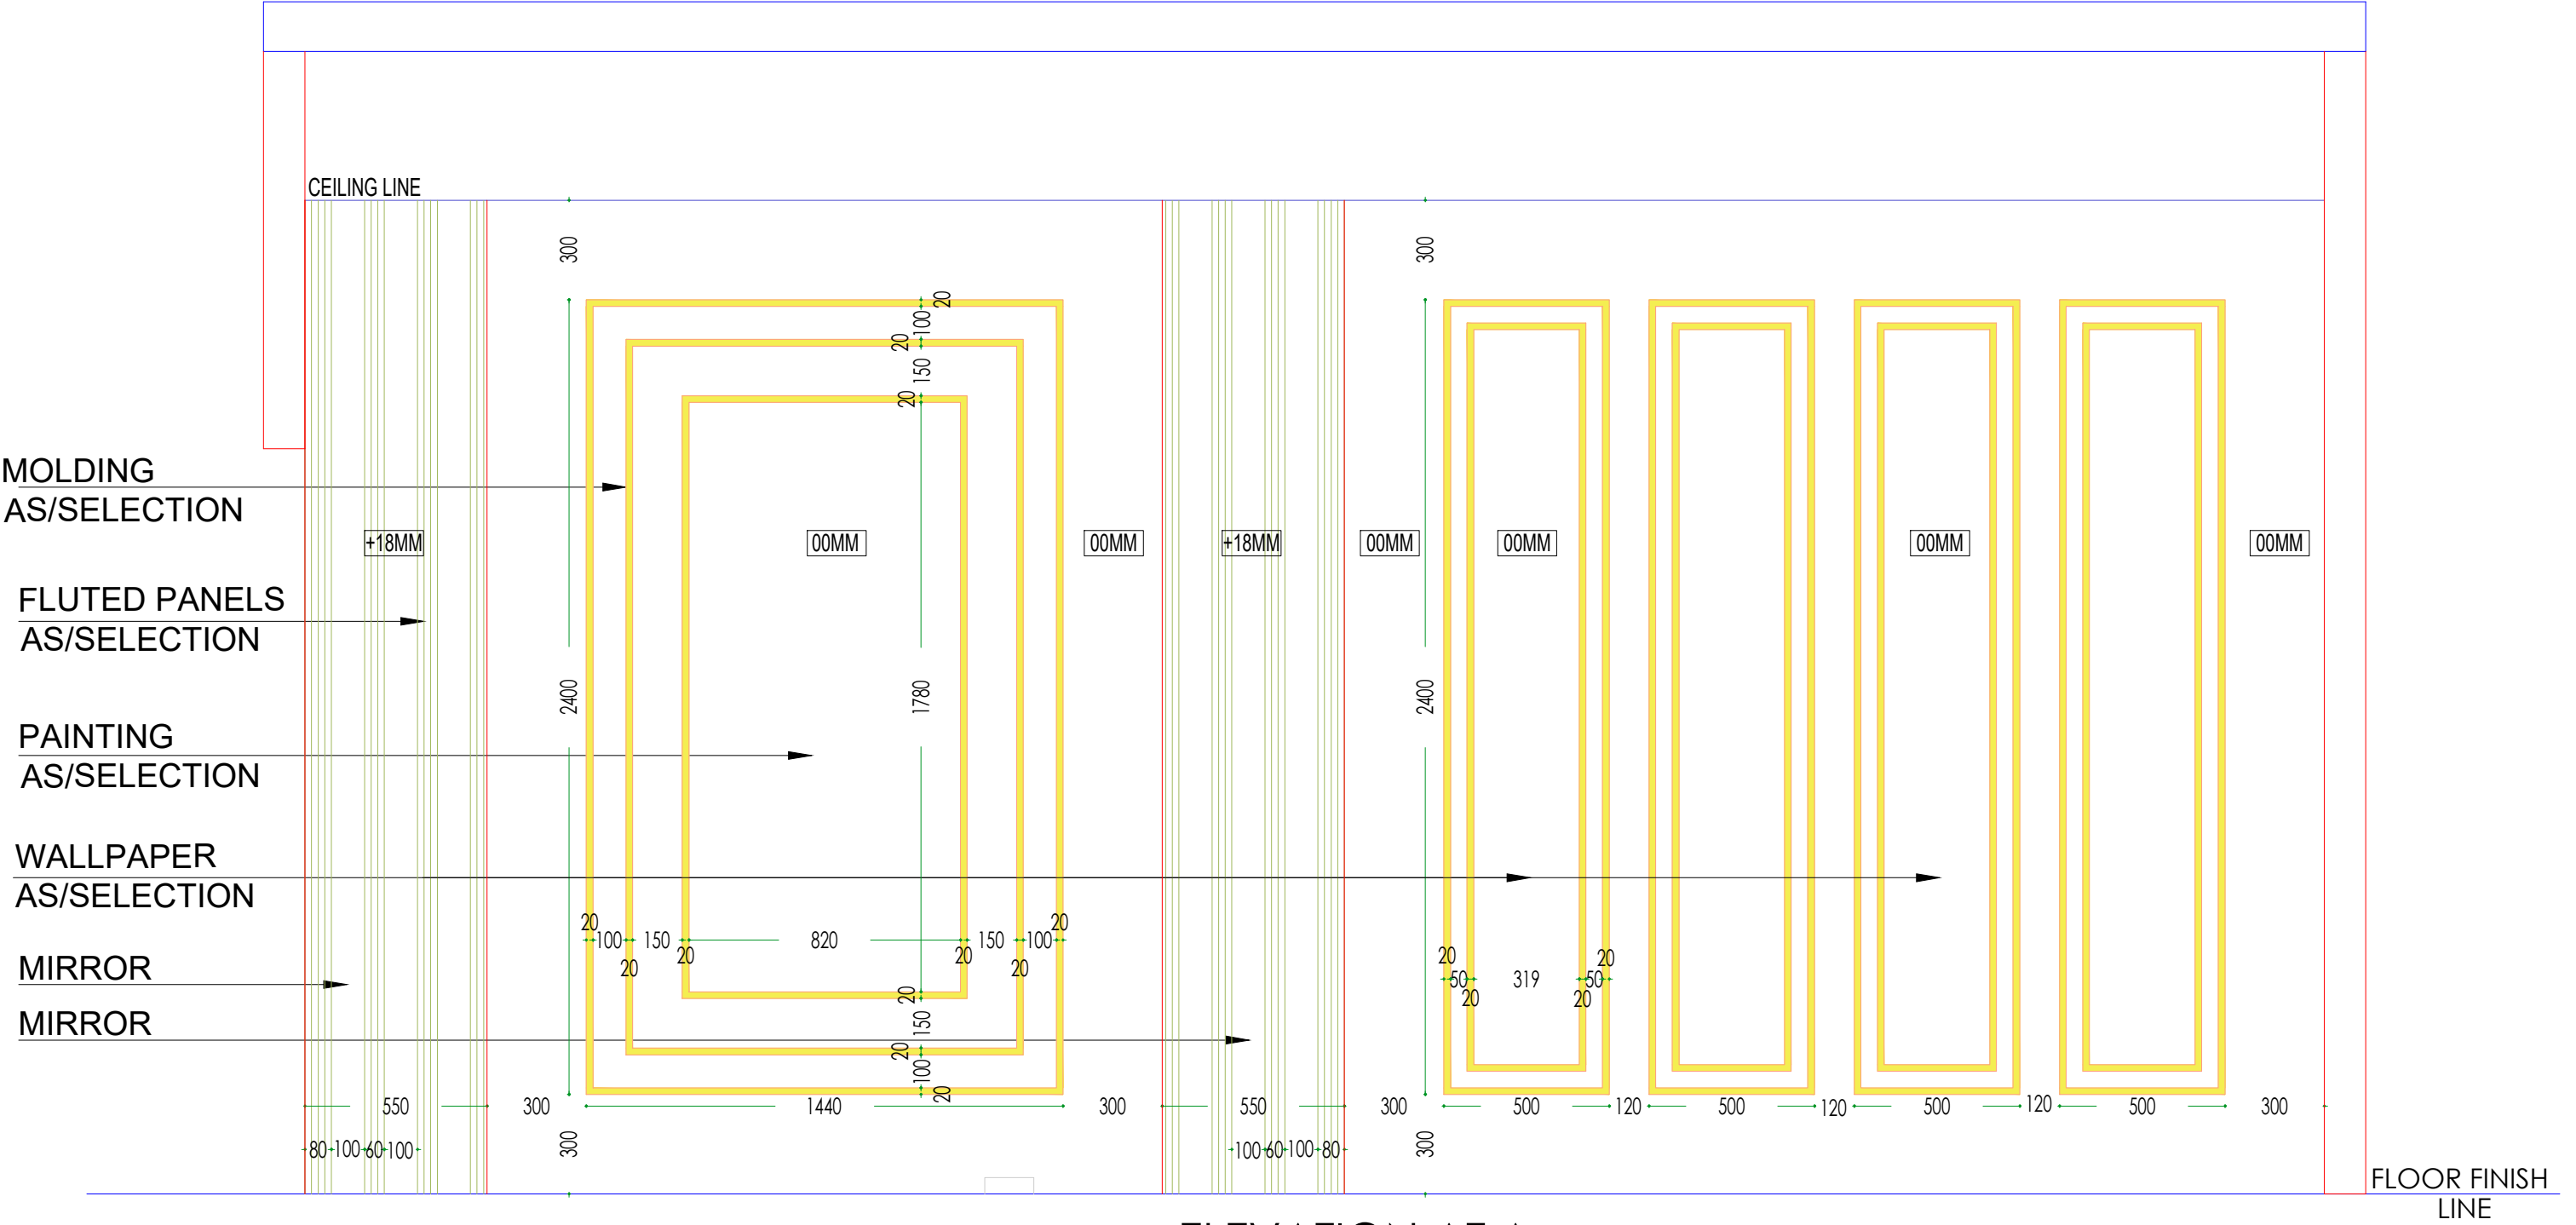


ELEVATION AT A

					Client Company & Name
					MR. RAVI TINGRE
					Job Title
					PROPOSED MIX USED BUILDING AT SR.NO. 37 & 39 KONDHWA KH
					Drawing Title
					WALL ELEVATION
					Scale
					N.T.S
					Drawn by
					TEJAL
					Checked by
					Date
					13/12/2025
					Job no.

					Drawing no
					Revision
					Status
REV	DETAILS	DRAWN	CHKD	DATE	

DINING AREA
2ND ELEVATION

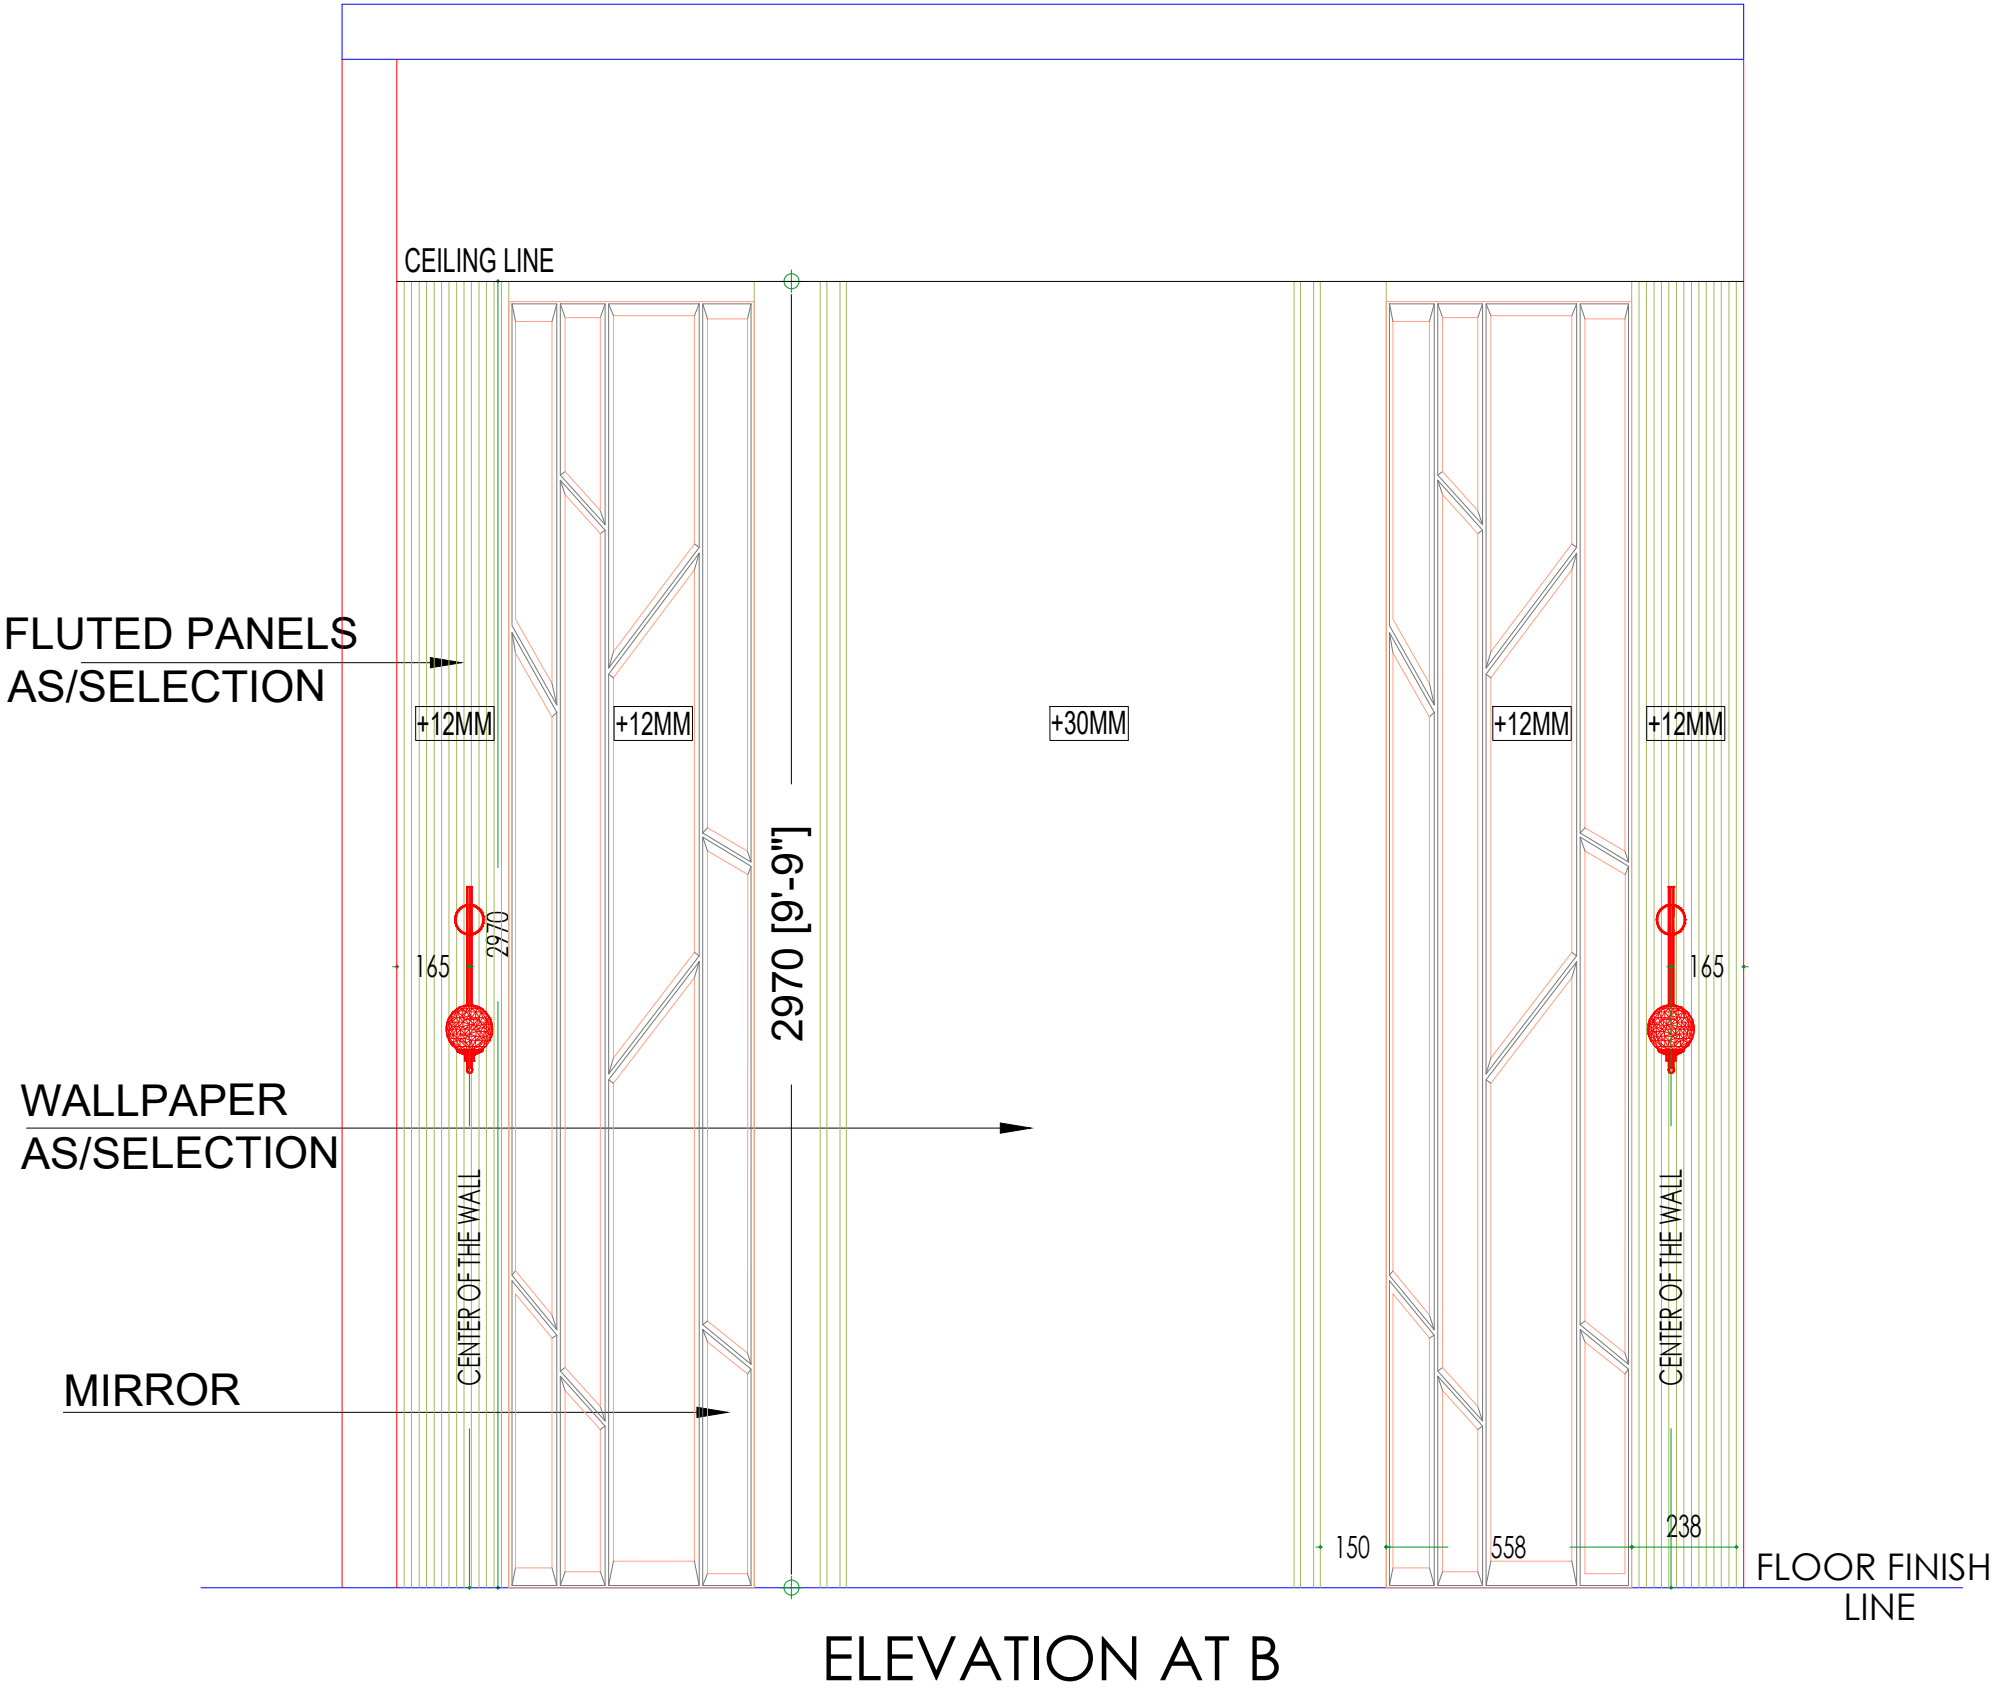


					Client Company & Name
					MR. RAVI TINGRE
					Job Title
					PROPOSED MIX USED BUILDING AT SR.NO. 37 & 39 KONDHWA KH
					Drawing Title
					WALL ELEVATION
					Scale
					N.T.S
					Drawn by
					TEJAL
					Checked by
					Date
					13/12/2025
					Job no.

					Drawing no
					Revision
					Status
REV	DETAILS	DRAWN	CHKD	DATE	

BEDROOM 01


FIRST ELEVATION

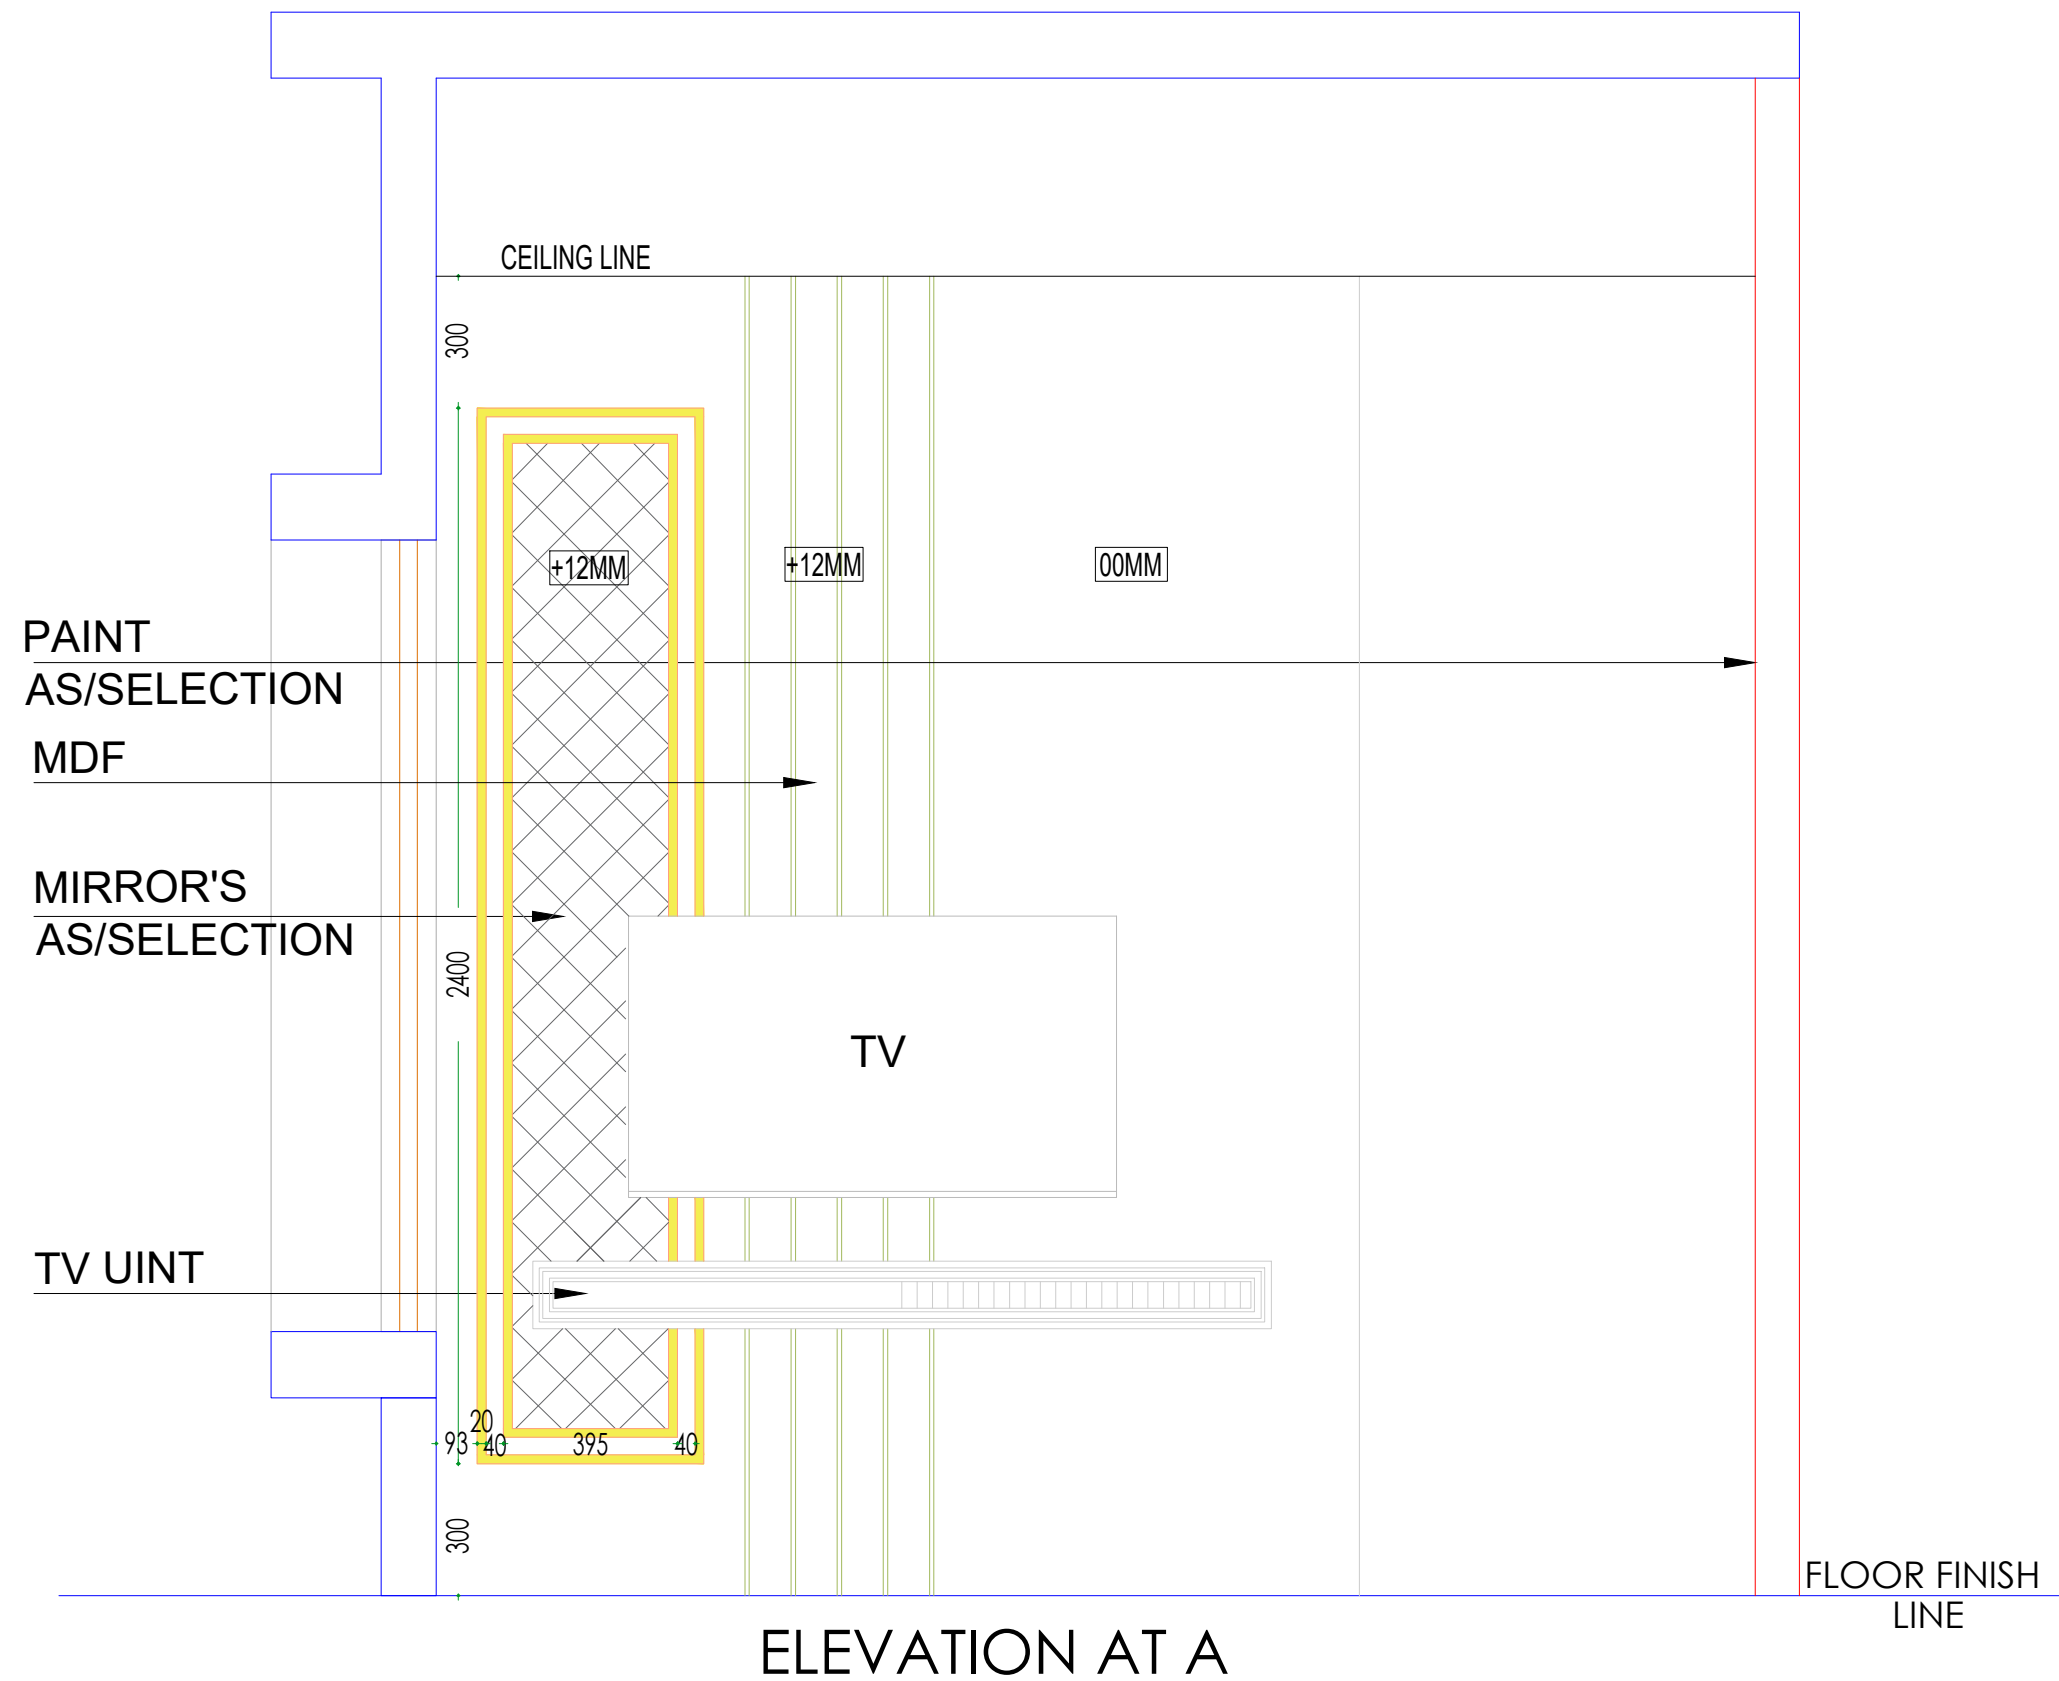

					Client Company & Name
					MR. RAVI TINGRE
					Job Title
					PROPOSED MIX USED BUILDING AT SR.NO. 37 & 39 KONDHWA KH
					Drawing Title Scale
					WALL ELEVATION N.T.S
					Drawn by Checked by Date
					TEJAL 13/12/2025
					Job no. Drawing no Revision

REV	DETAILS	DRAWN	CHKD	DATE	Status


MASTER BEDROOM 01
ELEVATION AT A

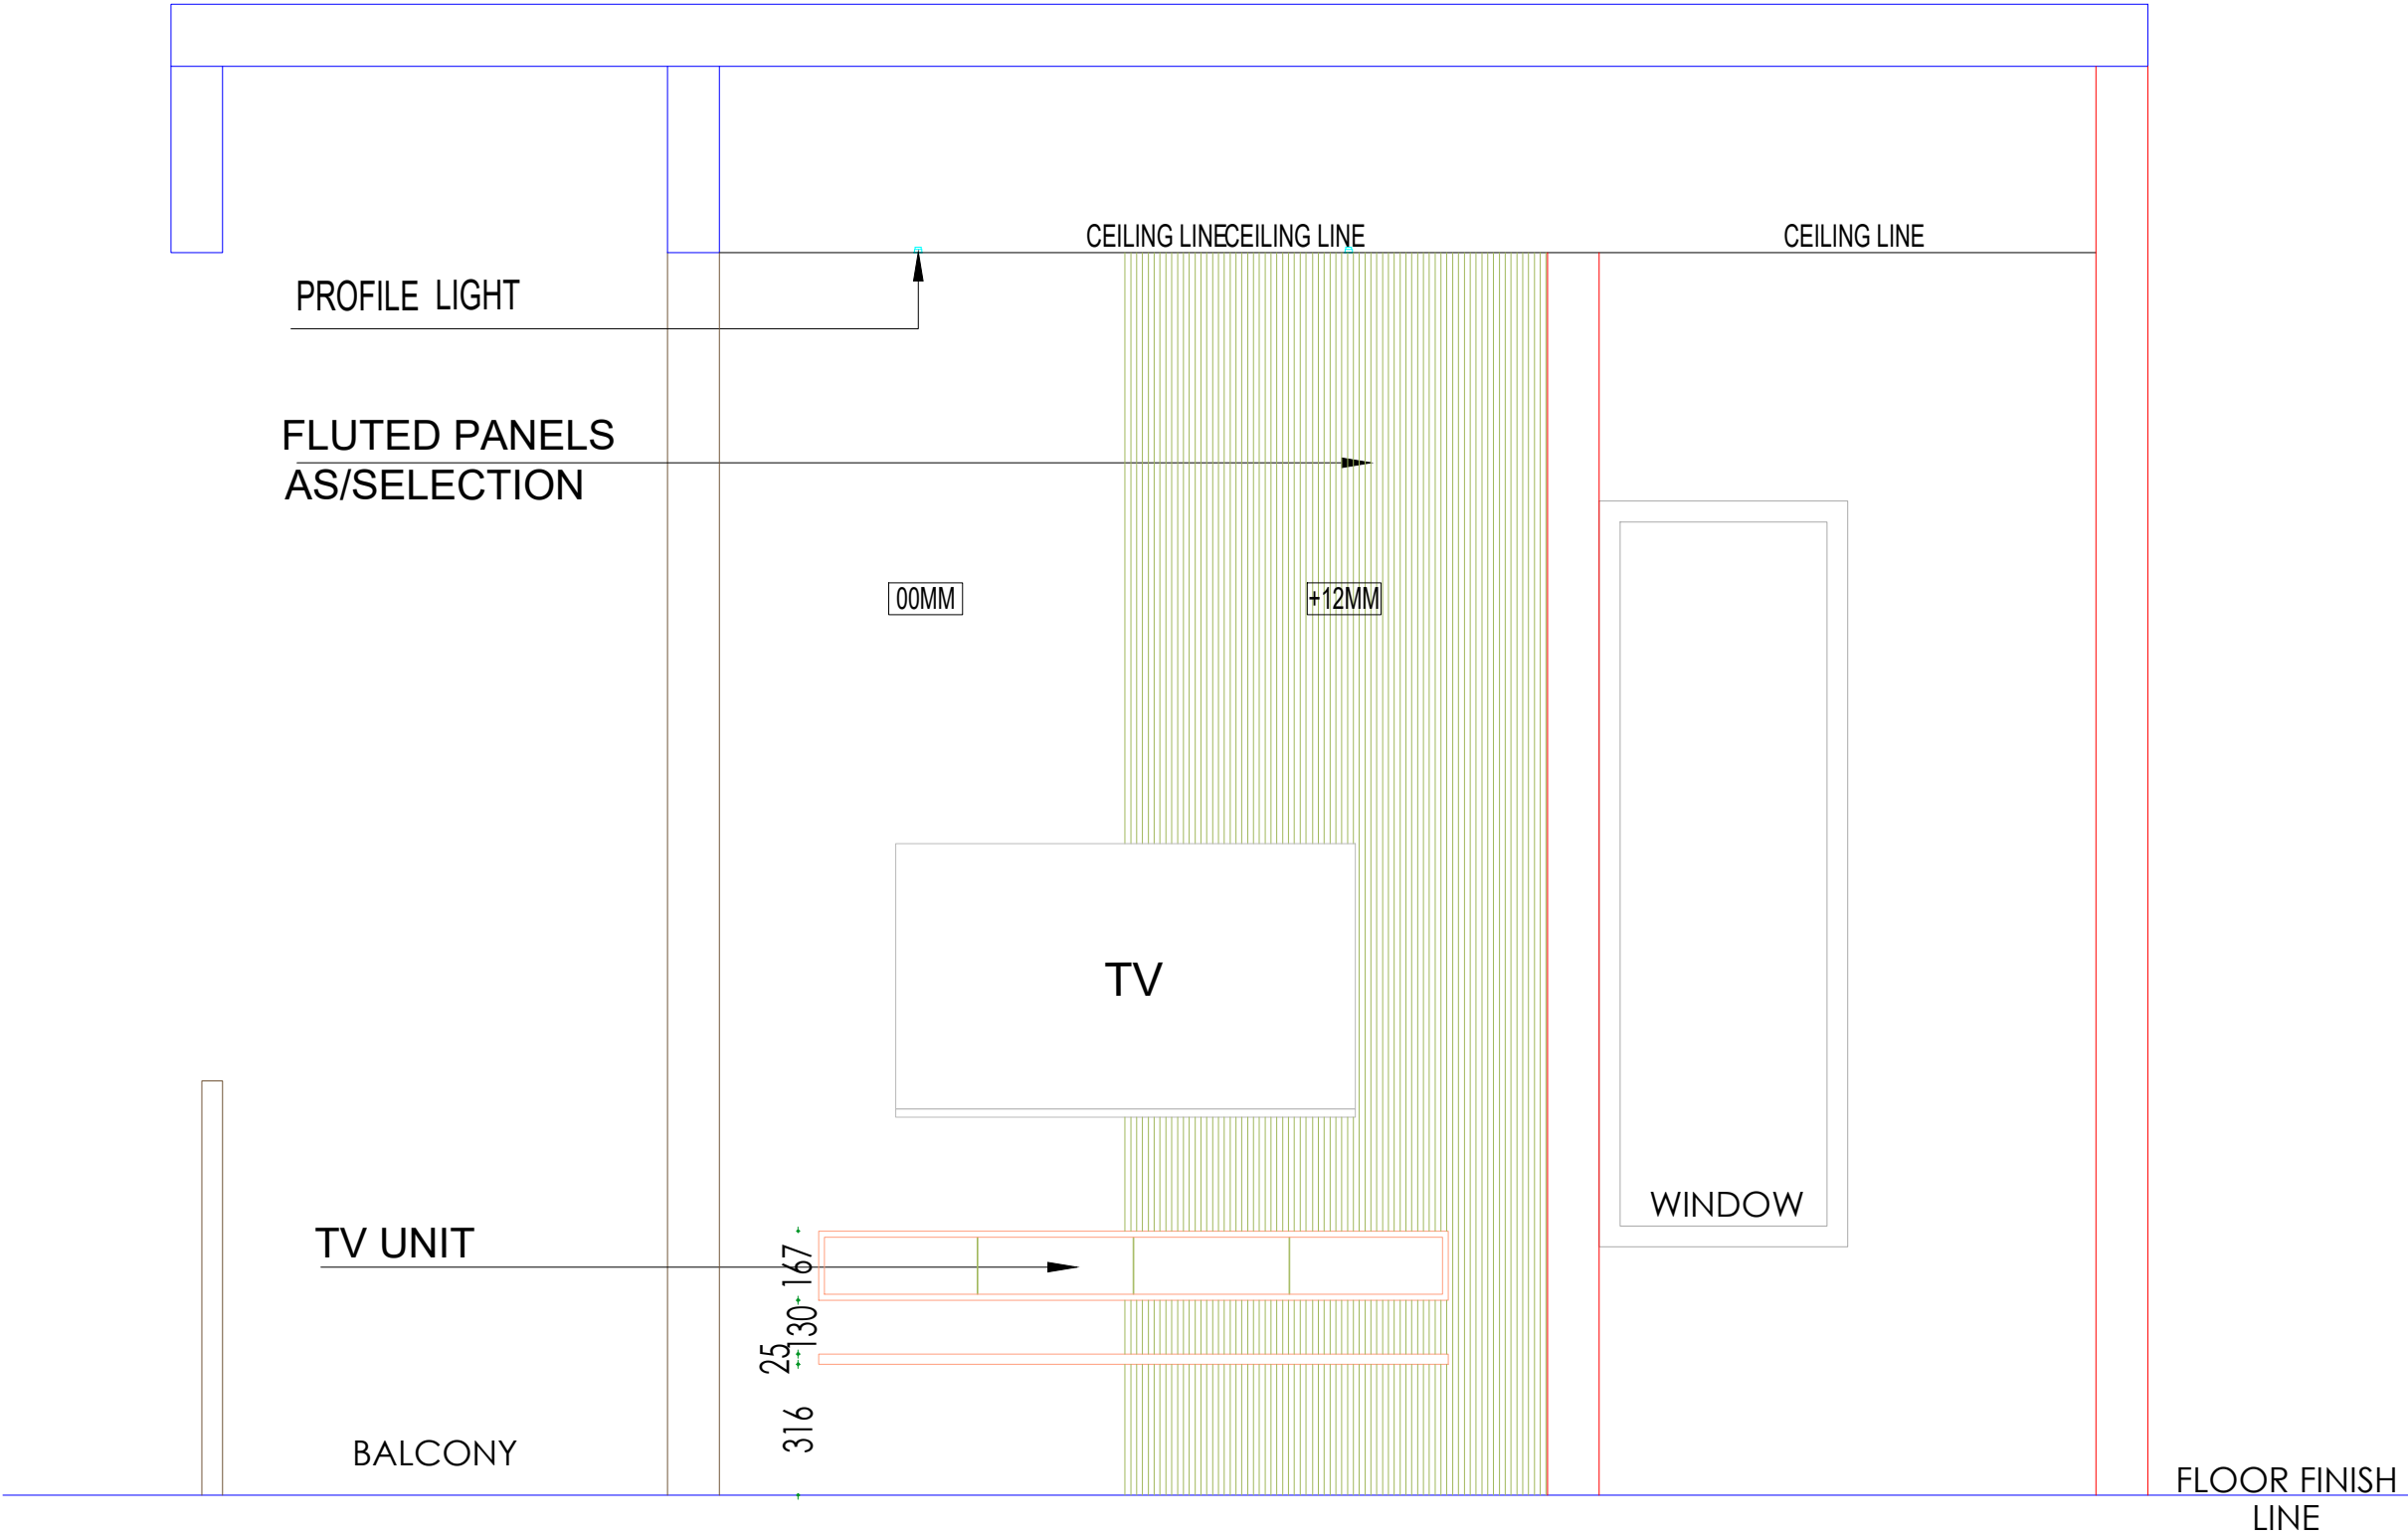

					Client Company & Name
					MR. RAVI TINGRE
					Job Title
					PROPOSED MIX USED BUILDING AT SR.NO. 37 & 39 KONDHWA KH
					Drawing Title
					WALL ELEVATION
					Scale
					N.T.S
					Drawn by
					TEJAL
					Checked by
					Date
					13/12/2025
					Job no.

					Drawing no
					Revision
					Status
REV	DETAILS	DRAWN	CHKD	DATE	


MASTER BEDROOM 02
ELEVATION A

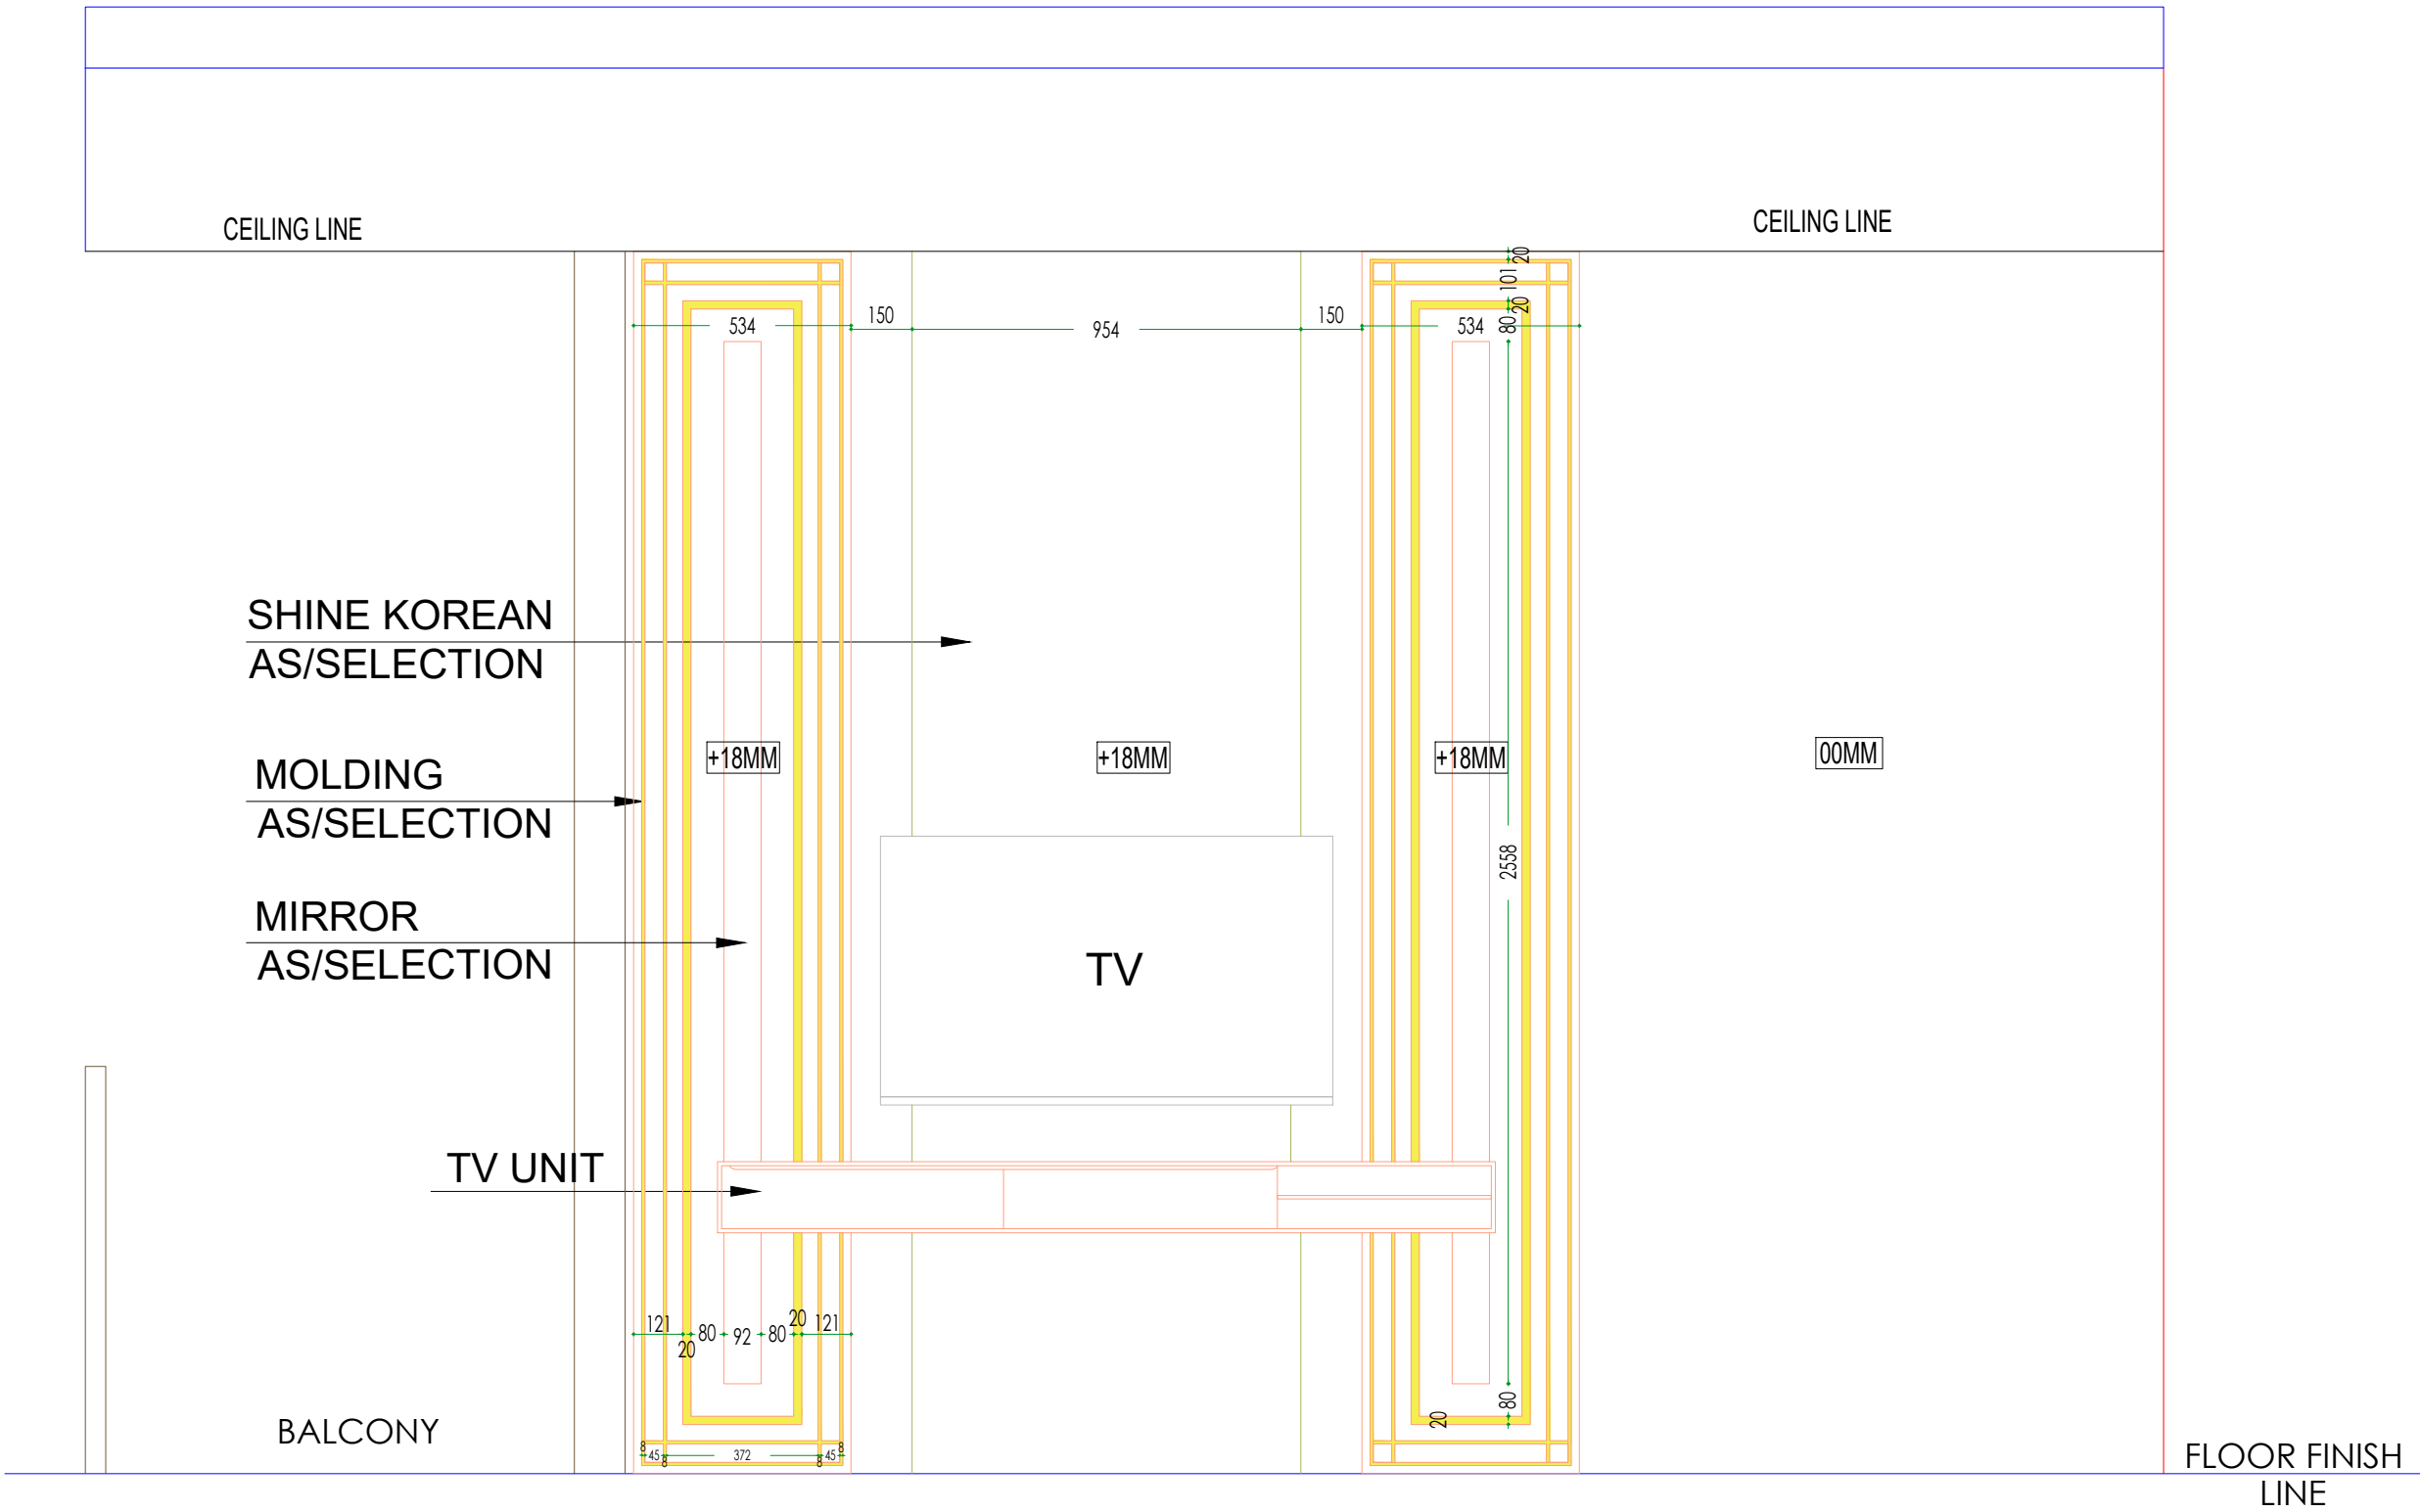

					Client Company & Name
					MR. RAVI TINGRE
					Job Title
					PROPOSED MIX USED BUILDING AT SR.NO. 37 & 39 KONDHWA KH
					Drawing Title
					WALL ELEVATION
					Scale
					N.T.S
					Drawn by
					TEJAL
					Checked by
					Date
					13/12/2025
					Job no.

					Drawing no
					Revision
					Status
REV	DETAILS	DRAWN	CHKD	DATE	

MASTER BEDROOM 02
ELEVATION B

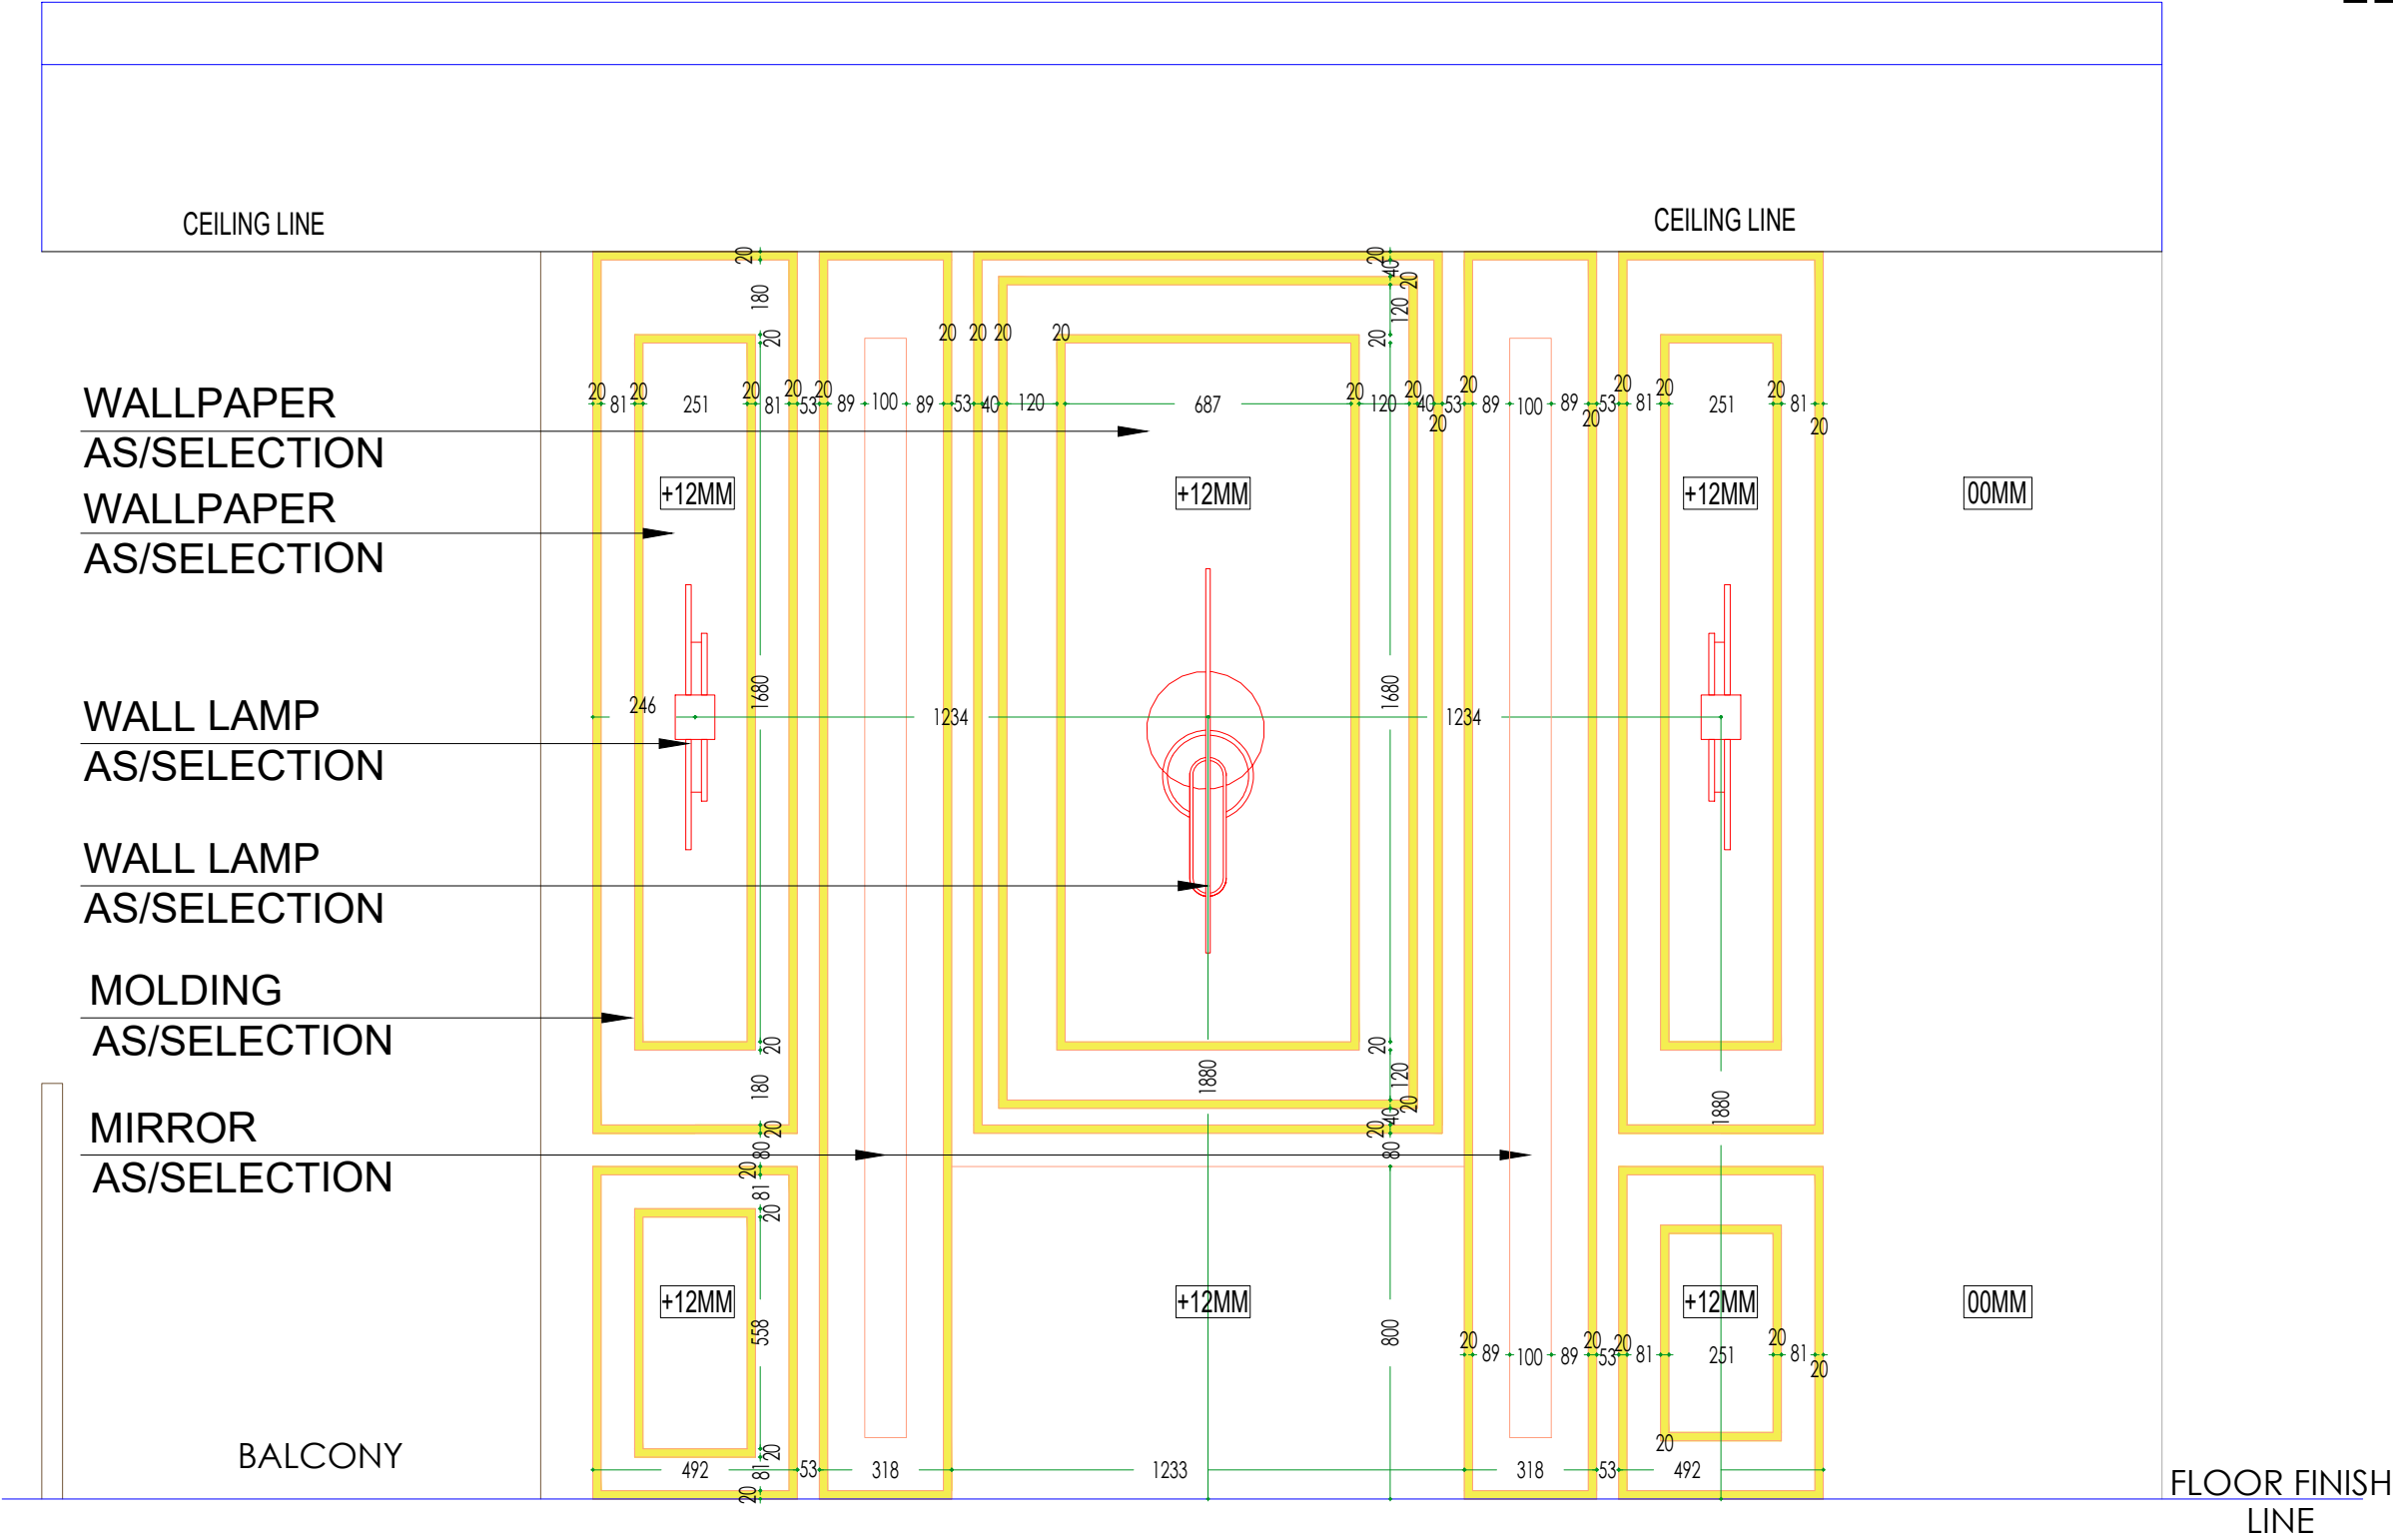

					Client Company & Name
					MR. RAVI TINGRE
					Job Title
					PROPOSED MIX USED BUILDING AT SR.NO. 37 & 39 KONDHWA KH
					Drawing Title
					WALL ELEVATION
					Scale
					N.T.S
					Drawn by
					TEJAL
					Checked by
					Date
					13/12/2025
					Job no.

					Drawing no
					Revision
					Status
REV	DETAILS	DRAWN	CHKD	DATE	