


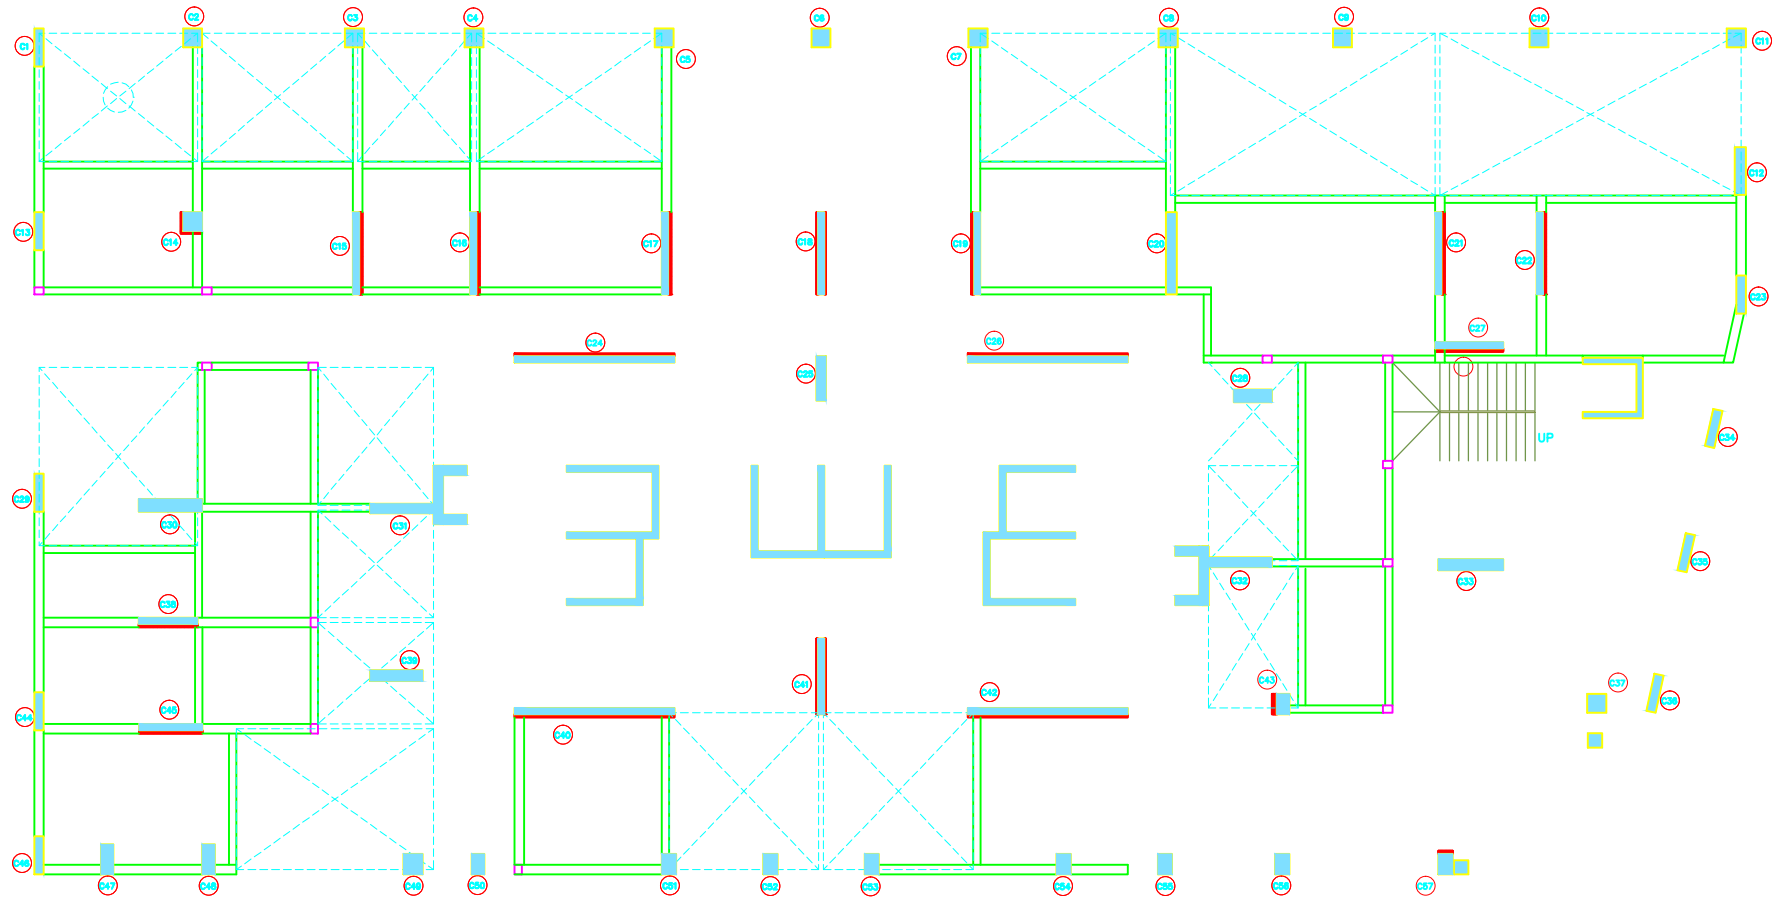

LAYOUT OF MEZZANINE SLAB & BEAM